


PROFIL 1

G2,PIS

S = 0.000
 ZTN = 212.286
 ZPRO= 212.286

ECHS=1/ 250
 ECHZ=1/ 250
 PC = 208.0
 LICENCE , 1570

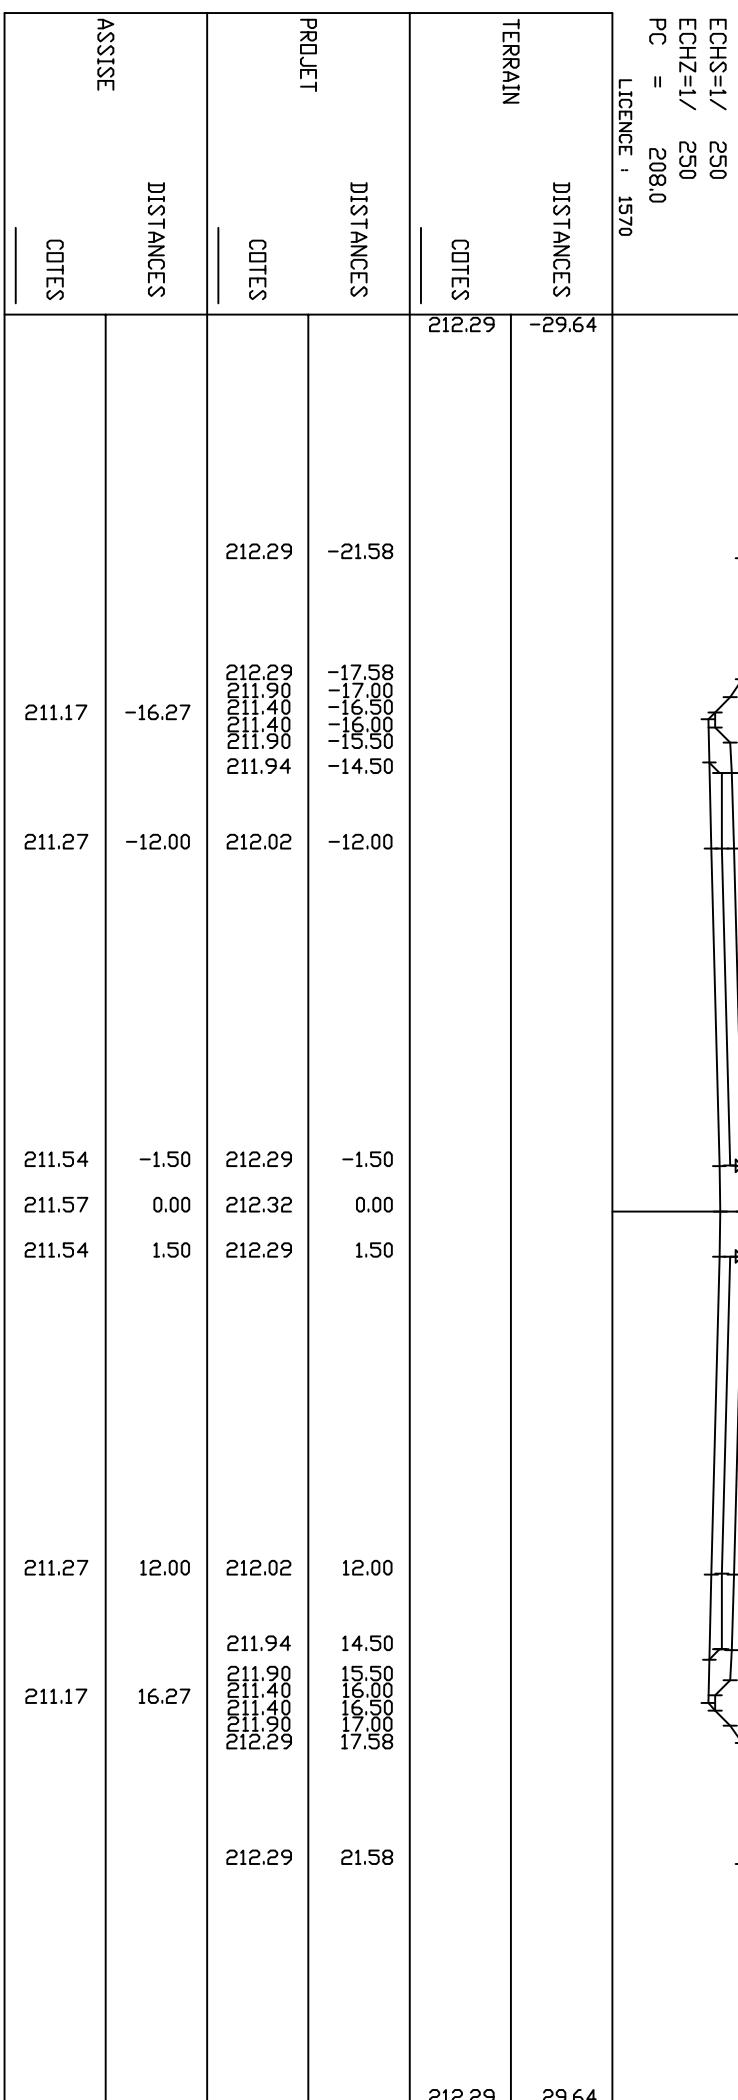


PROFIL

۲۰

G2,P1S

S = 25.000
 ZTN = 214.478
 ZPRD = 211.706

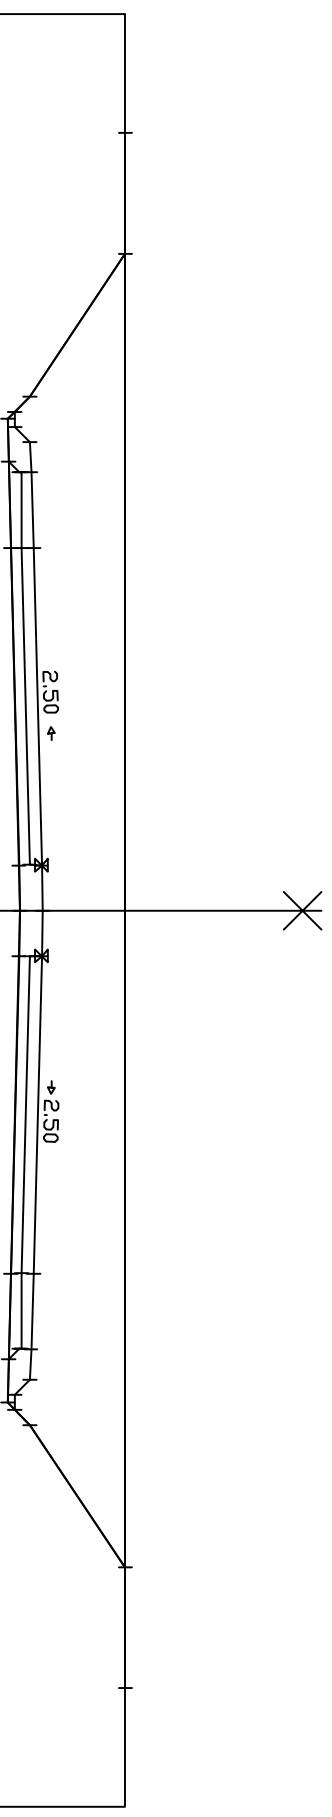


TERRAIN	DISTANCES			
	COTES	DISTANCES	COTES	DISTANCES
PROJET	COTES	DISTANCES	COTES	DISTANCES
ASSISE	COTES	DISTANCES	COTES	DISTANCES
			214.48	-29.64
			214.48	-25.72
			214.48	-21.72
			211.32	-17.00
			210.82	-16.50
			210.82	-16.00
			211.32	-15.50
			211.36	-14.50
210.59	-16.27	211.44	-12.00	
210.69	-12.00	211.71	-1.50	
210.96	0.00	211.74	0.00	
210.96	1.50	211.71	1.50	
210.69	12.00	211.44	12.00	
210.59	16.27	211.36	14.50	
		211.32	15.50	
		210.82	16.00	
		210.82	16.50	
		211.32	17.00	
		214.48	21.72	
		214.48	25.72	
			214.48	29.64

PROFIL 3

G2,PIS

S = 50000
 ZTN = 214.076
 ZPRD = 211.126

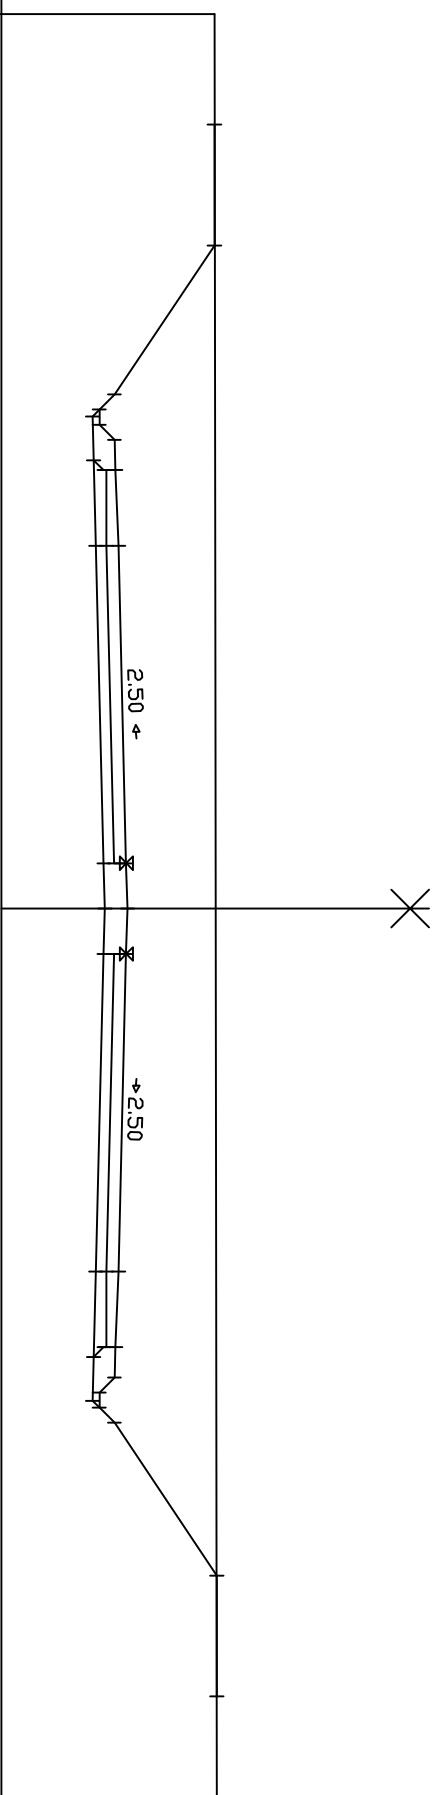


TERRAIN				LICENCE : 1570
PROJET	COTES	DISTANCES		COTES
		DISTANCES	COTES	
ASSISE	COTES	214.03	-29.58	
210.01	-16.27	214.04	-25.93	
		214.04	-21.93	
		210.74	-17.00	
		210.24	-16.50	
		210.24	-16.00	
		210.74	-15.50	
		210.78	-14.50	
210.11	-12.00	210.86	-12.00	
210.38	-1.50	211.13	-1.50	
210.41	0.00	211.16	0.00	
210.38	1.50	211.13	1.50	
210.11	12.00	210.86	12.00	
210.01	16.27	210.78	14.50	
		210.74	15.50	
		210.24	16.00	
		210.24	16.50	
		210.74	17.00	
		214.12	22.05	
		214.12	26.05	
				214.12 29.70

PROFIL 4

G2.PIS

S = 75,000
ZTN = 211,725
ZPRO= 210,546

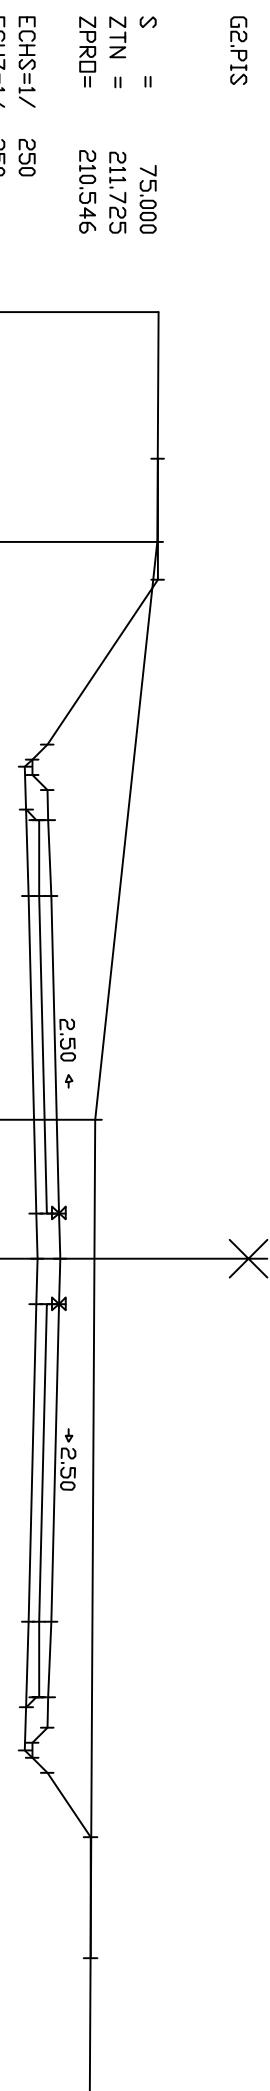


ASSISE		DISTANCES		TERRAIN	
COTES	DISTANCES	COTES	DISTANCES	COTES	DISTANCES
209.43	-16.27	213.81	-26.45	213.85	-31.29
209.53	-12.00	213.81	-22.45	213.79	-23.69
209.80	-1.50	210.16	-17.00		
209.83	0.00	209.66	-16.50		
209.80	1.50	209.66	-16.00		
		210.16	-15.50		
		210.20	-14.50		
209.53	12.00	210.28	-12.00	211.75	-4.59
209.43	16.27	210.55	-1.50		
209.80	0.00	210.58	0.00		
209.80	1.50	210.55	1.50		
209.53	12.00	210.28	12.00		
209.43	16.27	210.20	14.50		
		210.16	15.50		
		209.66	16.00		
		209.66	16.50		
		210.16	17.00		
		211.59	19.15		
		211.59	23.15		
				211.57	27.99

PROFIL 5


G2,PIS

S = 100.00
ZTN = 210.167
ZPRO = 209.966

ECHS=1/ 250
ECHZ=1/ 250
PC = 206.0
LICENCE : 1570

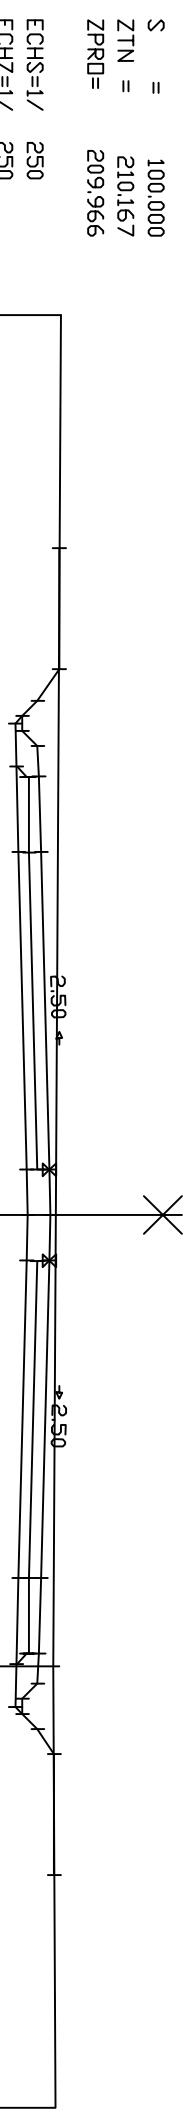

		DISTANCES		TERRAIN	
		COTES		DISTANCES	
		COTES		PROJECT	
		DISTANCES	COTES	DISTANCES	COTES
ASSISE	COTES				
208.85	-16.27	210.29	-22.07	210.34	-29.76
208.95	-12.00	210.29	-18.07		
		209.58	-17.00		
		209.08	-16.50		
		209.08	-16.00		
		209.58	-15.50		
		209.62	-14.50		
208.85	-1.50	209.70	-12.00		
209.22	0.00	209.97	-1.50		
209.22	1.50	210.00	0.00		
209.22	1.50	209.97	1.50		
208.95	12.00	209.70	12.00		
208.85	16.27	209.62	14.50	210.08	14.90
		209.58	15.50		
		209.08	16.00		
		209.08	16.50		
		209.58	17.00		
		210.13	17.82		
		210.13	21.82		
				210.17	29.51

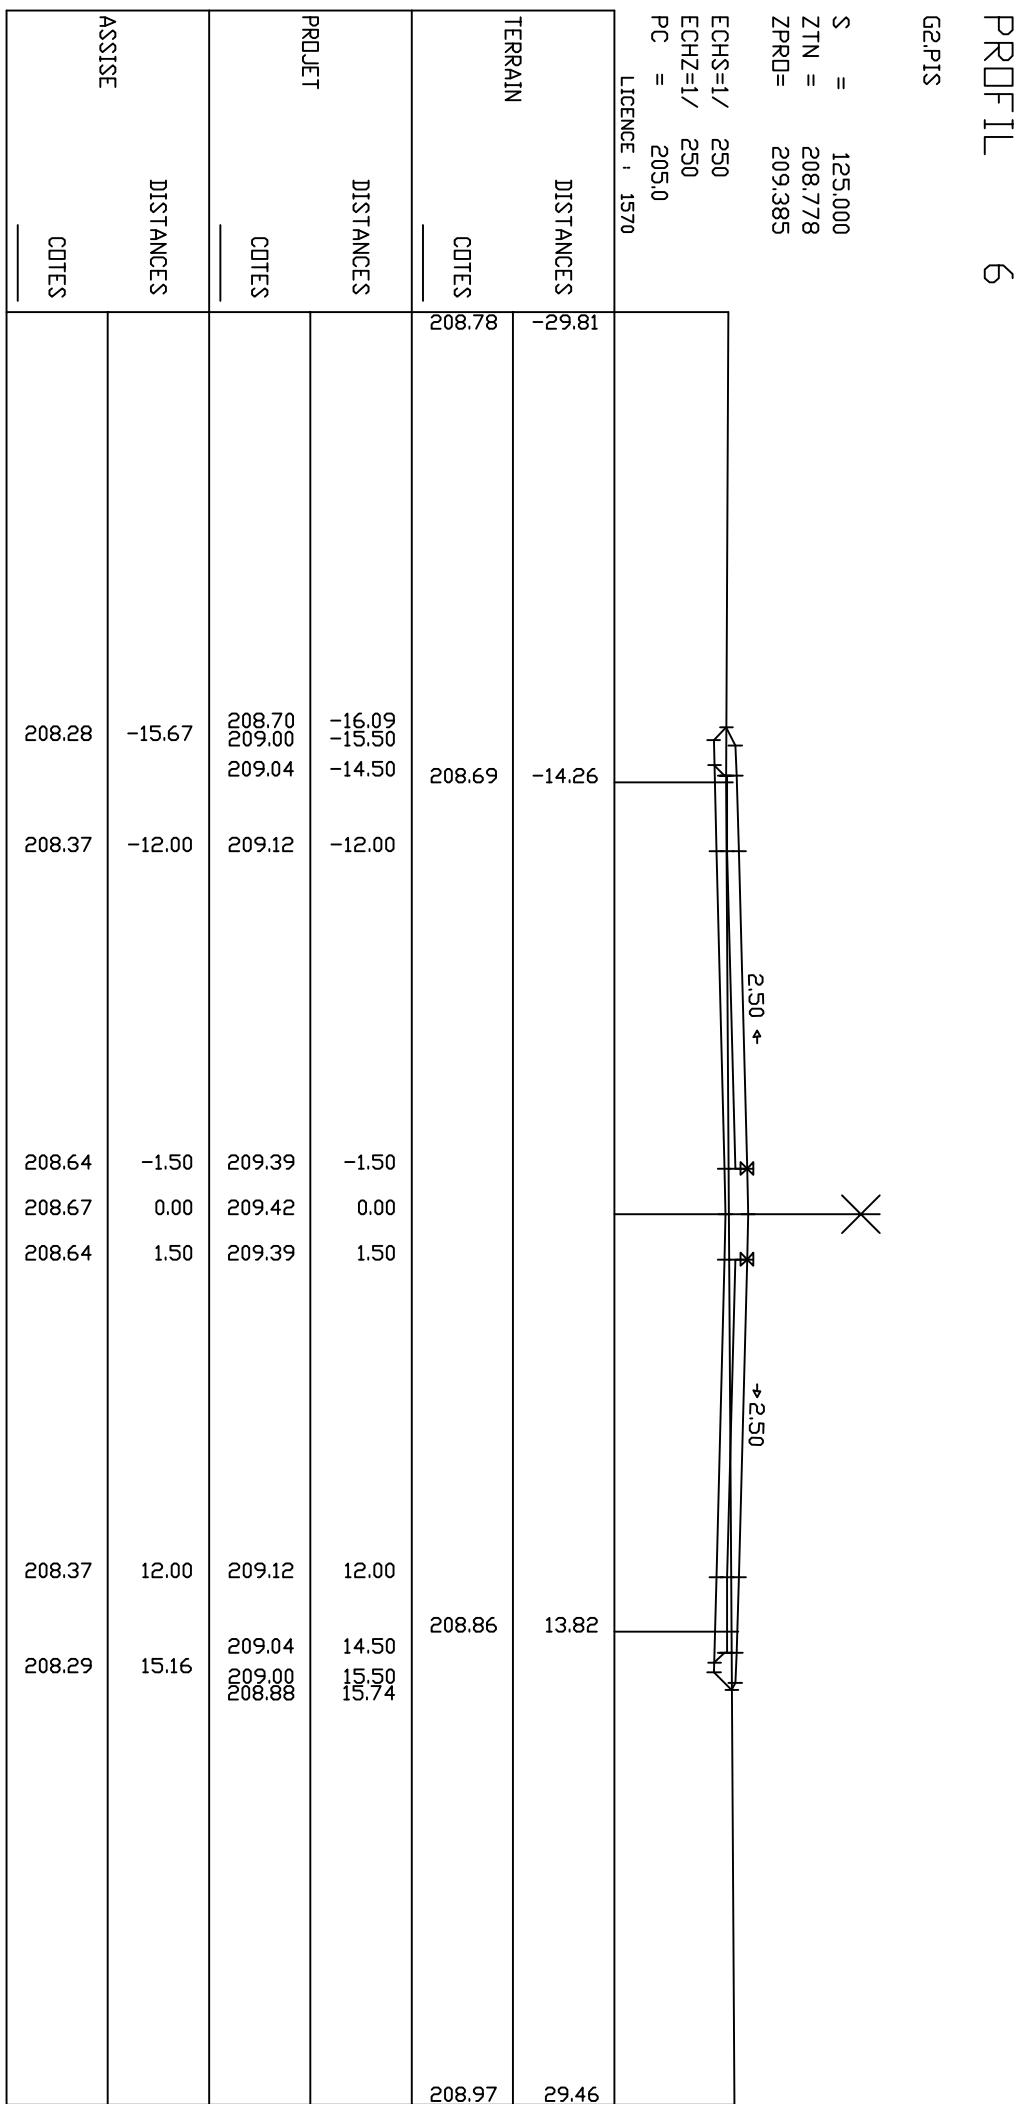

PROFIL 7

G2PIS

S = 150.000
 ZTN = 207,448
 ZPRO= 208,805

ECH\$=1/
 ECHZ=1/
 PC = 204,0
 LICENCE , 1570

ASSISE	DISTANCES	TERRAIN		DISTANCES COTES	DISTANCES COTES	DISTANCES COTES
		PROJECT	COTES			
207.67	-16.99	207.38	-17.56			
		208.42	-15.50			
		208.46	-14.50			
207.79	-12.00	208.54	-12.00			
208.06	-1.50	208.81	-1.50			
208.09	0.00	208.84	0.00			
208.06	1.50	208.81	1.50			
207.79	12.00	208.54	12.00			
		208.46	14.50			
		208.42	15.50			
207.67	16.99	207.51	17.31			
				207.56	29.51	

PROFIL 8

G2PIS

S = 175.000
 ZTN = 206.157
 ZPRD= 208.225

ECHS=1/
 ECHZ=1/
 PC = 203.0
 LICENCE , 1570

TERRAIN DISTANCES

COTES

206.23 -29.66

206.21 -21.15

206.05 -8.35

206.26 8.63

206.17 25.20

206.19 29.61

DISTANCES

DISTANCES

PROJET

COTES

206.18 -18.80

207.84

207.88

207.96

-15.50

-14.50

-12.00

206.23

206.21

206.05

206.26

206.17

206.19

206.18

207.88

207.84

207.96

12.00

207.88

207.84

206.21

14.50

15.50

18.75

206.23

0.00

208.26

1.50

208.23

208.23

-1.50

0.00

1.50

207.48

207.51

207.48

207.21

207.09

207.21

207.09

207.48

207.51

207.48

207.21

207.09

207.21

207.09

207.48

207.51

207.48

207.21

207.09

207.21

207.09

207.48

207.51

207.48

207.21

207.09

207.21

207.09

207.48

207.51

207.48

207.21

207.09

207.21

207.09

207.48

207.51

207.48

207.21

207.09

207.21

207.09

207.48

207.51

207.48

207.21

207.09

207.21

207.09

207.48

207.51

207.48

207.21

207.09

207.21

207.09

207.48

207.51

207.48

207.21

207.09

207.21

207.09

207.48

207.51

207.48

207.21

207.09

207.21

207.09

207.48

207.51

207.48

207.21

207.09

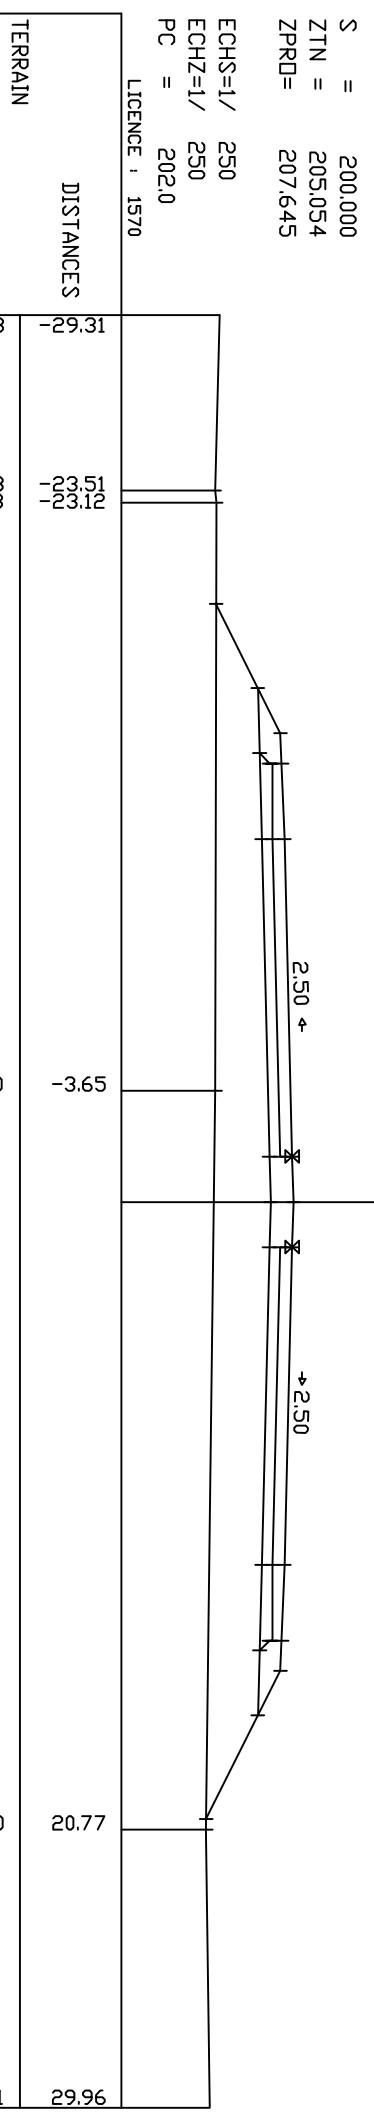

ASSISE COTES	DISTANCES COTES	PROJECT	
		DISTANCES	COTES
206.51	-16.99	205.13	-19.76
		207.25	-15.50
		207.29	-14.50
206.63	-12.00	207.38	-12.00
206.89	-1.50	207.64	-1.50
206.93	0.00	207.68	0.00
206.89	1.50	207.64	1.50
206.63	12.00	207.38	12.00
		207.29	14.50
		207.25	15.50
206.51	16.99	204.80	20.40

PROFIL 10

G2PIS

S = 225.000
 ZTN = 203.939
 ZPRO= 207.065

ECHS=1/
 ECHZ=1/
 PC = 2010
 LICENCE , 1570

TERRAIN

DISTANCES

COTES

204.32 -29.54

DISTANCES

COTES

204.05 -20.23

DISTANCES

COTES

203.98 -15.37

DISTANCES

COTES

203.99 -15.33

DISTANCES

COTES

203.97 -11.79

DISTANCES

COTES

203.90 -5.54

DISTANCES

COTES

204.00 8.50

DISTANCES

COTES

203.95 29.73

ASSISE	DISTANCES	COTES	PROJECT		DISTANCES		COTES		DISTANCES		COTES	
			DISTANCES	COTES	DISTANCES	COTES	DISTANCES	COTES	DISTANCES	COTES	DISTANCES	COTES
205.93	-16.99	206.67	204.07	-20.71	204.05	203.98	203.99	203.97	203.90	204.00	203.95	29.73
206.05	-12.00	206.71	206.80	-12.00	203.97	203.99	203.98	203.97	203.90	204.00	203.95	29.73
206.31	-1.50	207.06	207.06	-1.50	203.97	203.99	203.98	203.97	203.90	204.00	203.95	29.73
206.35	0.00	207.10	207.10	0.00	203.97	203.99	203.98	203.97	203.90	204.00	203.95	29.73
206.31	1.50	207.06	207.06	1.50	203.97	203.99	203.98	203.97	203.90	204.00	203.95	29.73
206.05	12.00	206.71	206.80	12.00	203.97	203.99	203.98	203.97	203.90	204.00	203.95	29.73
205.93	16.99	206.67	203.97	20.90	203.97	203.99	203.98	203.97	203.90	204.00	203.95	29.73

PROFIL 11

G2PIS

S = 250.000
 ZTN = 202.942
 ZPRO= 206.485


ECHS=1/
 ECHZ=1/
 PC = 250
 PC = 200.0
 LICENCE , 1570


		TERRAIN		DISTANCES			
		DISTANCES		COTES			
		PROJECT		COTES			
ASSISE	DISTANCES	COTES	COTES	COTES	COTES		
205.35	-16.99	206.09 206.13	203.14	-21.41	203.27	-29.26	
205.47	-12.00	206.22	206.22	-12.00	202.91 202.99	-6.89 -6.71	
205.73	-1.50	206.48	206.48	-1.50			
205.77	0.00	206.52		0.00			
205.73	1.50	206.48		1.50			
205.47	12.00	206.22	206.22	12.00	202.86	13.00	
205.35	16.99	206.13 206.09	202.76	14.50 15.50	202.68	30.02	

PROFIL 12
G2PIS

S = 275,000
ZTN = 201,864
ZPRD= 205,904

LICENCE : 1570

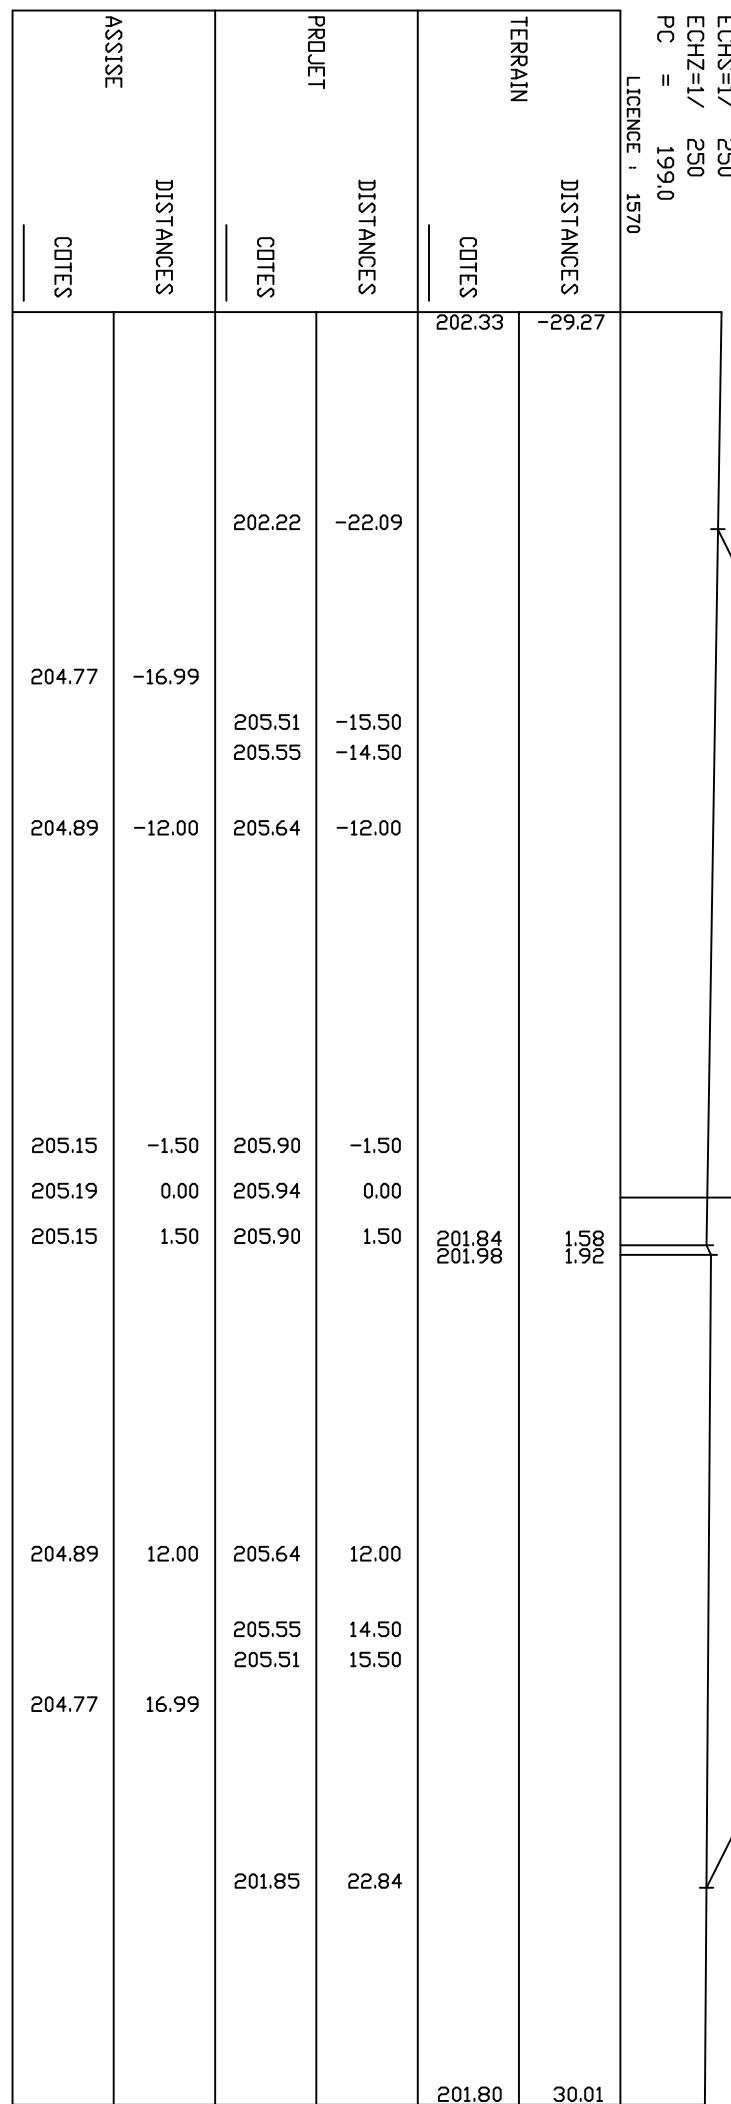

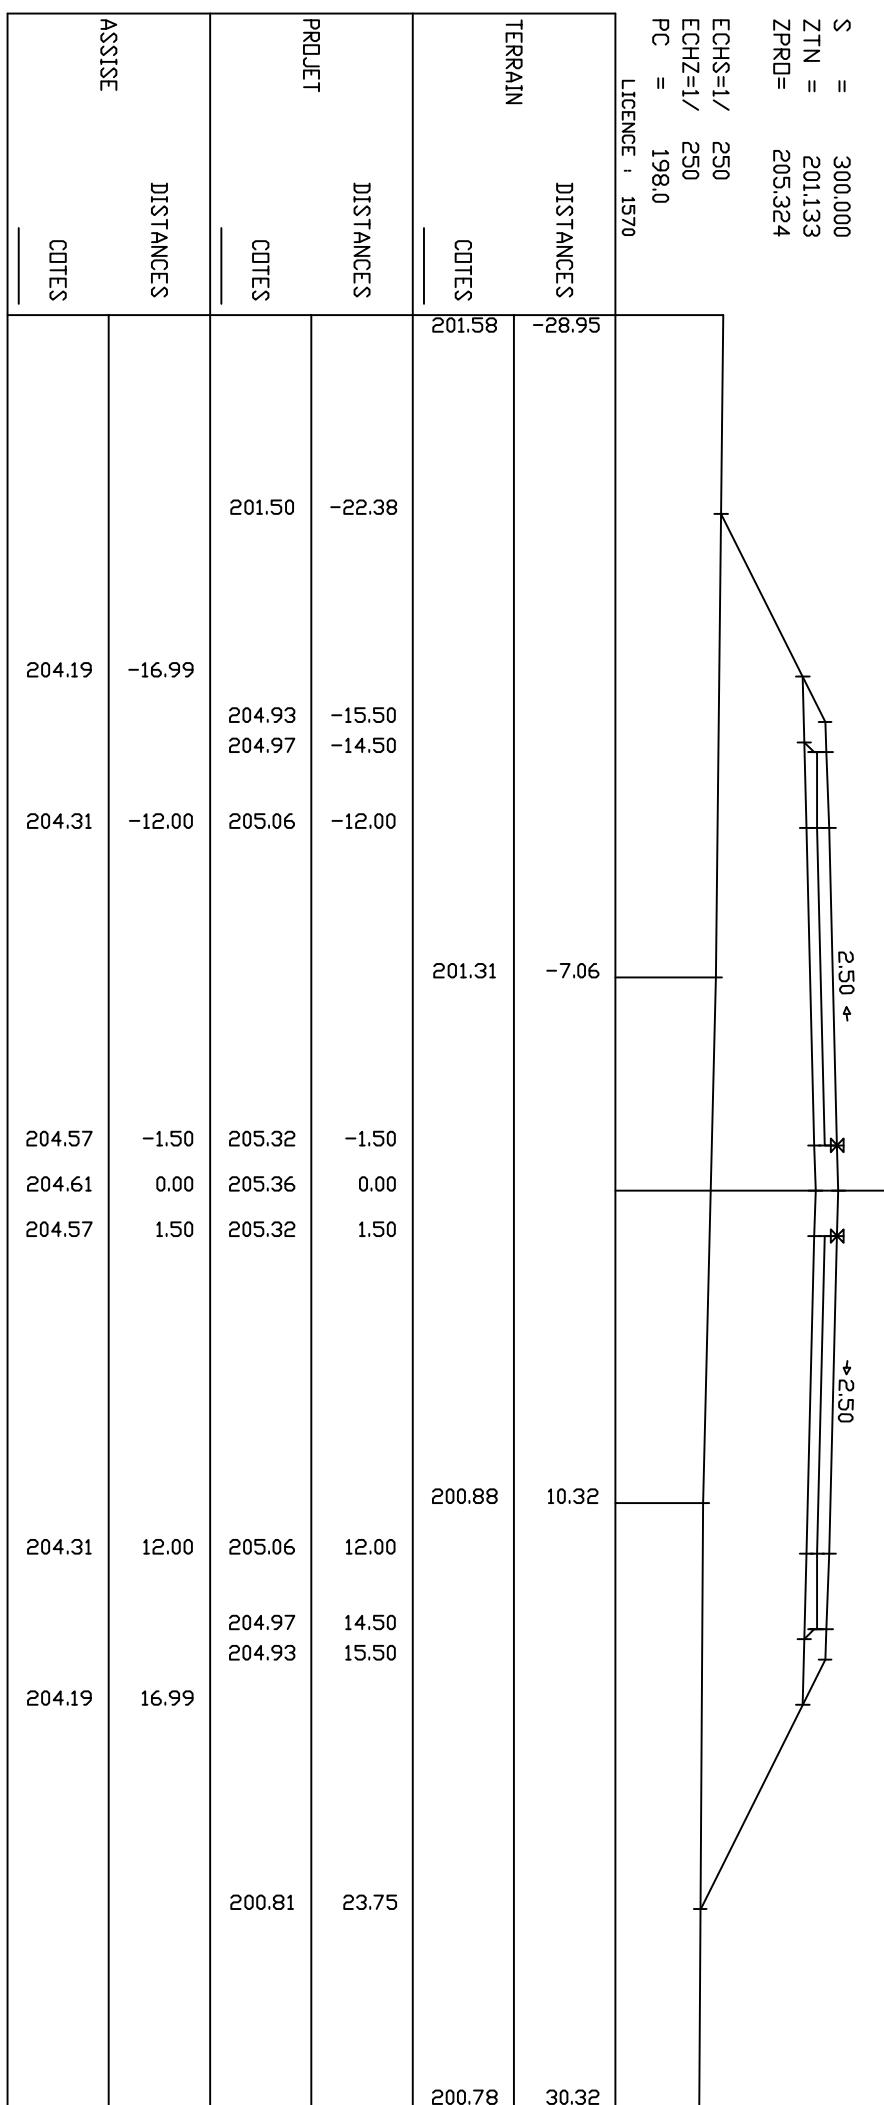

PROFIL 14

G2PIS

S = 325.000
 ZTN = 200.394
 ZPRO= 204.744

ECHS=1/
 ECHZ=1/
 PC = 197,0
 LICENCE , 1570

TERRAIN

DISTANCES

COTES

200.95 -28.67

DISTANCES

COTES

200.80 -16.52

DISTANCES

COTES

200.87 -22.46

DISTANCES

COTES

204.35 -15.50

DISTANCES

COTES

204.39 -14.50

DISTANCES

COTES

204.48 -12.00

DISTANCES

COTES

204.74 -1.50

DISTANCES

COTES

204.78 0.00

DISTANCES

COTES

204.74 1.50

DISTANCES

COTES

204.39 12.00

DISTANCES

COTES

204.35 14.50

DISTANCES

COTES

199.90 24.41

DISTANCES

COTES

199.87 30.61

DISTANCES


COTES

199.93 19.06

DISTANCES

COTES

199.87 30.61

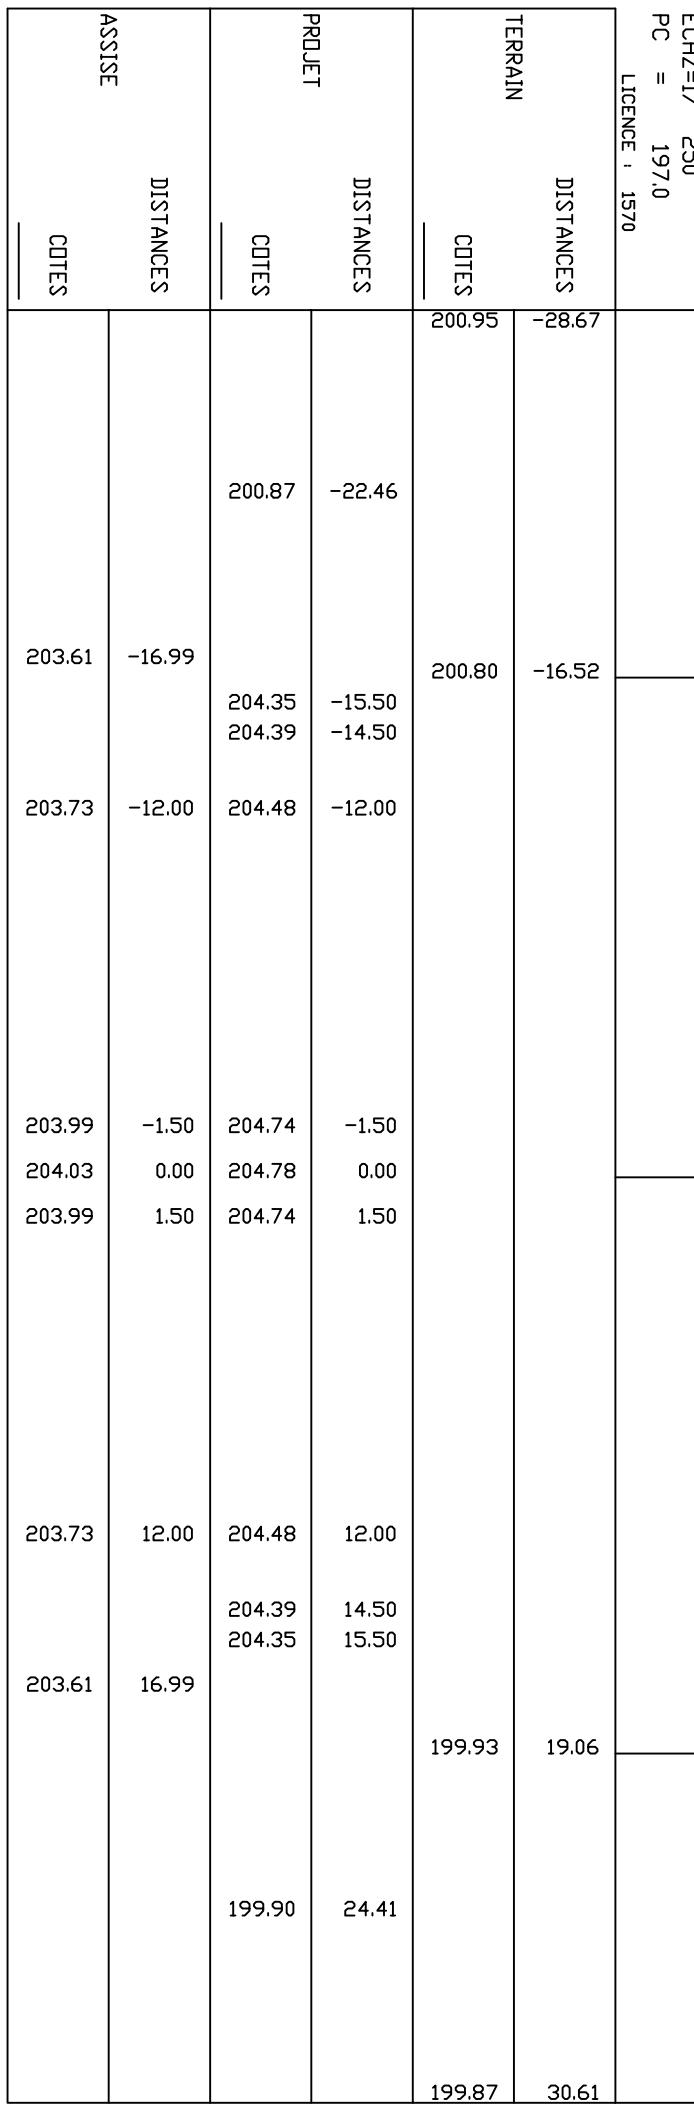



PROFIL 15

G2PIS

S = 350.000
 ZTN = 199.656
 ZPRO= 204.164

ECHS=1/
 ECHZ=1/
 PC = 196.0
 LICENCE , 1570

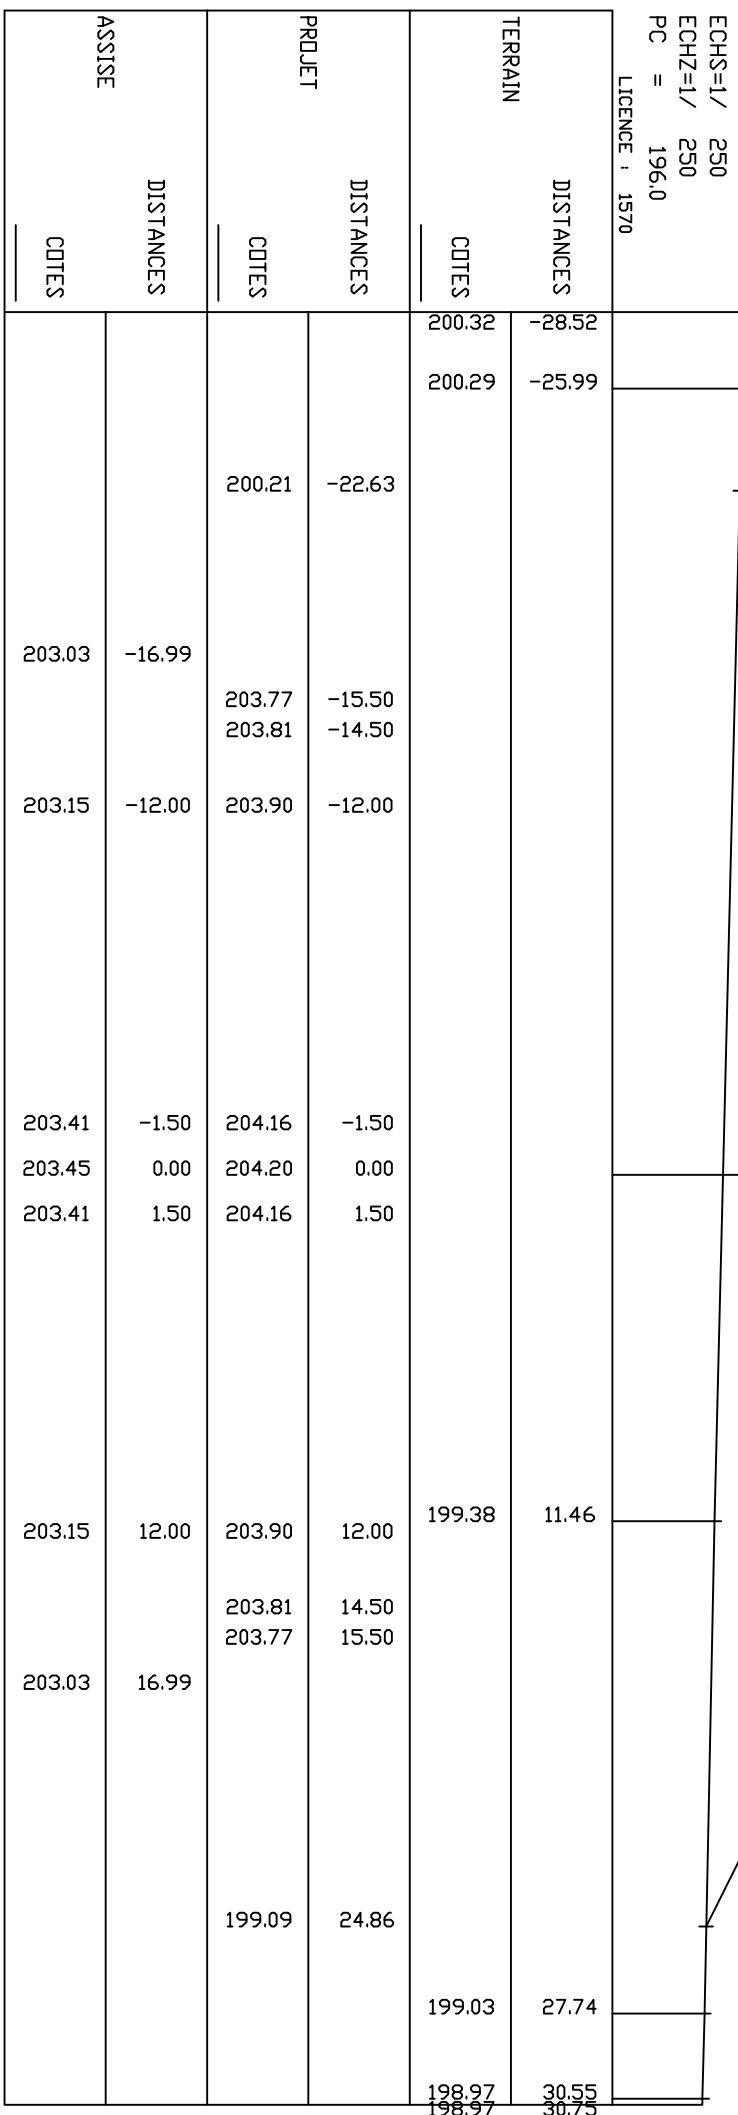

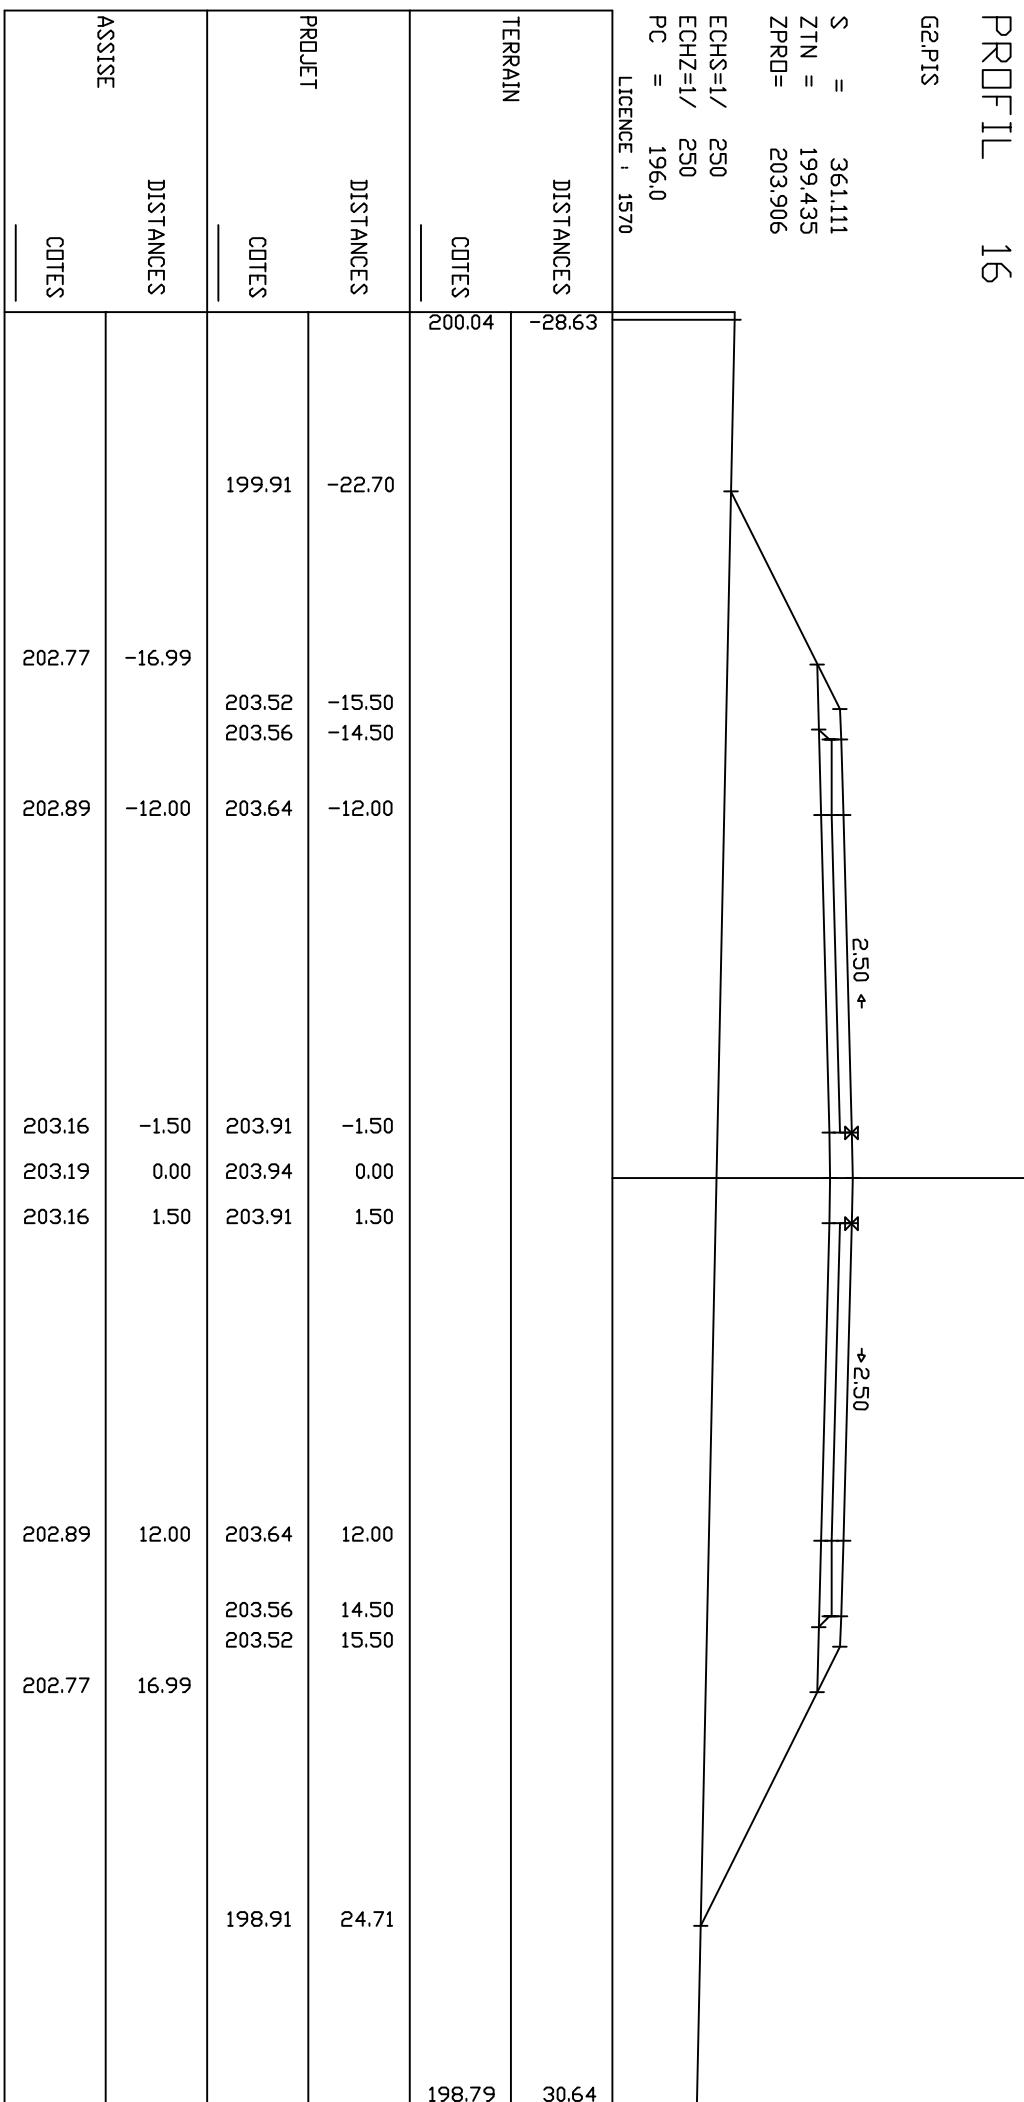

PROFIL 17

G2PIS

S = 375.000
 ZTN = 199.203
 ZPRO= 203.584

ECHS=1/
 ECHZ=1/
 PC = 196.0
 LICENCE , 1570

TERRAIN

DISTANCES

COTES

200.06 -28.46

DISTANCES

COTES

199.22 -0.80

DISTANCES

COTES

198.56 30.82

DISTANCES

COTES

198.69 24.51

DISTANCES

COTES

202.45 -16.99

DISTANCES

COTES

202.57 -12.00

DISTANCES

COTES

202.83 -1.50

DISTANCES

COTES

202.87 0.00

DISTANCES

COTES

202.83 1.50

DISTANCES

COTES

202.57 12.00

DISTANCES

COTES

202.45 16.99

ASSISE		PROJECT	TERRAIN	DISTANCES	COTES
DISTANCES	COTES	DISTANCES	DISTANCES	COTES	
202.45	-16.99	199.87	-22.15	200.06	-28.46
202.57	-12.00	203.19 203.23	-15.50 -14.50	199.22	-0.80
202.83	-1.50	203.58	-1.50	198.56	30.82
202.87	0.00	203.62	0.00		
202.83	1.50	203.58	1.50		
202.57	12.00	203.32	12.00		
202.45	16.99	203.23 203.19	14.50 15.50		
		198.69	24.51		

ASSISE COTES	DISTANCES COTES	TERRAIN		DISTANCES COTES	DISTANCES COTES	G2PIS
		PROJECT	COTES			
201.87	-16.99	199.86	-21.02		200.08	-28.28
		202.61	-15.50			
		202.65	-14.50			
201.99	-12.00	202.74	-12.00			
202.25	-1.50	203.00	-1.50			
202.29	0.00	203.04	0.00			
202.25	1.50	203.00	1.50			
201.99	12.00	202.74	12.00			
		202.65	14.50			
		202.61	15.50			
201.87	16.99	198.50	23.73			
				198.28	31.00	


PROFIL 18

S = 400.000
 ZTN = 199.217
 ZPRO= 203.004
 ECHS=1/
 ECHZ=1/
 PC = 195.0
 LICENCE , 1570



2.50 ↗

↗ 2.50

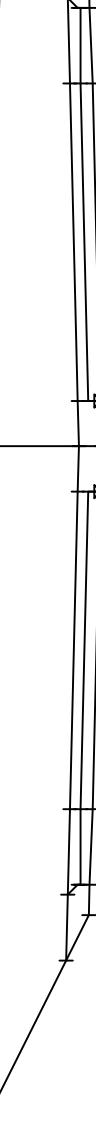

PROFIL 19

G2PIS

S = 425.000
 ZTN = 199.220
 ZPRO= 202.424


ECHS=1/
 ECHZ=1/
 PC = 195.0
 LICENCE , 1570

		TERRAIN		DISTANCES		
		DISTANCES		COTES		
		PROJECT		COTES		
ASSISE	DISTANCES	COTES	COTES	COTES	COTES	
201.29	-16.99	199.83	-19.92	200.08	-28.26	
		202.03	-15.50			2.50 ↗
		202.07	-14.50			↗ 2.50
201.41	-12.00	202.16	-12.00			
201.67	-1.50	202.42	-1.50			
201.71	0.00	202.46	0.00			
201.67	1.50	202.42	1.50			
201.41	12.00	202.16	12.00	198.86	12.02	
		202.07	14.50			
		202.03	15.50			
201.29	16.99	198.44	22.68			
				198.12	31.02	

PROFIL 20

G2,PIS

S = 450,000
ZTN = 199,046
ZPRO = 201,843

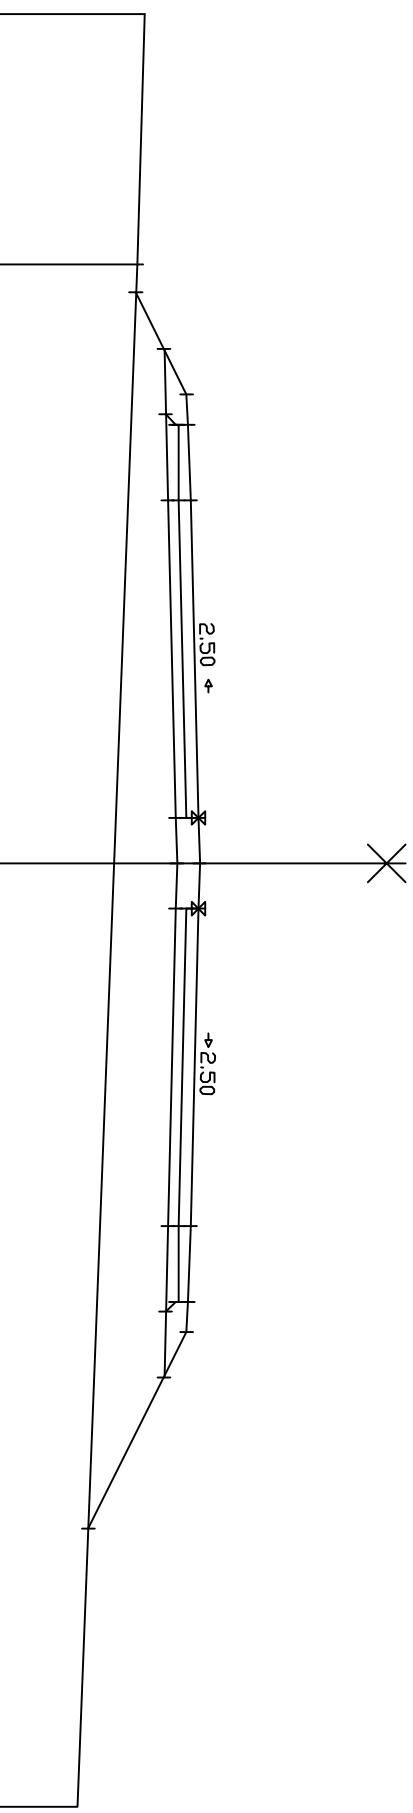

TERRAIN				DISTANCES	
				COTES	
				200.06	-28.07
PROJET	DISTANCES				
	COTES				
				199.81	-19.80
ASSISE	DISTANCES				
	COTES				
				197.85	31.21

PROFIL 21

G2PIS

S = 475.000
 ZTN = 198.748
 ZPRO= 201.263

ECHS=1/
 ECHZ=1/
 PC = 195.0
 LICENCE , 1570

TERRAIN

DISTANCES

COTES

199.82 -28.23

TERRAIN

DISTANCES

COTES

198.54 5.55

TERRAIN

DISTANCES


COTES

197.73 31.04

ASSISE	DISTANCES	COTES	PROJECT		DISTANCES	COTES	DISTANCES	COTES
			DISTANCES	COTES				
200.13	-16.99	199.45	-18.35					
		200.87	-15.50					
		200.91	-14.50					
200.25	-12.00	201.00	-12.00					
200.51	-1.50	201.26	-1.50					
200.55	0.00	201.30	0.00					
200.51	1.50	201.26	1.50					
200.25	12.00	201.00	12.00					
		200.91	14.50					
		200.87	15.50					
200.13	16.99	198.04	21.17					


PROFIL 22
G2.PIS

S = 500,000
 ZTN = 199,003
 ZPRD= 200.683
 ECHS=1/
 250

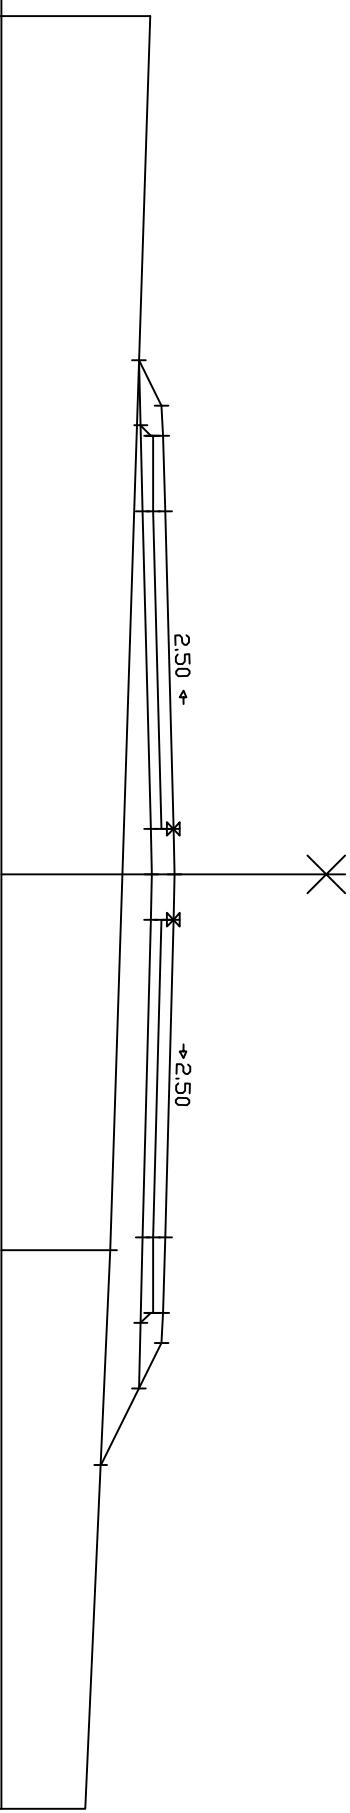

ASSISE COTES	DISTANCES COTES	TERRAIN DISTANCES COTES		DISTANCES COTES	G2PIS	PROFIL 23
		PROJECT COTES	199.71 199.75			
199.02	-14.83	199.71 199.75	-15.51 -15.50 -14.50	200.18	-28.09	
199.09	-12.00	199.84	-12.00	199.95	-20.78	
199.35	-1.50	200.10	-1.50			
199.39	0.00	200.14	0.00			
199.35	1.50	200.10	1.50			
199.09	12.00	199.84	12.00			
		199.75 199.71	14.50 15.50			
198.97	16.99	198.15	18.62			
				197.58	31.19	

S = 525.000
 ZTN = 199.000
 ZPRO= 200.103
 ECHS=1/
 ECHZ=1/
 PC = 195.0
 LICENCE , 1570

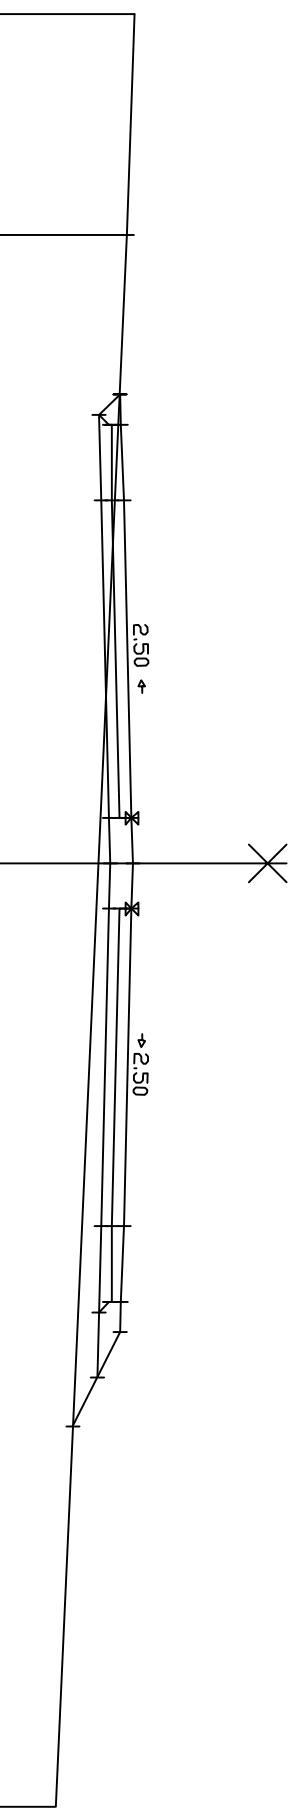


PROFIL 24


G2PIS

S = 550.000
 ZTN = 198.781
 ZPRO= 199.523

ECHS=1/
 ECHZ=1/
 PC = 195.0
 LICENCE , 1570

ASSISE	DISTANCES	COTES	TERRAIN		DISTANCES	COTES
			DISTANCES	COTES		
198.40	-16.27	199.47 199.13 198.63 198.63 199.13 199.17	-21.50	-17.50 -17.00 -16.50 -16.00 -15.50 -14.50	199.79	-31.63
198.51	-12.00	199.26	-12.00			
198.77	-1.50	199.52	-1.50			
198.81	0.00	199.56	0.00			
198.77	1.50	199.52	1.50			
198.51	12.00	199.26	12.00	198.44	10.78	
198.39	16.99	199.17 199.13 198.13	14.50 15.50 17.51			
				197.66	27.64	

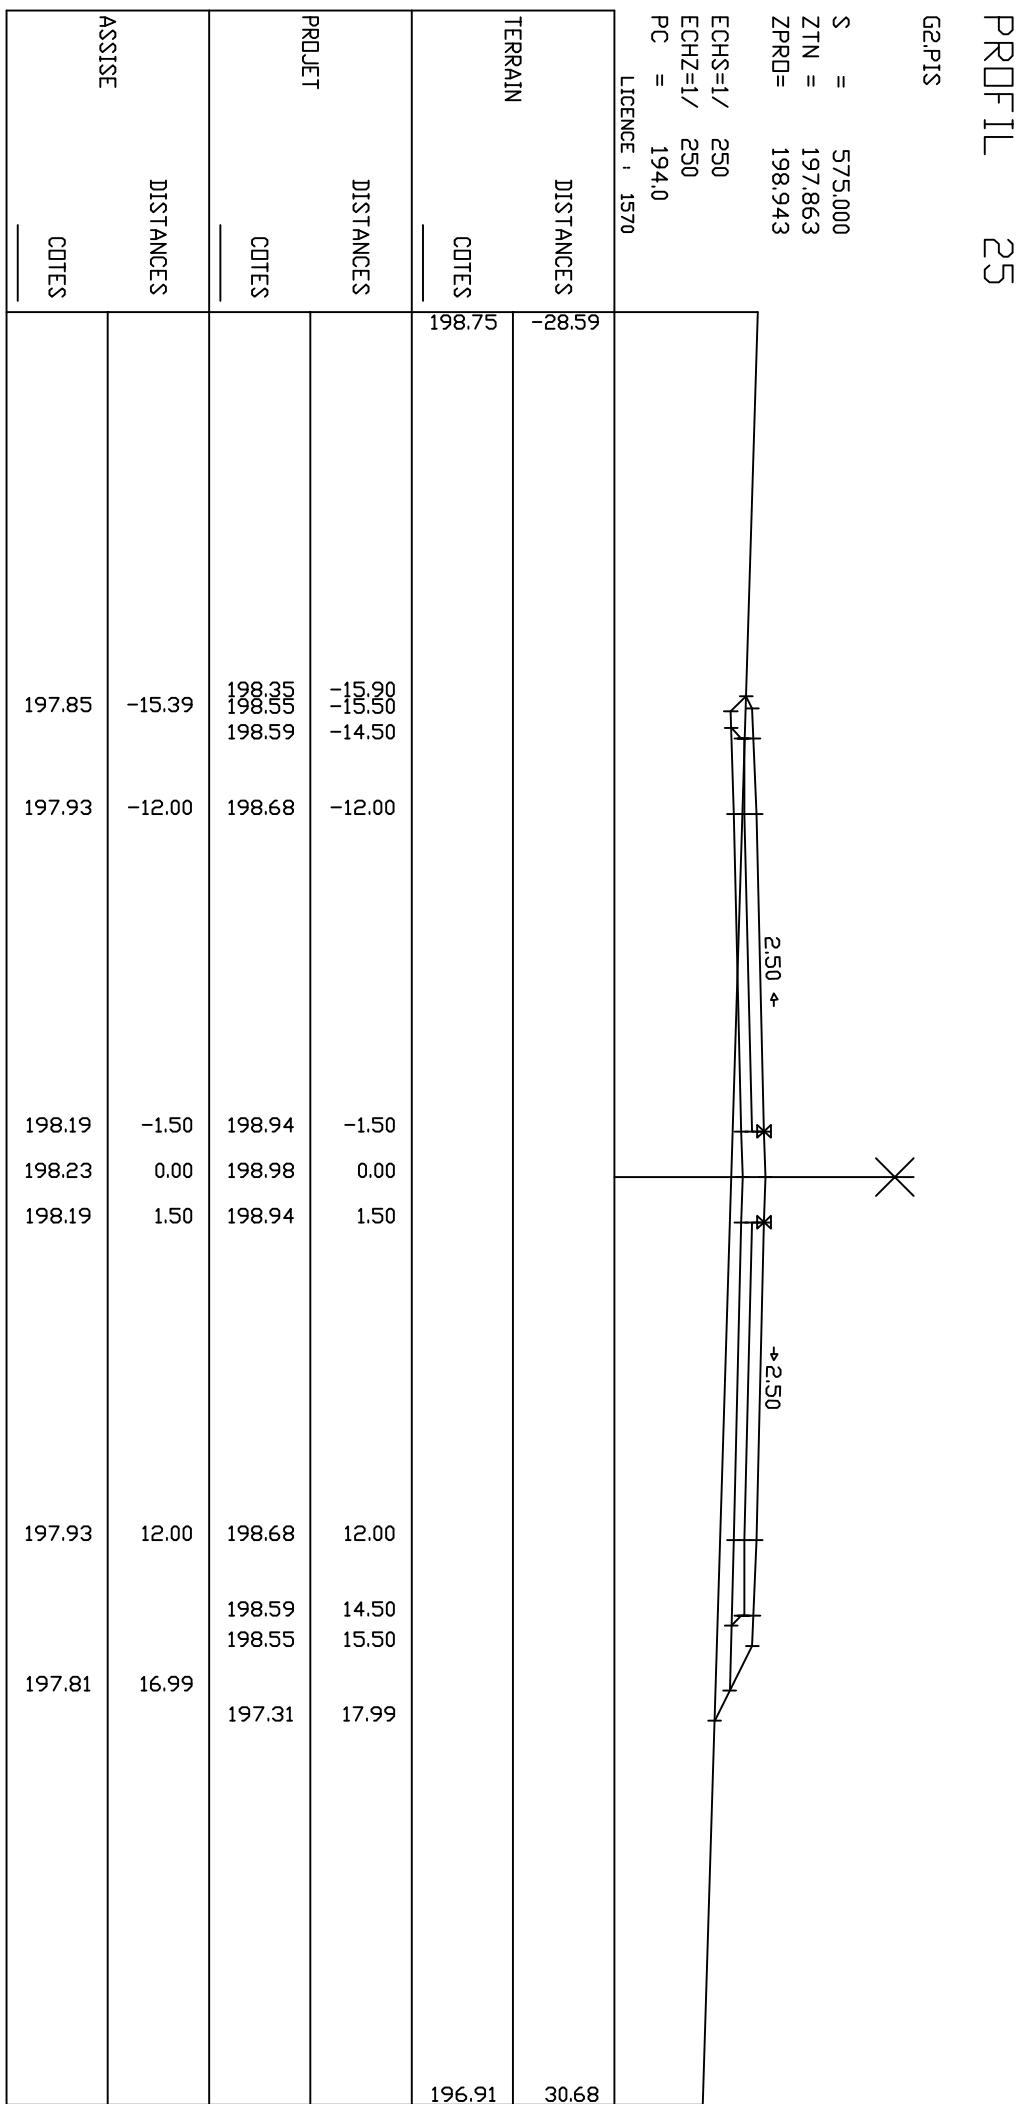

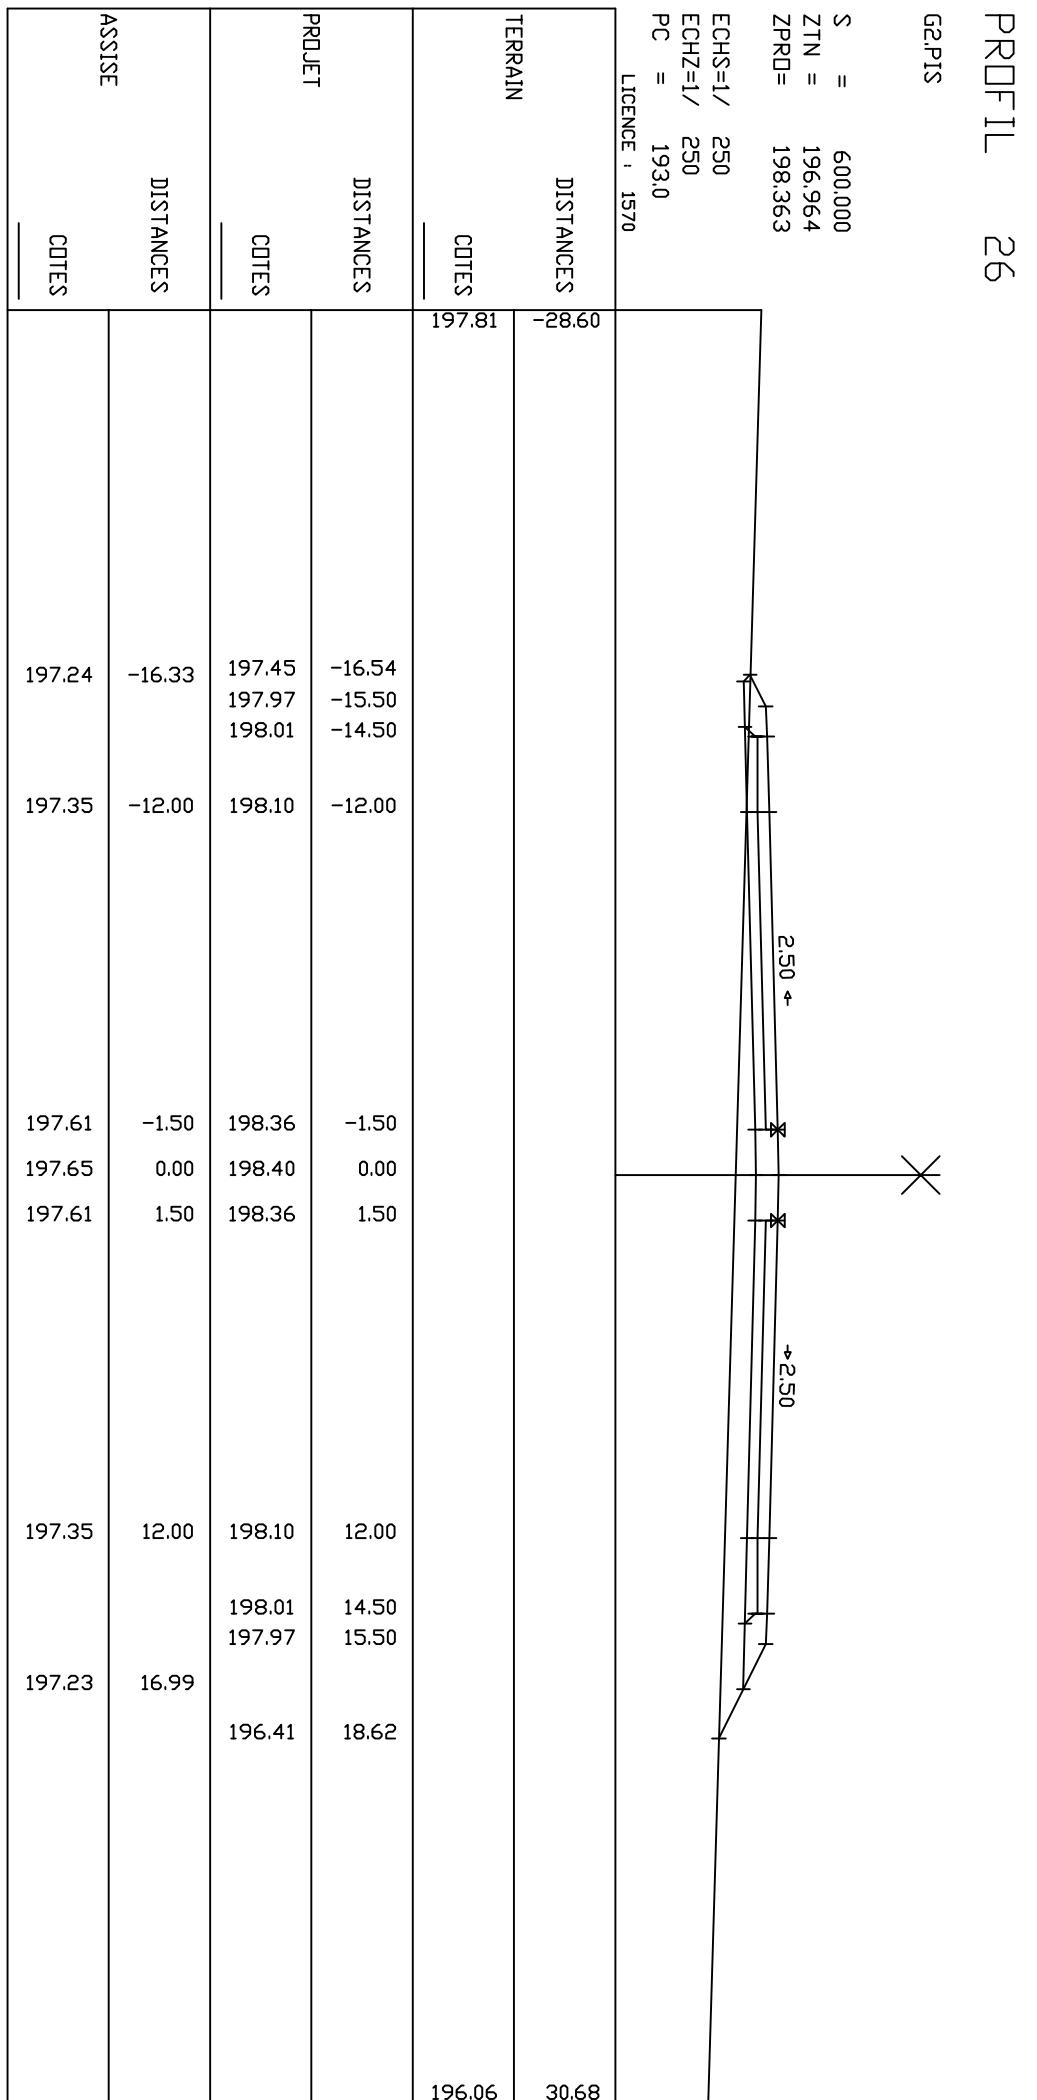


PROFIL 27

G2,PIS

S = 625,000
ZTN = 196,937
ZPRO = 197,782

PC = 193.0
LICENCE : 1570

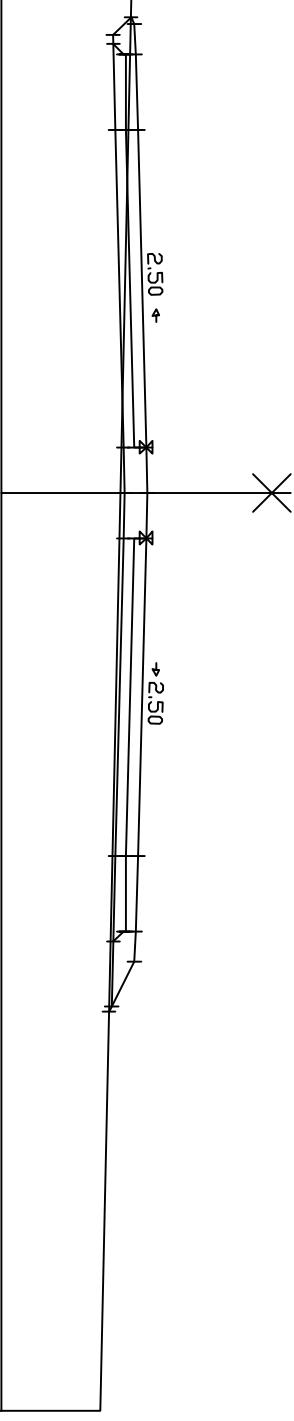

PROFIL 28

G2PIS

S = 650.000
 ZTN = 196.168
 ZPRO= 197.202

ECH\$=1/
 ECHZ=1/
 PC = 193.0
 LICENCE , 1570

		DISTANCES		DISTANCES		COTES		COTES		DISTANCES		TERRAIN	
ASSISE	DISTANCES												
	COTES												
196.10	-15.69	196.51 196.81 196.85		-16.10 -15.50 -14.50		196.78	-28.92						
196.19	-12.00	196.94		-12.00									
196.45	-1.50	197.20		-1.50									
196.49	0.00	197.24		0.00									
196.45	1.50	197.20		1.50									
196.19	12.00	196.94		12.00									
196.06	16.99	196.85 196.81 195.80		14.50 15.50 17.53		195.52	30.35						


PROFIL 29

G2,RIS

S = 675.000
 ZTN = 195.480
 ZPRD= 196.622

ECHS=1/
 ECHZ=1/
 PC = 192.0

LIGENCE : 1570

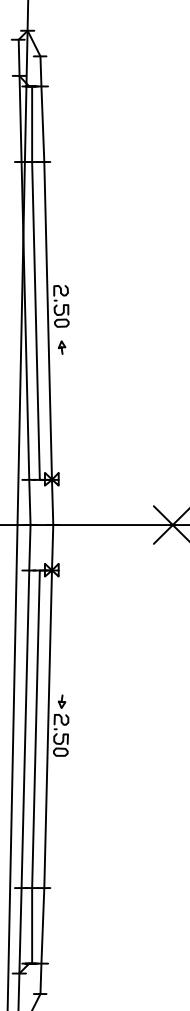

TERRAIN

DISTANCES

COTES

196.07 -28.94

PROJECT

DISTANCES

COTES

—


ASSISE	DISTANCES	COTES	—
--------	-----------	-------	---


ASSISE	DISTANCES	COTES	—
--------	-----------	-------	---


四

—
—
□

S = 700.000
ZTN = 194.711
ZPRD= 196.042

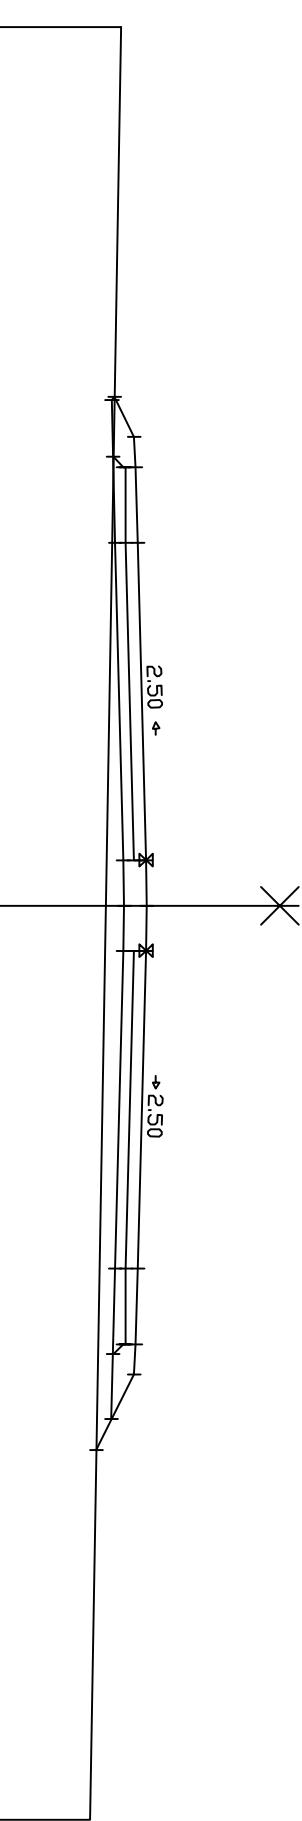

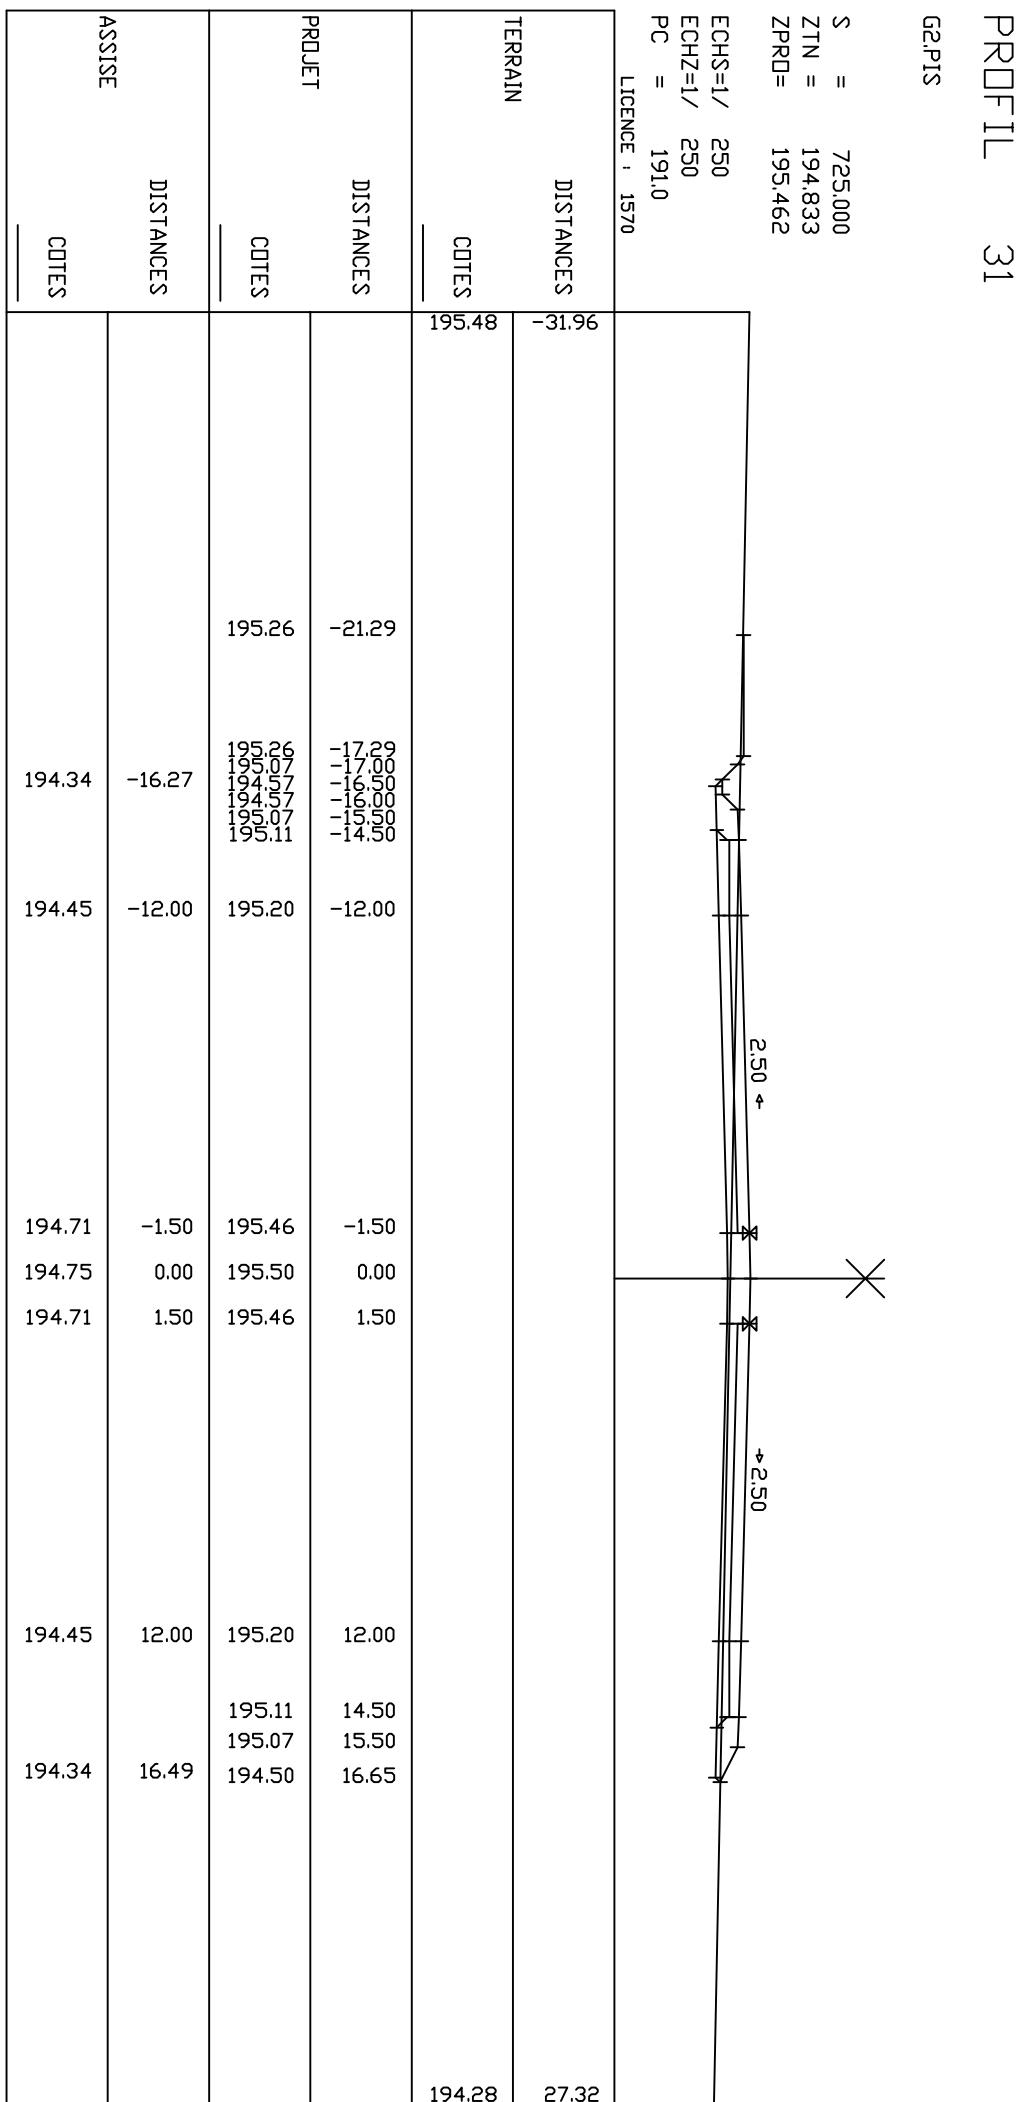


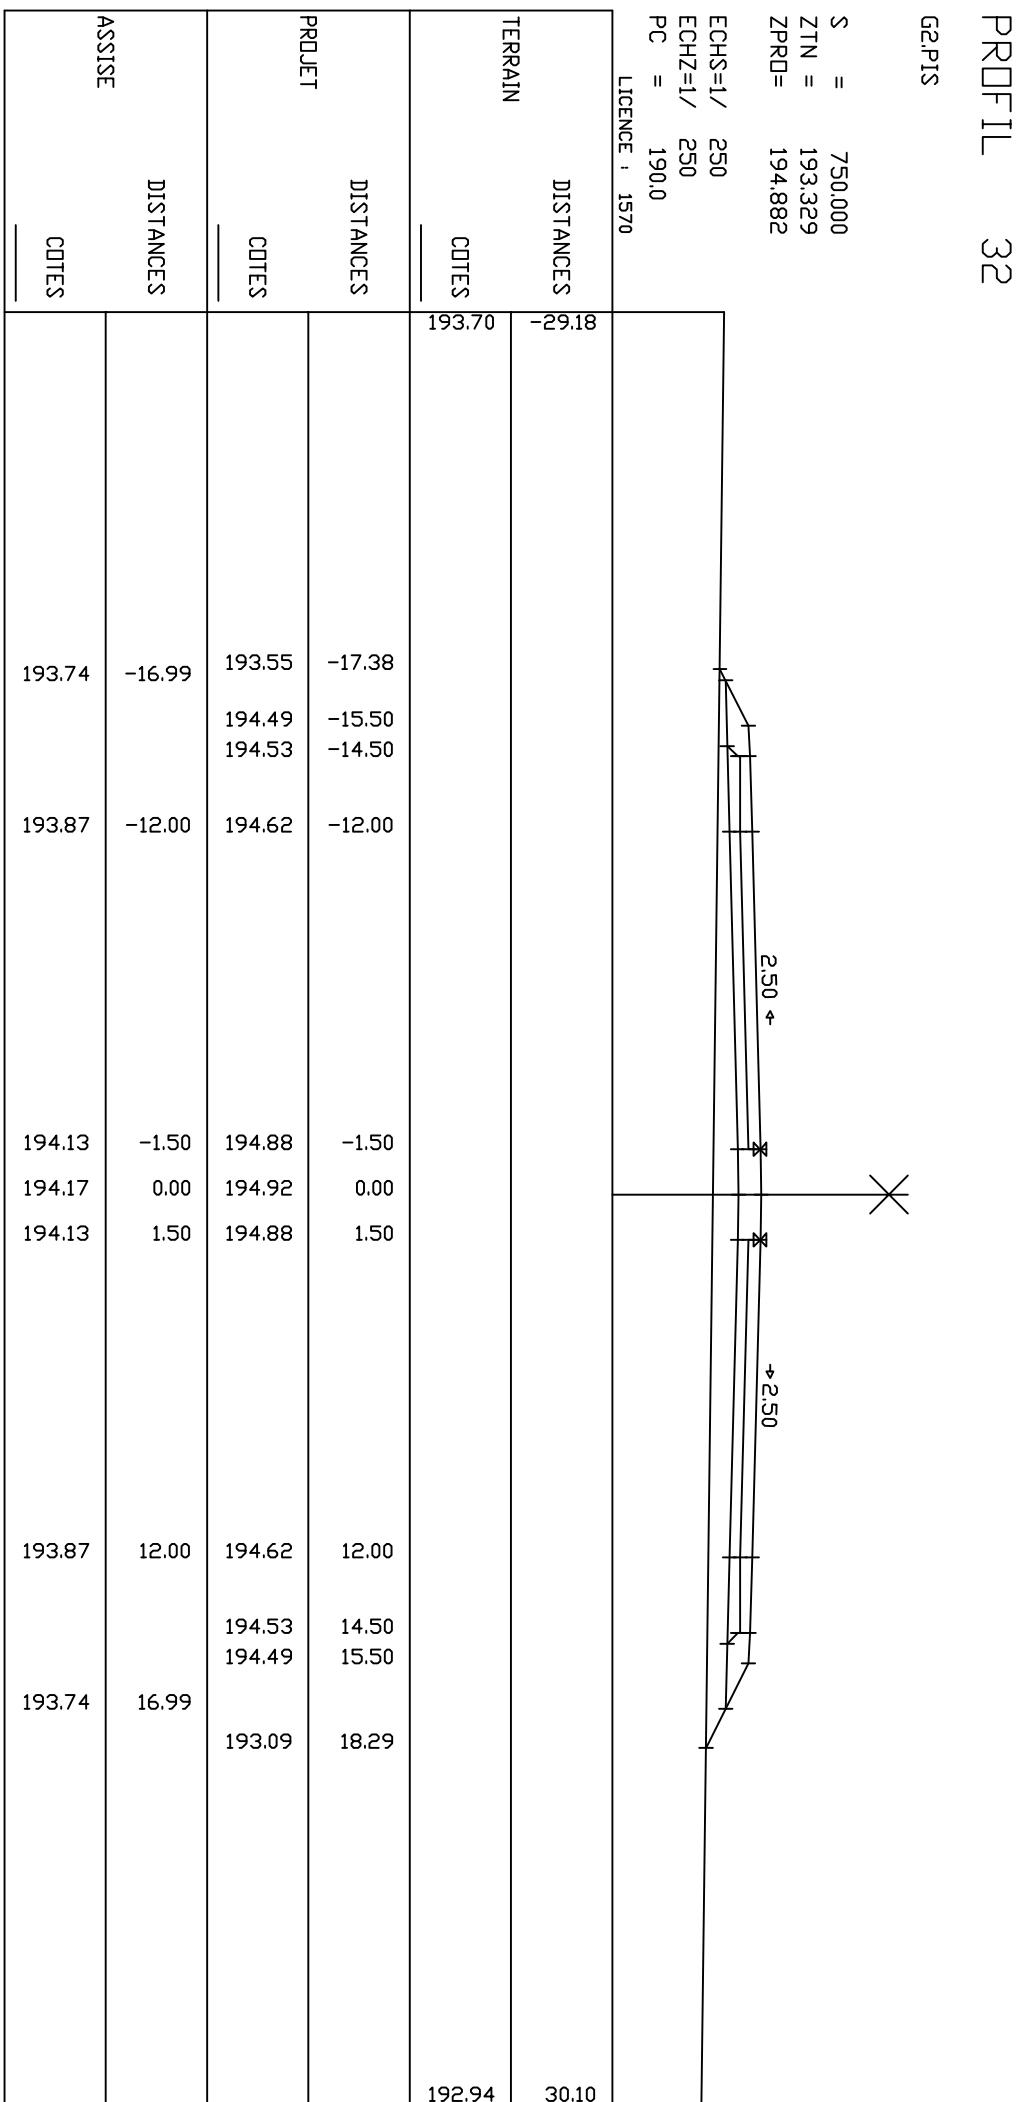

PROFIL 33

G.P.S.

S = //5,000
 ZTN = 192,327
 ZPRD= 194,302

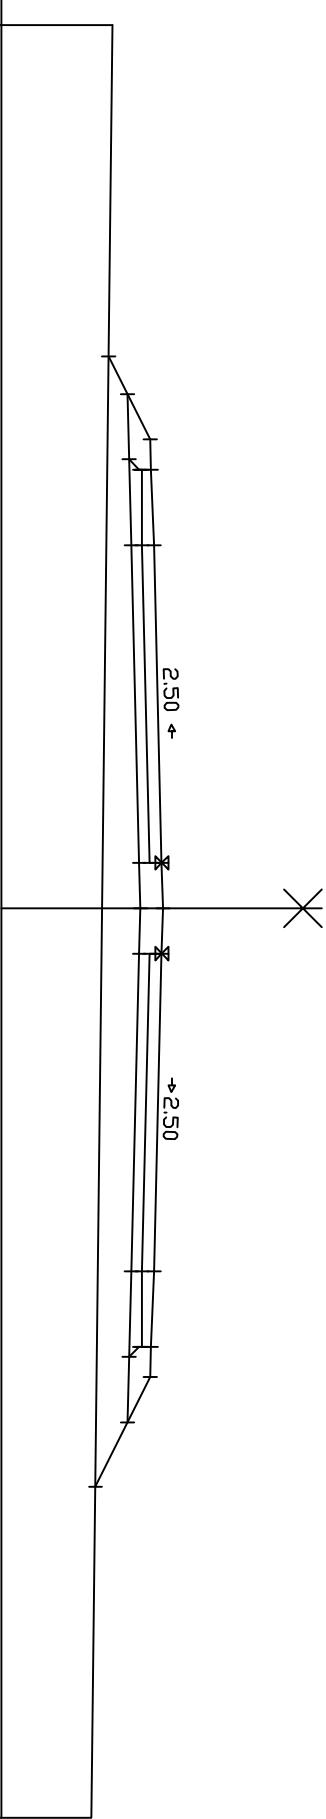


		TERRAIN		DISTANCES		COTES		DISTANCES		COTES		DISTANCES		COTES			
ASSISE		PROJECT		PROJECT		TERRAIN		PROJECT		TERRAIN		PROJECT		TERRAIN		PROJECT	
DISTANCES		DISTANCES		COTES		COTES		DISTANCES		COTES		DISTANCES		COTES		DISTANCES	
192.62	-15.70	193.03 193.33 193.37	-16.11 -15.50 -14.50	193.02	-29.65												
192.71	-12.00	193.46	-12.00														
192.97	-1.50	193.72	-1.50														
193.01	0.00	193.76	0.00														
192.97	1.50	193.72	1.50														
192.71	12.00	193.46	12.00														
192.62	15.68	193.37 193.33 193.03	14.50 15.50 16.09	193.04	29.63												


PROFIL 34


G2PIS

S = 800.000
ZTN = 193.031
ZPRO= 193.721

ECHS=1/
ECHZ=1/
PC = 190.0
LICENCE , 1570

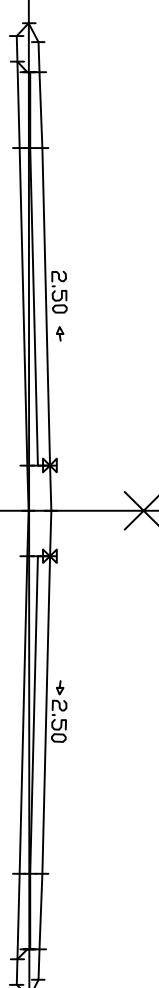

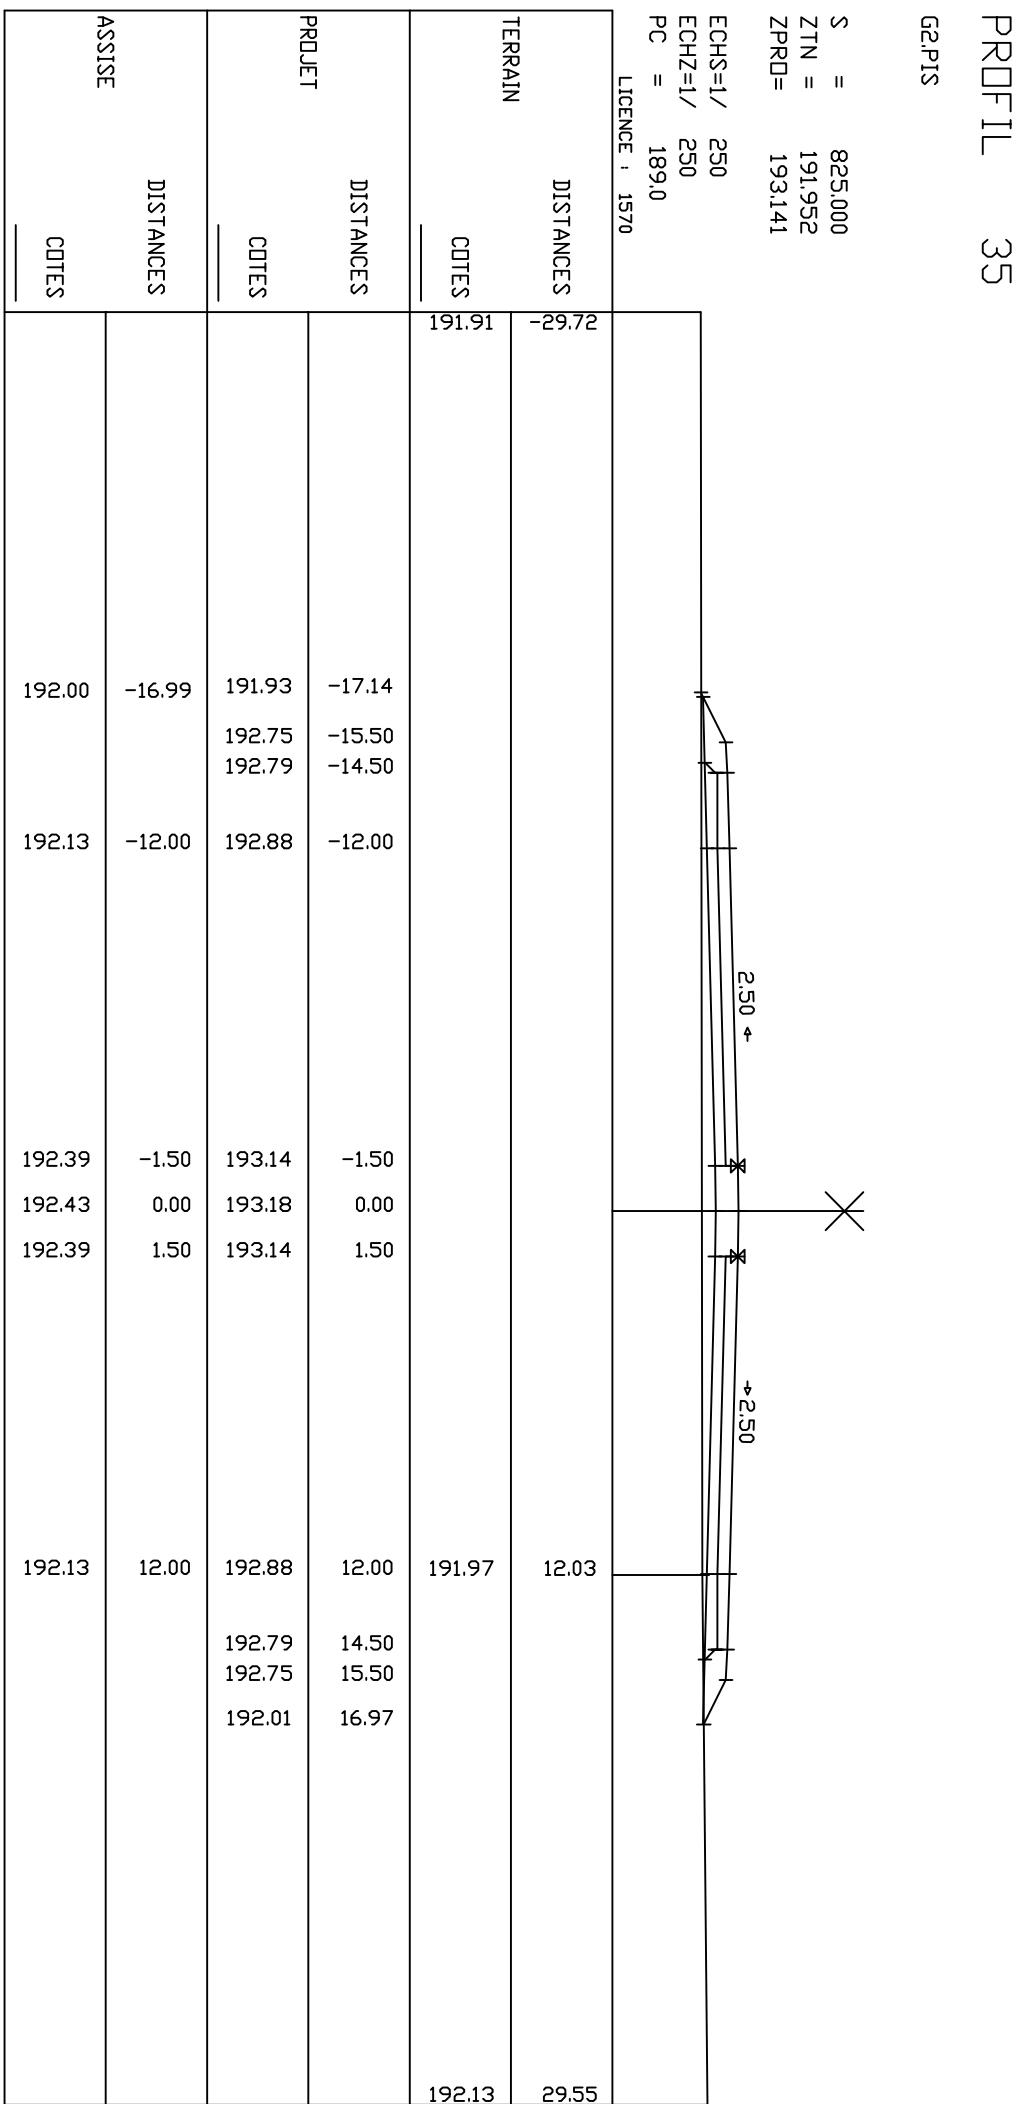

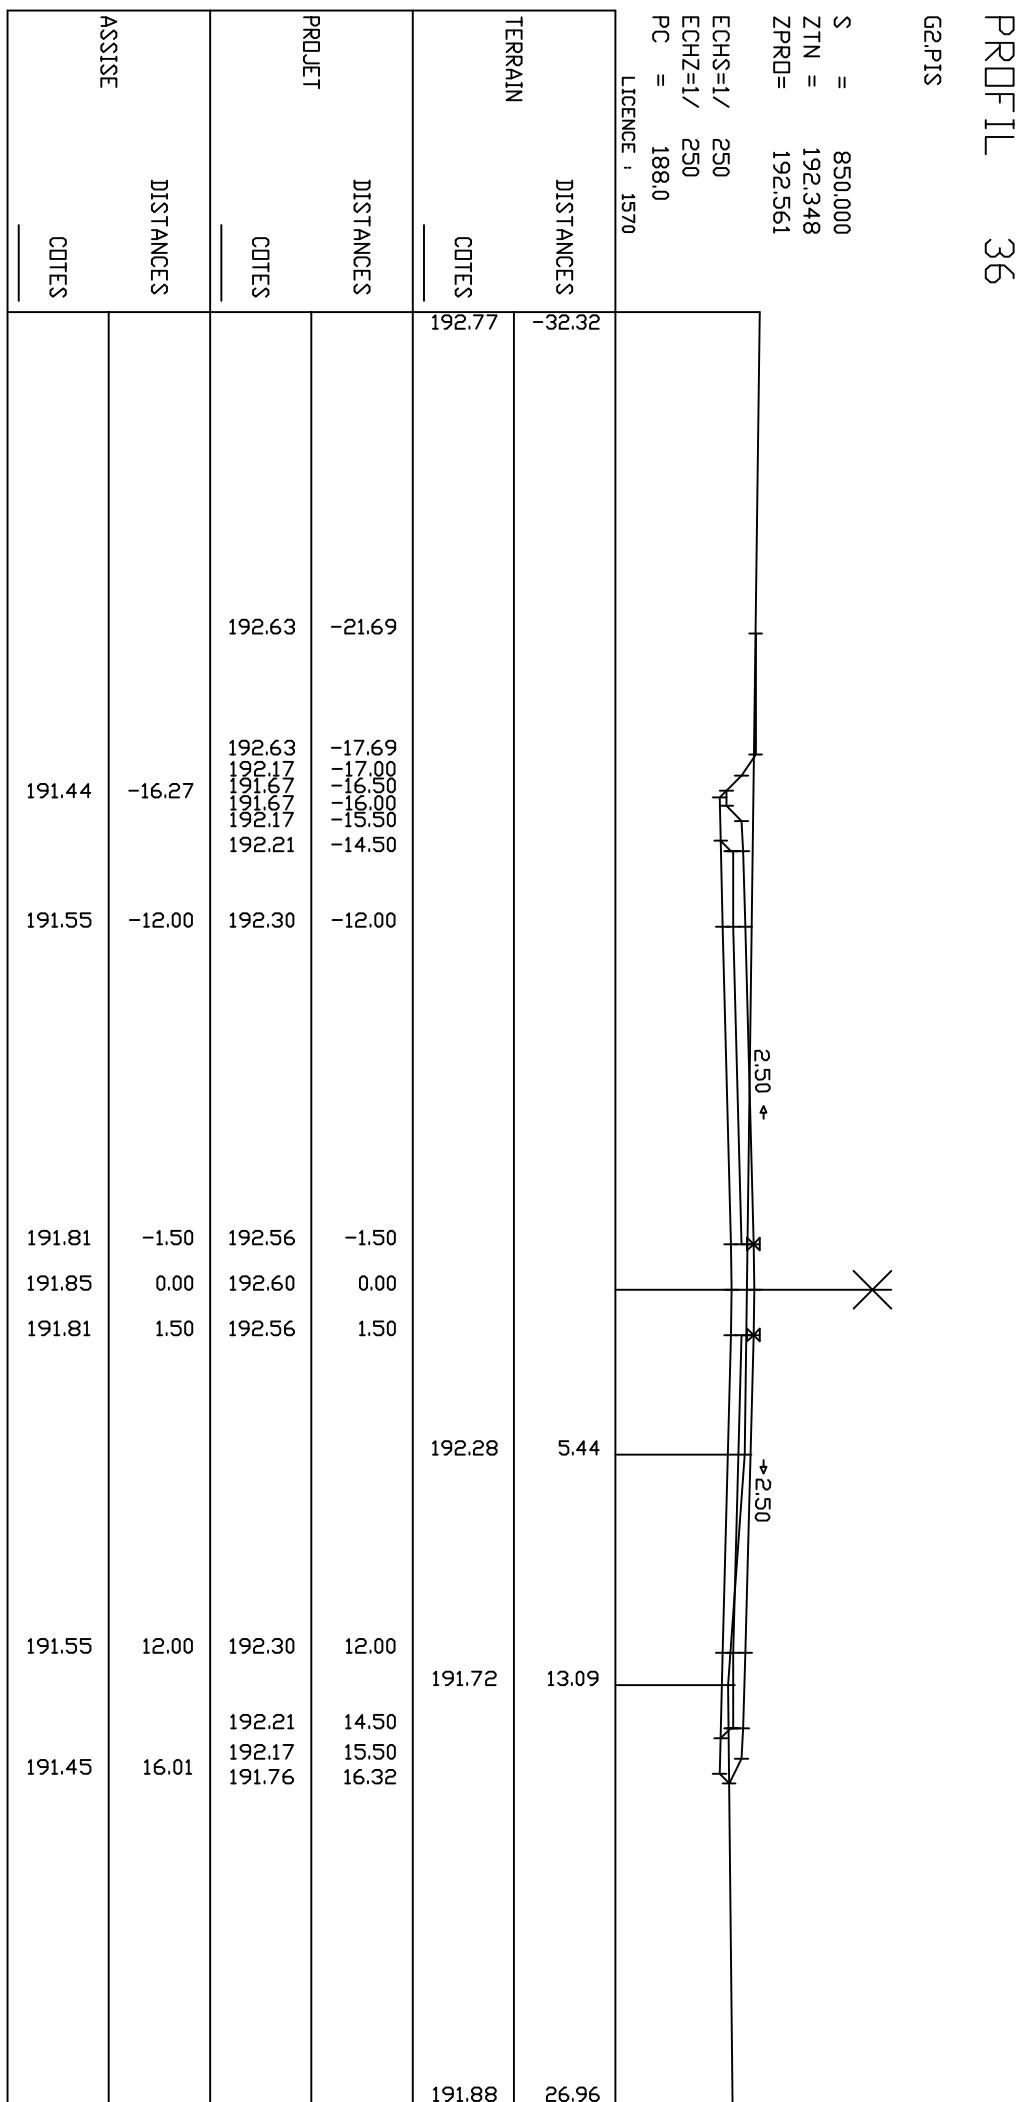


PROFIL 37

G2PIS

S = 875.000
 ZTN = 190.280
 ZR0= 191.981


ECHS=1/
 ECHZ=1/
 PC = 187.0
 LICENCE , 1570

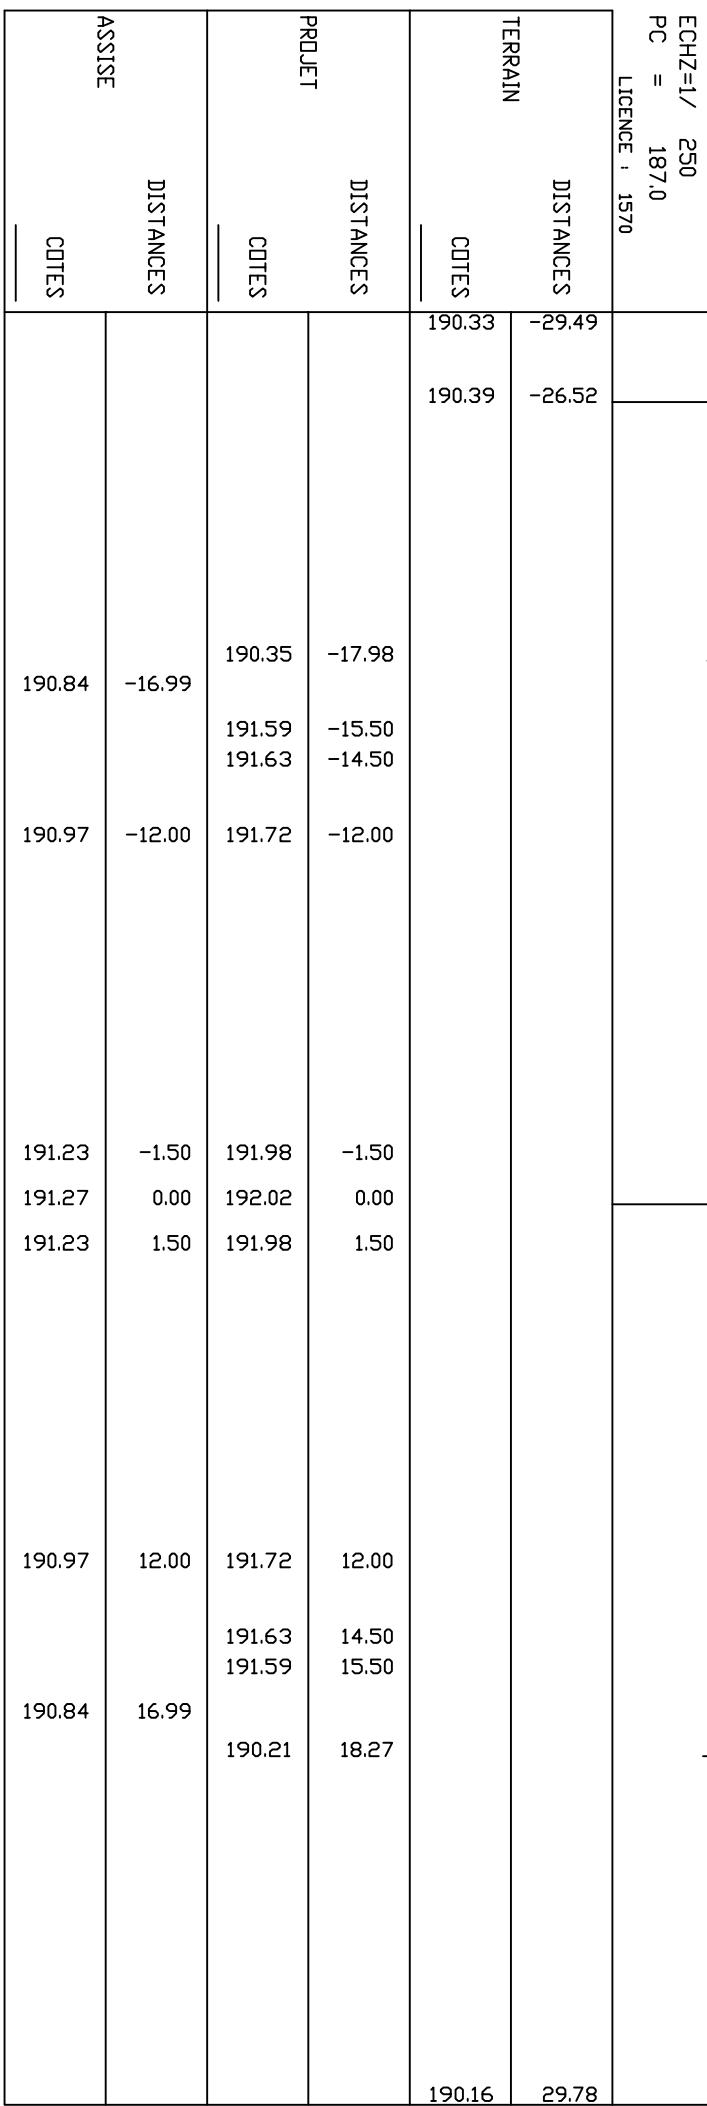


PROFIL 38

S = 900.00
ZTN = 189.021
ZPRO= 191.401

LICENCE : 1570
ECHZ=1/
PC = 186,0
EUCHZ=1/
PC = 250

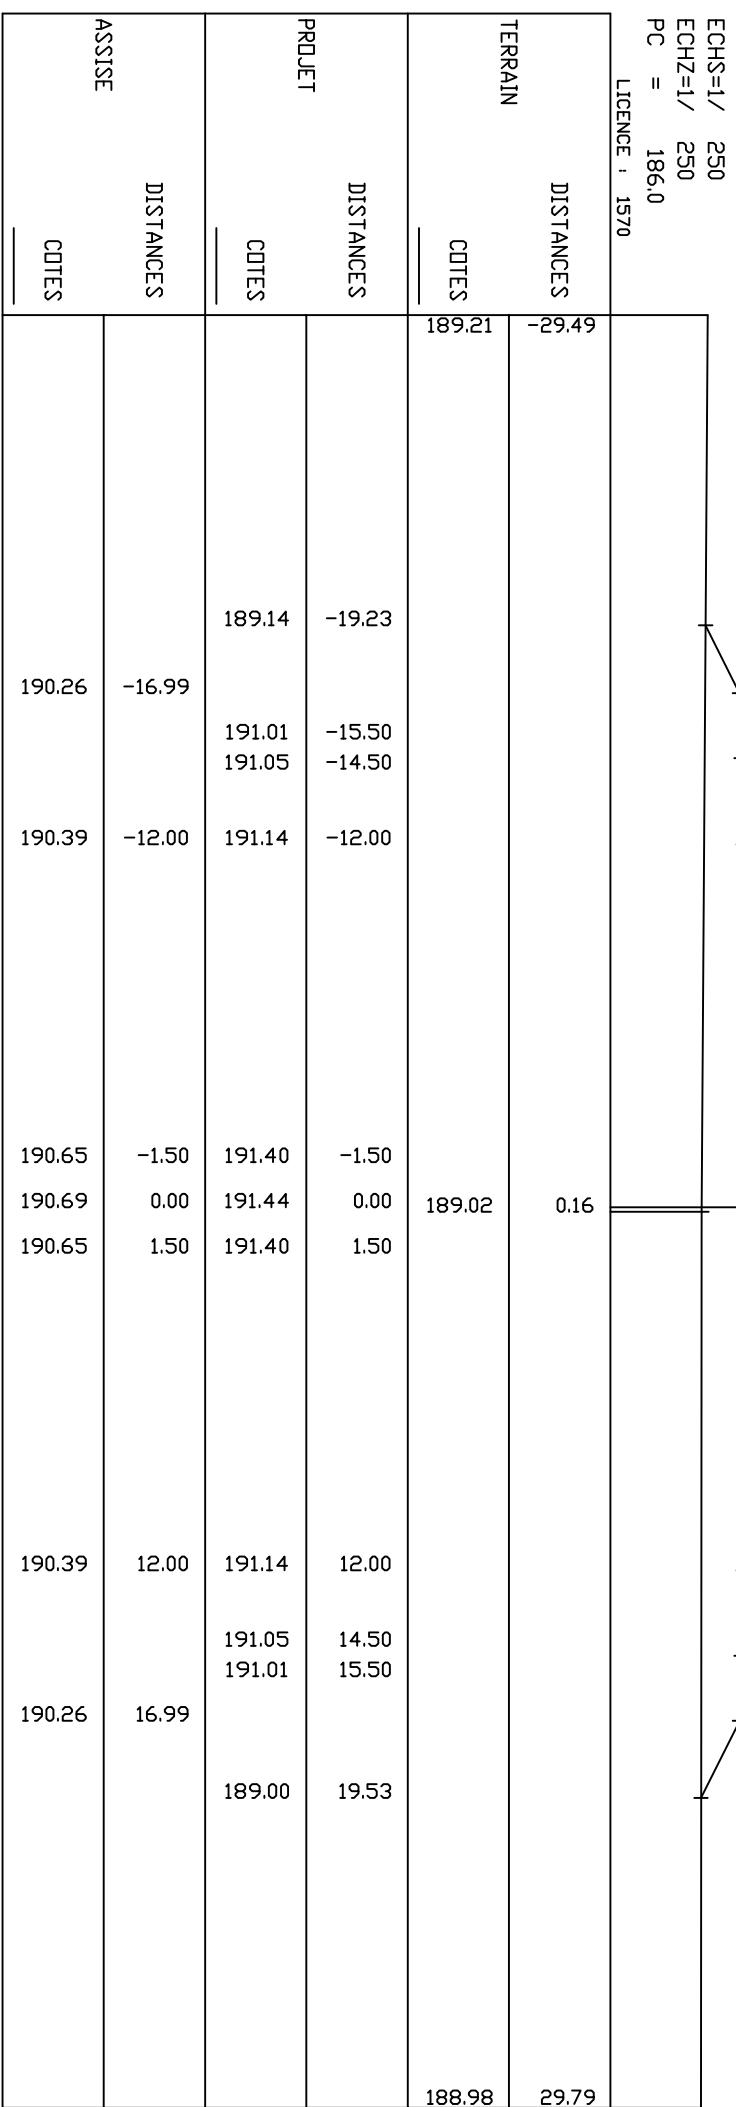

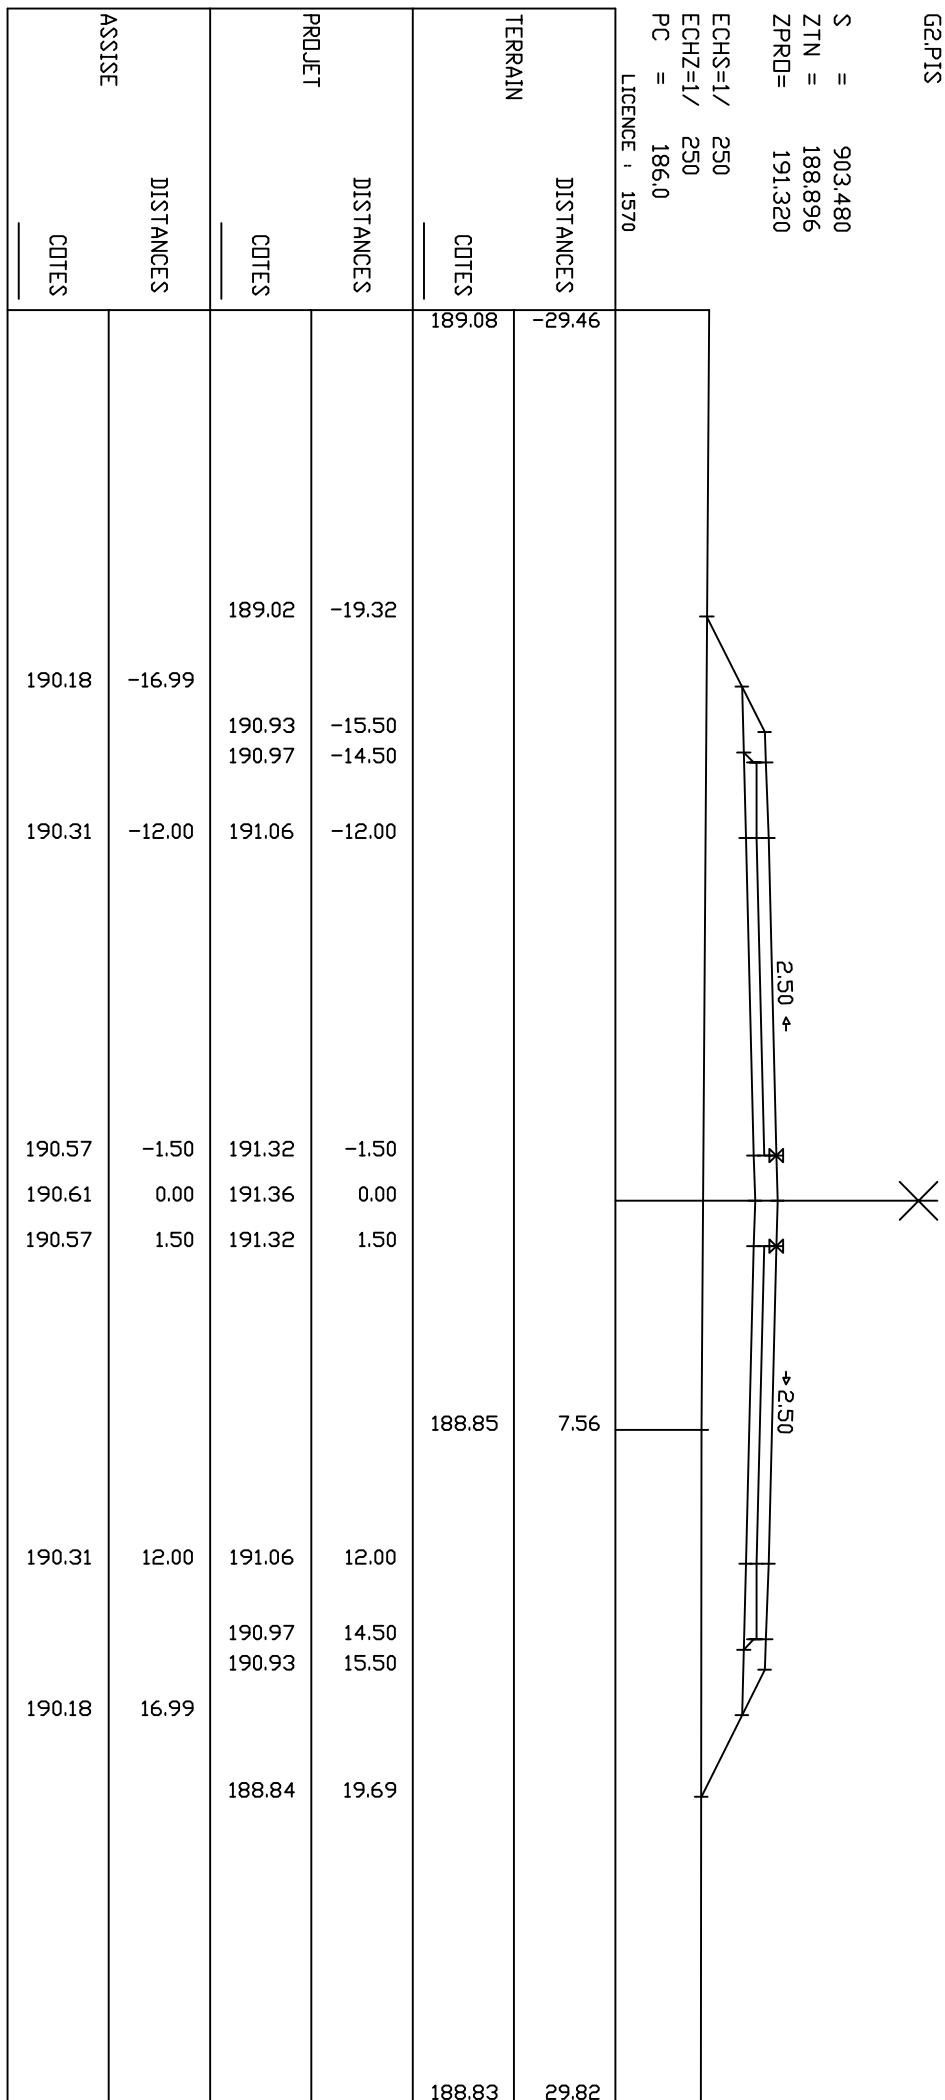


PROFIL 40

G2.PIS

S = 925.000
ZTN = 188.179
ZPRO = 190.821

ECHS=1/ 250
 ECHZ=1/ 250
 PC = 185.0

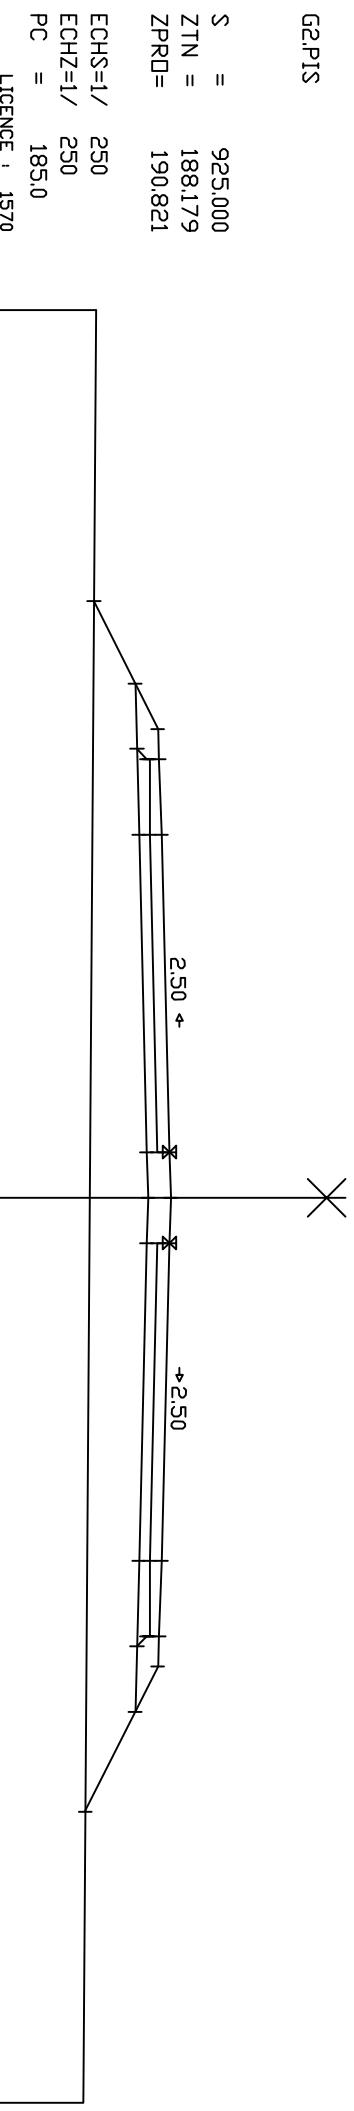

PROFIL 41

G2PIS

S = 950.000
 ZTN = 187.337
 ZPRO= 190.240


ECHS=1/
 ECHZ=1/
 PC = 184.0
 LICENCE , 1570

		TERRAIN		DISTANCES	COTES	
		DISTANCES		COTES		
		PROJECT	COTES			
ASSISE	DISTANCES					
189.10	-16.99	187.49	-20.23			
		189.85	-15.50			
		189.89	-14.50			
189.23	-12.00	189.98	-12.00			
189.49	-1.50	190.24	-1.50			
189.53	0.00	190.28	0.00			
189.49	1.50	190.24	1.50			
189.23	12.00	189.98	12.00			
		189.89	14.50			
		189.85	15.50			
189.10	16.99	187.18	20.83			
				187.12	29.94	

PROFIL 42

G2,PIS

S = 9/5.000
ZTN = 186,495
ZPRO = 189,660

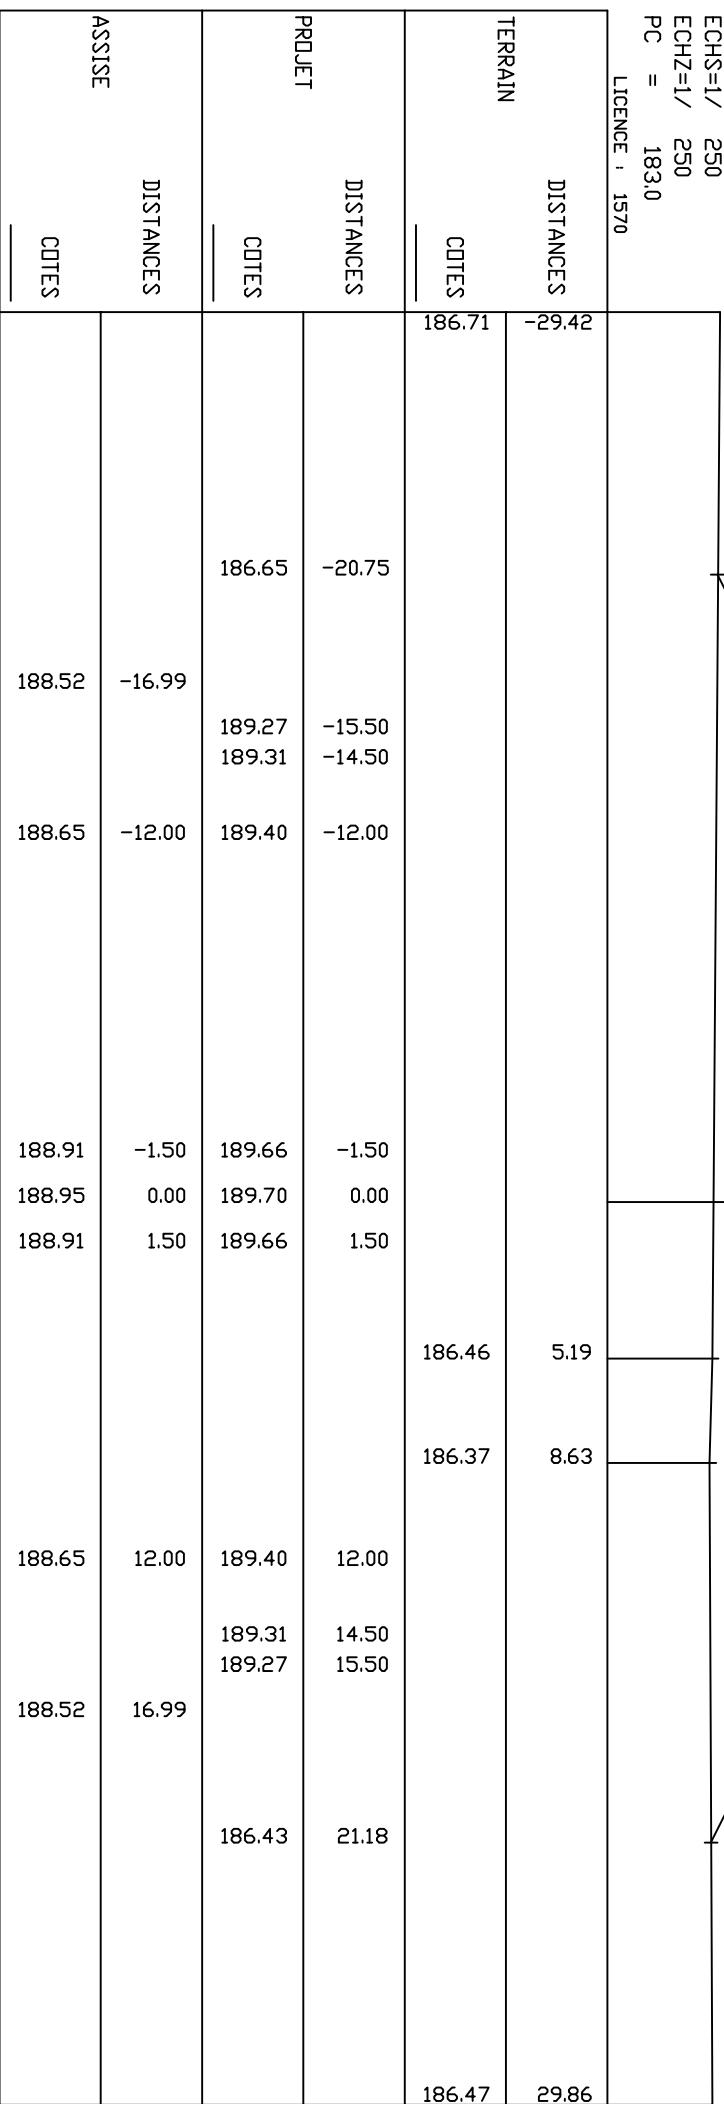

PROFIL 43

G2PIS

S = 1000.000
 ZTN = 185.774
 ZPRO= 189.080

ECHS=1/
 ECHZ=1/
 PC = 183.0
 LICENCE , 1570

TERRAIN

DISTANCES

COTES

185.87 -29.73

DISTANCES

COTES

185.82 -23.08

DISTANCES

COTES

185.69 -17.83

DISTANCES

COTES

185.78 -21.32

DISTANCES

COTES

188.69 -15.50

DISTANCES

COTES

188.73 -14.50

DISTANCES

COTES

188.82 -12.00

DISTANCES

COTES

189.08 -1.50

DISTANCES

COTES

189.12 0.00

DISTANCES

COTES

189.08 1.50

DISTANCES

COTES

188.82 12.00

DISTANCES

COTES

188.73 14.50

DISTANCES

COTES

188.69 15.50

DISTANCES


COTES

185.87 21.13

DISTANCES

COTES

185.91 29.54

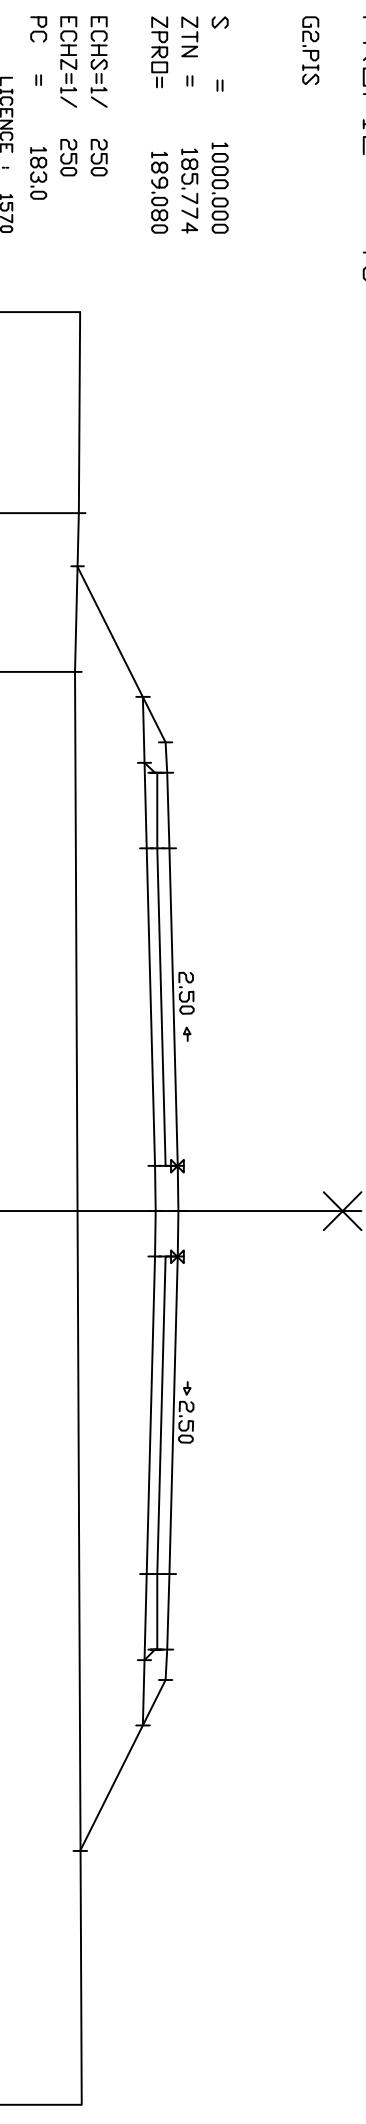

PROFIL 44

G2PIS

S = 1025.000
 ZTN = 185.096
 ZPRO= 188.500

ECHS=1/
 ECHZ=1/
 PC = 182.0
 LICENCE , 1570

ASSISE	DISTANCES	DISTANCES		TERRAIN	DISTANCES	COTES
		PROJET	COTES			
187.36	-16.99	188.11 188.15	-15.50 -14.50	185.01	-21.70	185.01
187.49	-12.00	188.24	-12.00			
187.75	-1.50	188.50	-1.50			
187.79	0.00	188.54	0.00			
187.75	1.50	188.50	1.50			
187.49	12.00	188.24	12.00			
187.36	16.99	188.15 188.11	14.50 15.50			
		185.21	21.30			
				185.25	29.44	

PROFIL 45

G2PIS

S = 1050.000
 ZTN = 184.390
 ZPRO= 187.920

ECHS=1/
 ECHZ=1/
 PC = 181.0
 LICENCE , 1570

TERRAIN

DISTANCES

COTES

184.20
184.19-29.94
-29.07

DISTANCES

DISTANCES

COTES

184.24 -22.09

187.53 -15.50

187.57 -14.50

187.66 -12.00

187.92 -1.50

187.96 0.00

187.92 1.50

187.66 12.00

187.57 14.50

187.53 15.50

184.54 21.48

184.60 29.33

DISTANCES

COTES

ASSISE

COTES

DISTANCES


COTES

PROFIL 46

G2.PIS

S = 10/5,000
ZTN = 184,741
ZPRO= 187,340

LICENCE : 157
ECHS=1/
ECHZ=1/
PC = 182,0

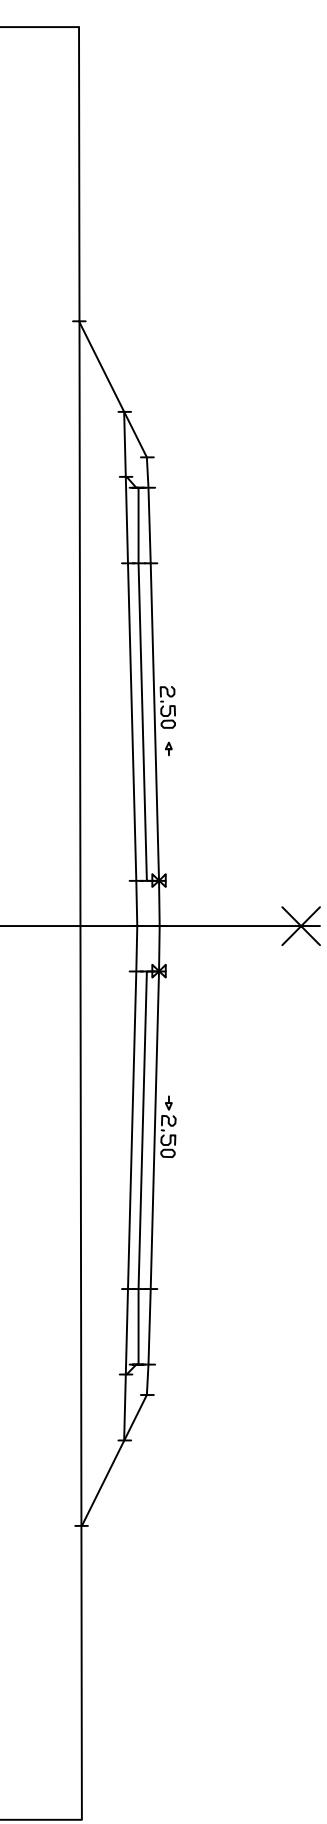

TERRAIN

DISTANCES

COTES

184.68 -29.72

DISTANCES

ASSISE CÔTESS

PROFIL 47

G2PIS

S = 1100.000
 ZTN = 184.266
 ZPRO= 186.760

ECHS=1/
 ECHZ=1/
 PC = 181.0
 LICENCE , 1570


ASSISE	DISTANCES	DISTANCES		COTES	TERRAIN
		DISTANCES	COTES		
185.62	-16.99	184.23	-19.79	184.21	-29.72
185.75	-12.00	186.37 186.41	-15.50 -14.50	186.50	-12.00
186.01	-1.50	186.76	-1.50		
186.05	0.00	186.80	0.00		
186.01	1.50	186.76	1.50		
185.75	12.00	186.50	12.00		
185.62	16.99	186.41 186.37	14.50 15.50	184.31	19.63
				184.33	29.56

PROFIL 48

G2,PIS

S = 1125.000
ZTN = 183.332
ZPRD = 186.179


LICENCE : 1570
ECHZ=1/ 250
PC = 180.0

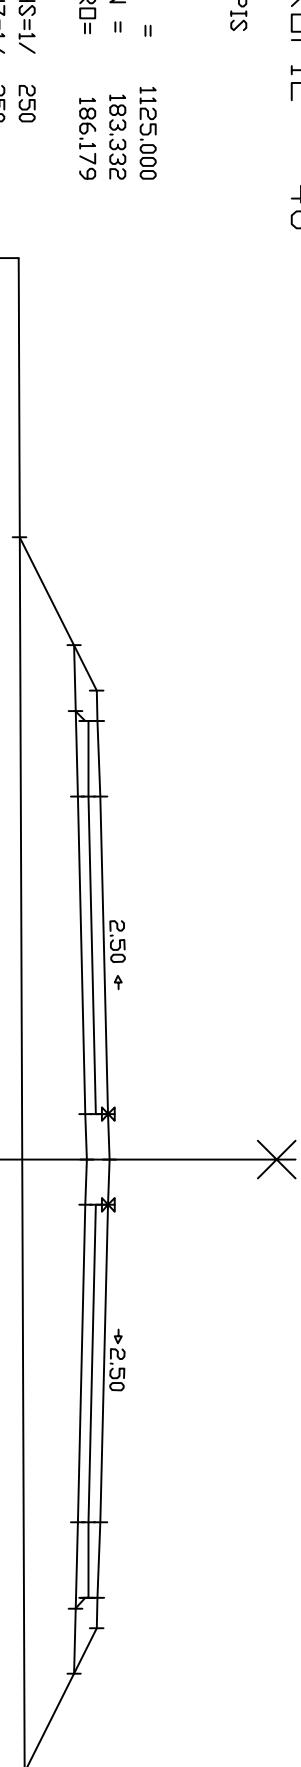

PROFIL 49

G2,PIS


S = 1129.356
ZTN = 183.191
ZPRO = 186.078

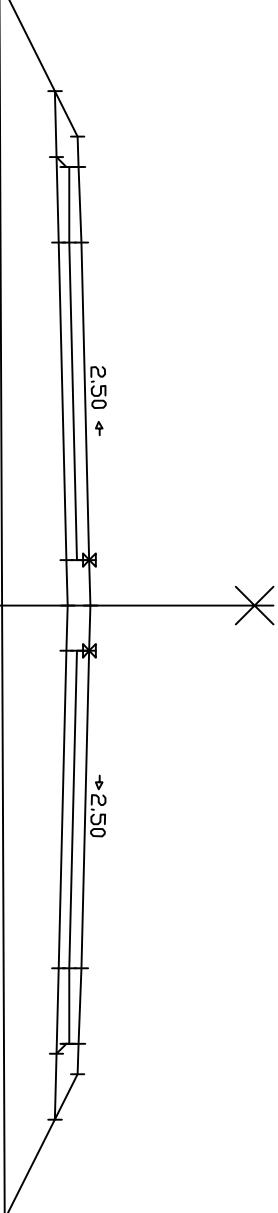

TERRAIN				DISTANCES	COTES
PROJECT				DISTANCES	COTES
ASSISE	COTES	DISTANCES	COTES		
				183.07	-29.80
184.94	-16.99	183.11	-20.66		
		185.69	-15.50		
		185.73	-14.50		
185.07	-12.00	185.82	-12.00		
185.33	-1.50	186.08	-1.50		
185.37	0.00	186.12	0.00		
185.33	1.50	186.08	1.50		
185.07	12.00	185.82	12.00		
		185.73	14.50		
		185.69	15.50		
184.94	16.99	183.27	20.33		
				183.31	29.47

PROFIL 50

S	=	1150.000
ZTN	=	182.764
ZPRO	=	185.599
ECHS=1/	250	
ECHZ=1/	250	
PC	=	180.0
LICENCE :		1570

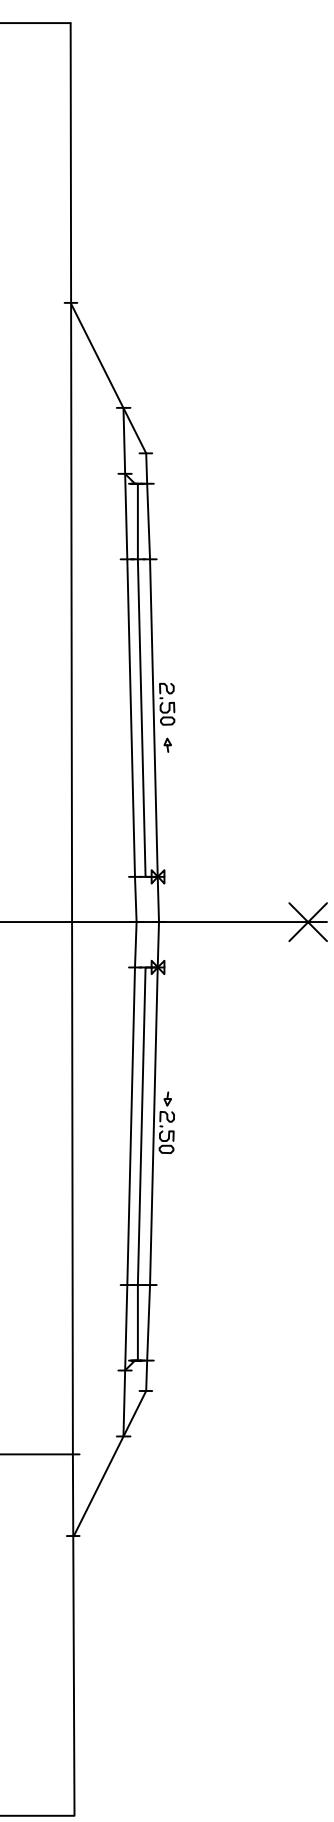


TERRAIN				DISTANCES	PC = 180.0 LICENCE : 1570
PROJECT		COTES	DISTANCES	COTES	
ASSISE	COTES	DISTANCES	COTES	DISTANCES	
184.46	-16.99	182.73	-20.47	182.71	-29.72
184.59	-12.00	185.21 185.25	-15.50 -14.50		
184.85	-1.50	185.34	-12.00		
184.89	0.00	185.60	-1.50		
184.85	1.50	185.64	0.00		
184.59	12.00	185.60	1.50		
184.46	16.99	185.34	12.00	182.80	17.60
		185.25 185.21	14.50 15.50		
		182.81	20.30		
				182.85	29.55

		TERRAIN		DISTANCES	COTES
		DISTANCES		COTES	
		PROJECT	COTES		
ASSISE	DISTANCES				
183.88	-16.99	182.33	-20.09	182.32	-29.70
		184.63 184.67	-15.50 -14.50		
184.01	-12.00	184.76	-12.00		
184.27	-1.50	185.02	-1.50		
184.31	0.00	185.06	0.00		
184.27	1.50	185.02	1.50		
184.01	12.00	184.76	12.00		
		184.67 184.63	14.50 15.50		
183.88	16.99	182.39	19.97		
				182.41	29.58

PROFIL 51
G2PIS

S = 1175.000
ZTN = 182.364
ZRD= 185.019


ECHS=1/
ECHZ=1/
PC = 179.0
LICENCE , 1570

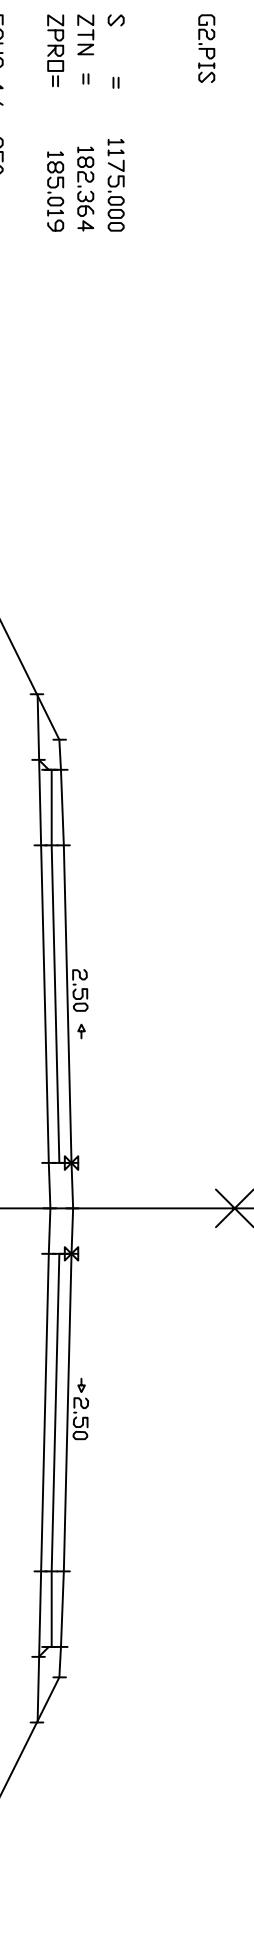

PROFIL 52

G2,PIS

S = 120000
 ZTN = 181.964
 ZPRD= 184.439
 ECHS=1/
 ECHZ=1/
 PC = 179.0
 LICENCE : 1570

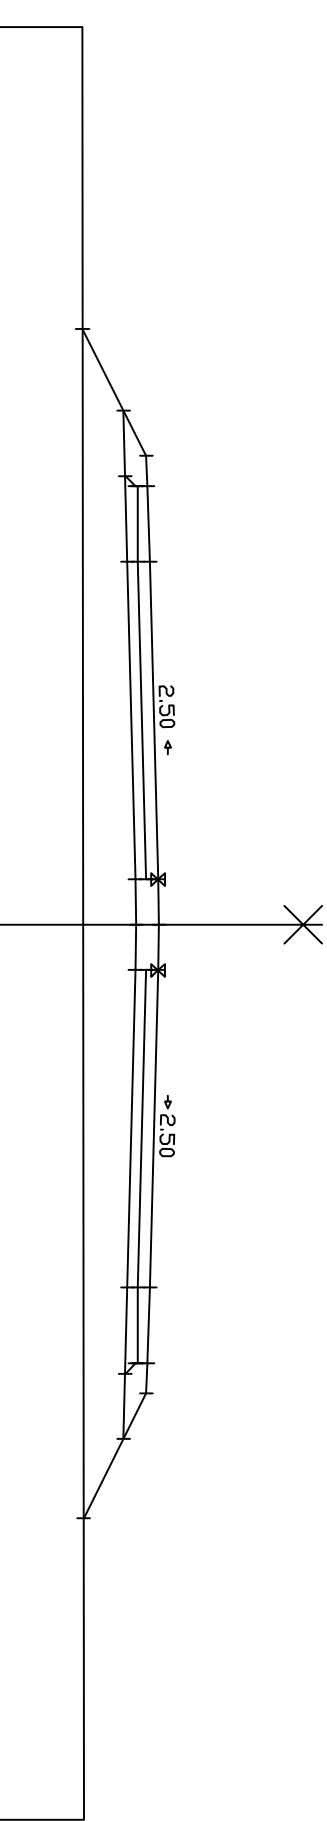


PROFIL 53

G2PIS

S = 1225.000
 ZTN = 182.203
 ZPRO= 183.859

ECHS=1/
 ECHZ=1/
 PC = 179.0
 LICENCE , 1570

		DISTANCES		TERRAIN	DISTANCES COTES	DISTANCES COTES	DISTANCES COTES
PROJECT	ASSISE	DISTANCES COTES	DISTANCES COTES				
182.72	-16.99	182.25	-17.94		182.28	-29.55	
182.85	-12.00	183.47 183.51	-15.50 -14.50				
182.85	12.00	183.60	-12.00				
183.11	-1.50	183.86	-1.50				
183.15	0.00	183.90	0.00				
183.11	1.50	183.86	1.50				
182.72	16.99	183.51 183.47 182.16	14.50 15.50 18.12				
				182.13	29.73		

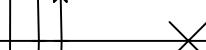

2.50 ↗




→ 2.50

PROFIL 54

G2,PIS

S = 1250.000
ZTN = 181.184
ZPRO= 183.279


LICENCE : 157
PC = 178,0
ECHZ=1/
ECHS=1/
250

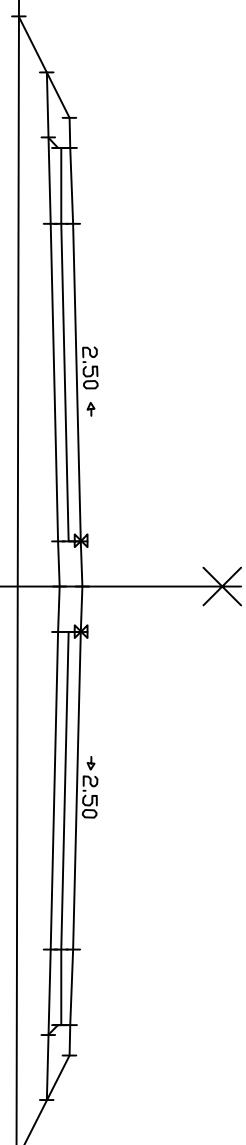

PROFIL 55 GÖRIS

S = 1275.000
ZTN = 179.772
ZPRO = 182.699

ECHZ=1/ 250
PC = 177.0
LICENCE : 1570

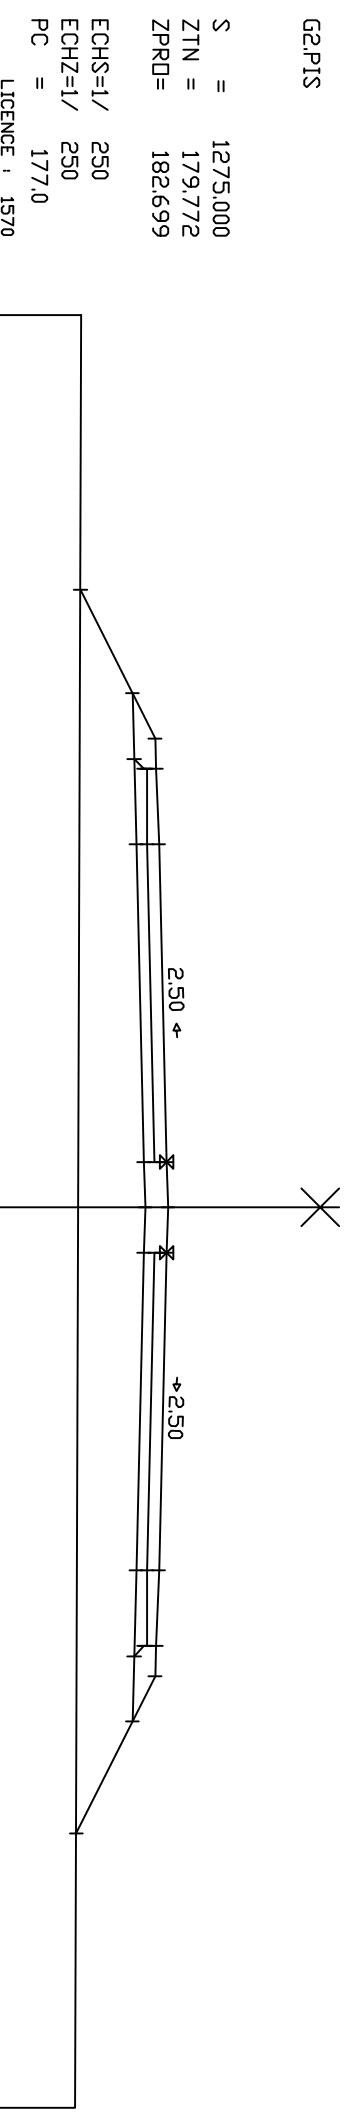

PROFIL 56

GZ.PIS

S = 1300.000
 ZTN = 179.925
 ZPRD= 182.128

ECHS=1/
 ECHZ=1/
 PC = 177.0
 LICENCE , 1570

TERRAIN
 DISTANCES
 COTES

179.78 -29.53

DISTANCES
 COTES

179.98 -18.38

DISTANCES
 COTES

180.99 -16.99

DISTANCES
 COTES

181.12 -12.00

DISTANCES
 COTES

181.38 -1.50

DISTANCES
 COTES

181.42 0.00

DISTANCES
 COTES

181.38 1.50

DISTANCES
 COTES

181.12 12.00

DISTANCES
 COTES

180.99 16.99

PROFIL 57

G2PIS

S = 1325.000
 ZTN = 179.842
 ZPRO= 181.602

ECHS=1/
 ECHZ=1/
 PC = 250
 LICENCE , 176.0
 1570

		TERRAIN		DISTANCES			
		DISTANCES		COTES			
		PROJECT		COTES			
ASSISE	DISTANCES	COTES	COTES	COTES	COTES	COTES	COTES
180.47	-16.99	180.42	-17.08	180.28	-28.87		
		181.21	-15.50				
		181.25	-14.50				
180.59	-12.00	181.34	-12.00				
180.85	-1.50	181.60	-1.50	180.61	-2.41		
180.89	0.00	181.64	0.00				
180.85	1.50	181.60	1.50	179.36	1.51		
180.59	12.00	181.34	12.00				
		181.25	14.50				
		181.21	15.50				
180.47	16.99	179.65	18.62				
				179.85	30.41		

PRODUCED BY AN AUTODESK STUDENT VERSION


PROFIL 58

G2,PIS

S = 1350.000
ZTN = 179.887
ZPRO= 181.128

EUCHS=1/
ECHZ=1/
PC = 177,0

LICENCE : 1570

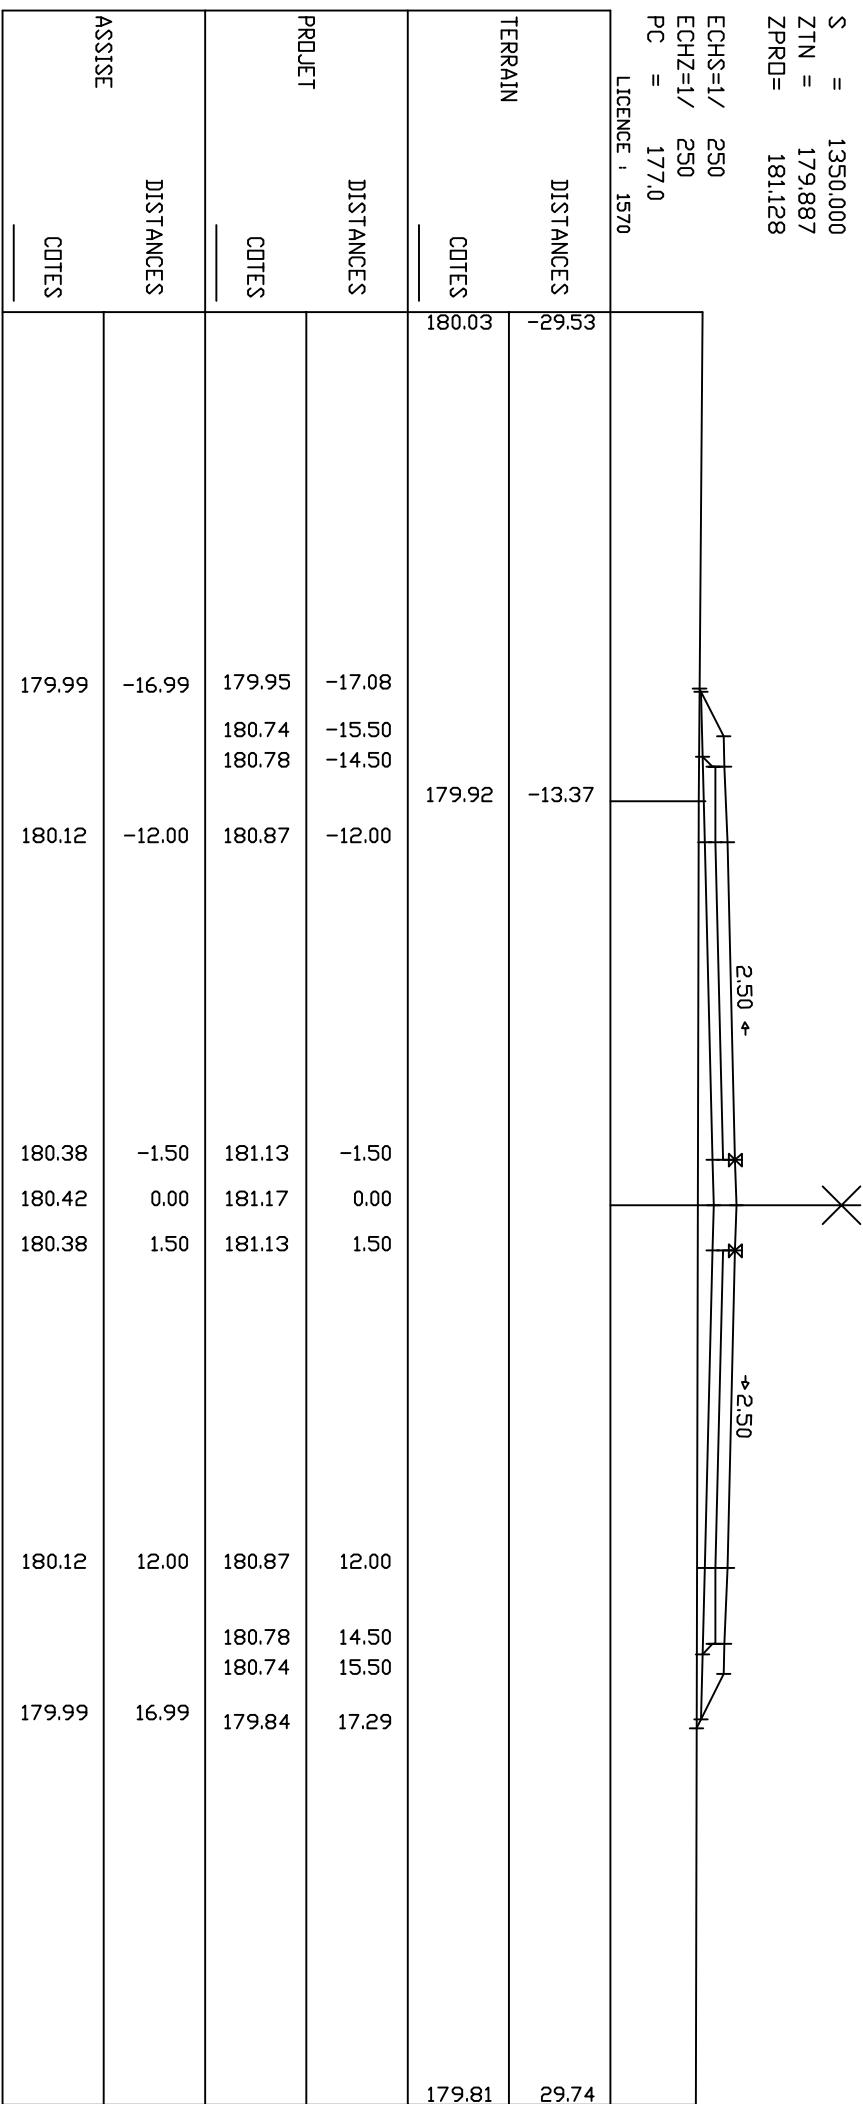


PROFIL 59

G2,PIS


S = 1375.000
ZTN = 179.719
ZPRO = 180.702


ECHS=1/
ECHZ=1/
PC = 177.0


LICENCE : 1570

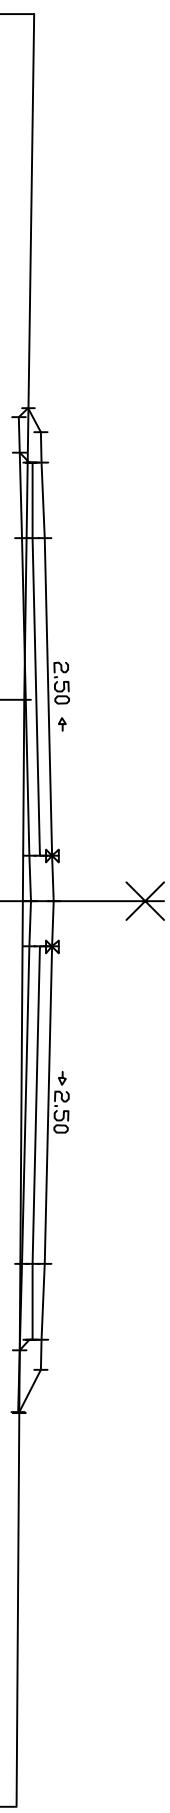

TERRAIN				DISTANCES	LICENCE : 1570
PROJECT				COTES	-29.33
ASSISE				DISTANCES	
				COTES	
179.59	-16.00	179.90 180.31 180.35	-16.32 -15.50 -14.50	180.09	
179.69	-12.00	180.44	-12.00	179.77	-6.66
179.95	-1.50	180.70	-1.50		
179.99	0.00	180.74	0.00		
179.95	1.50	180.70	1.50		
179.69	12.00	180.44	12.00		
		180.35 180.31	14.50 15.50		
179.57	16.89	179.60	16.93		
				179.51	29.94

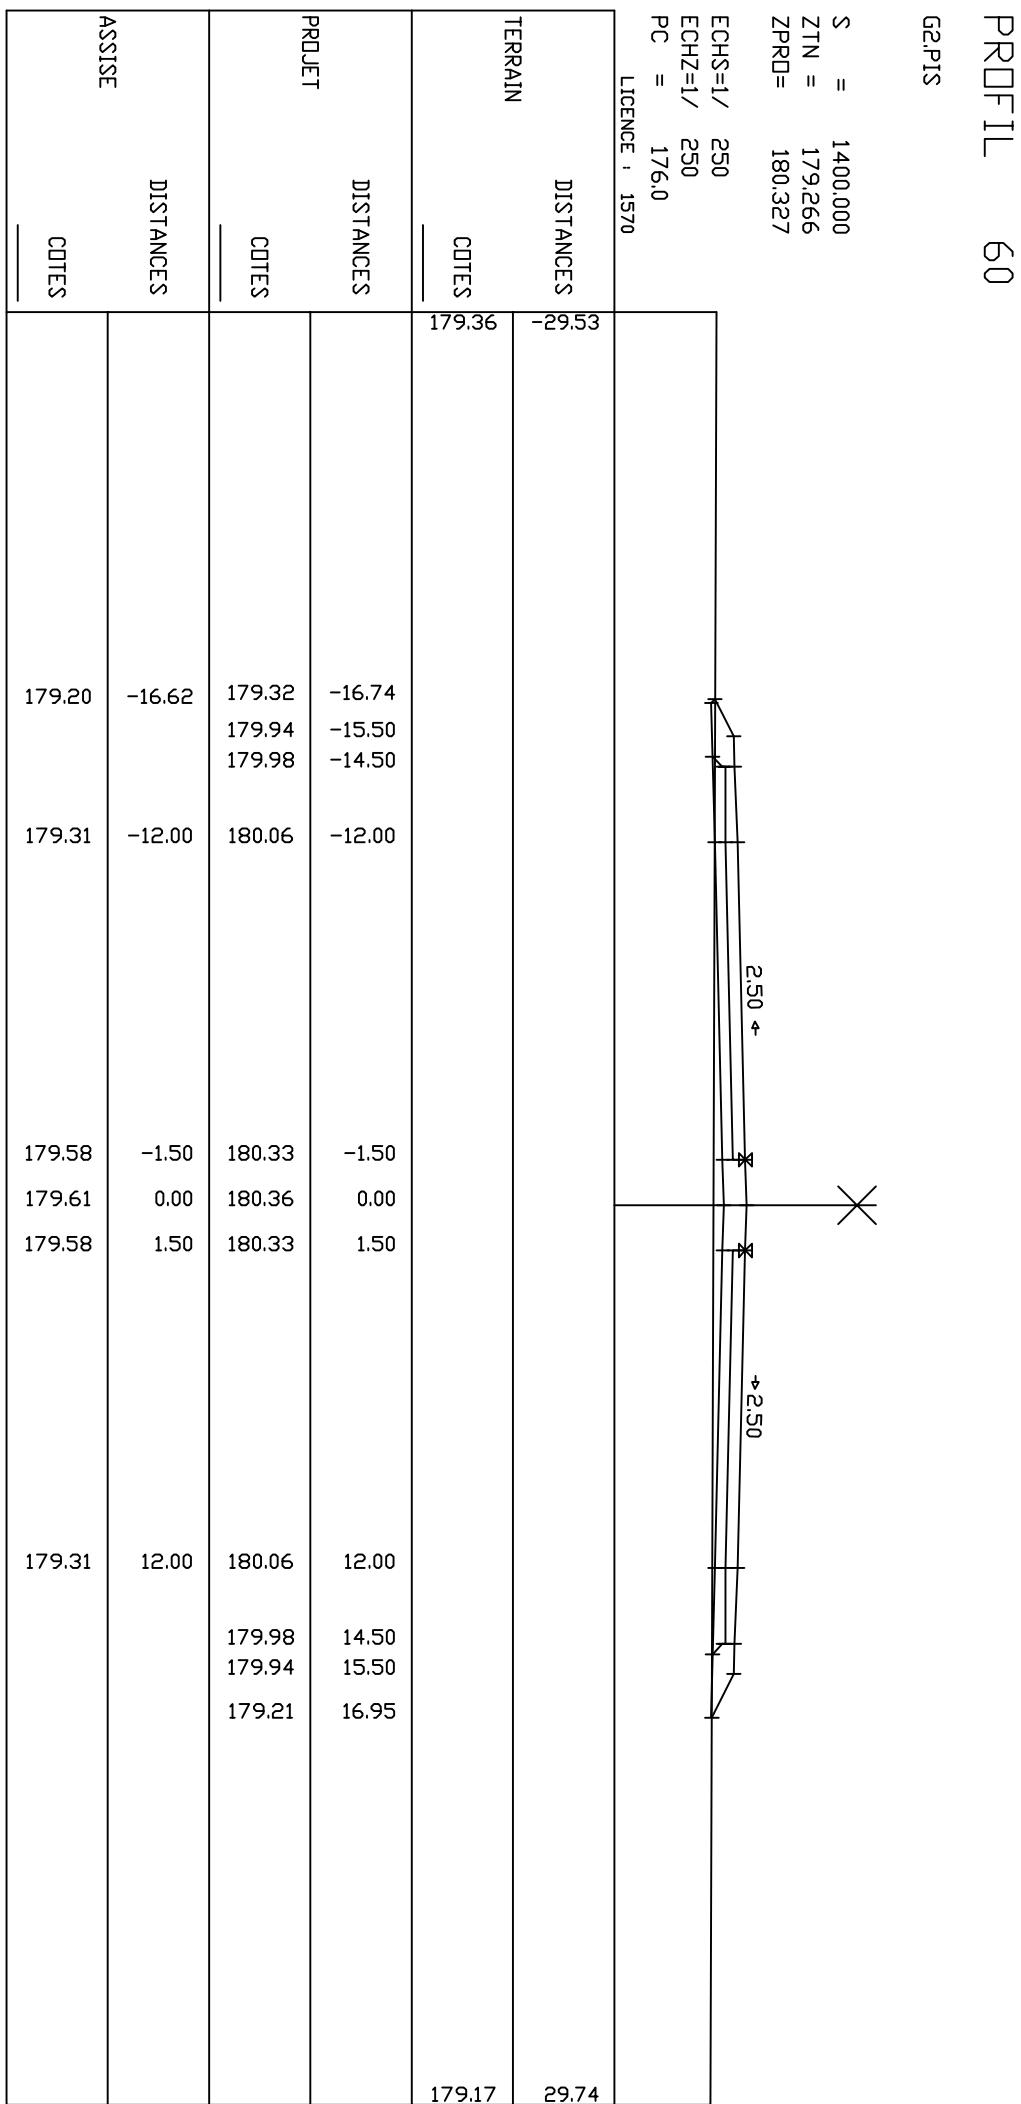

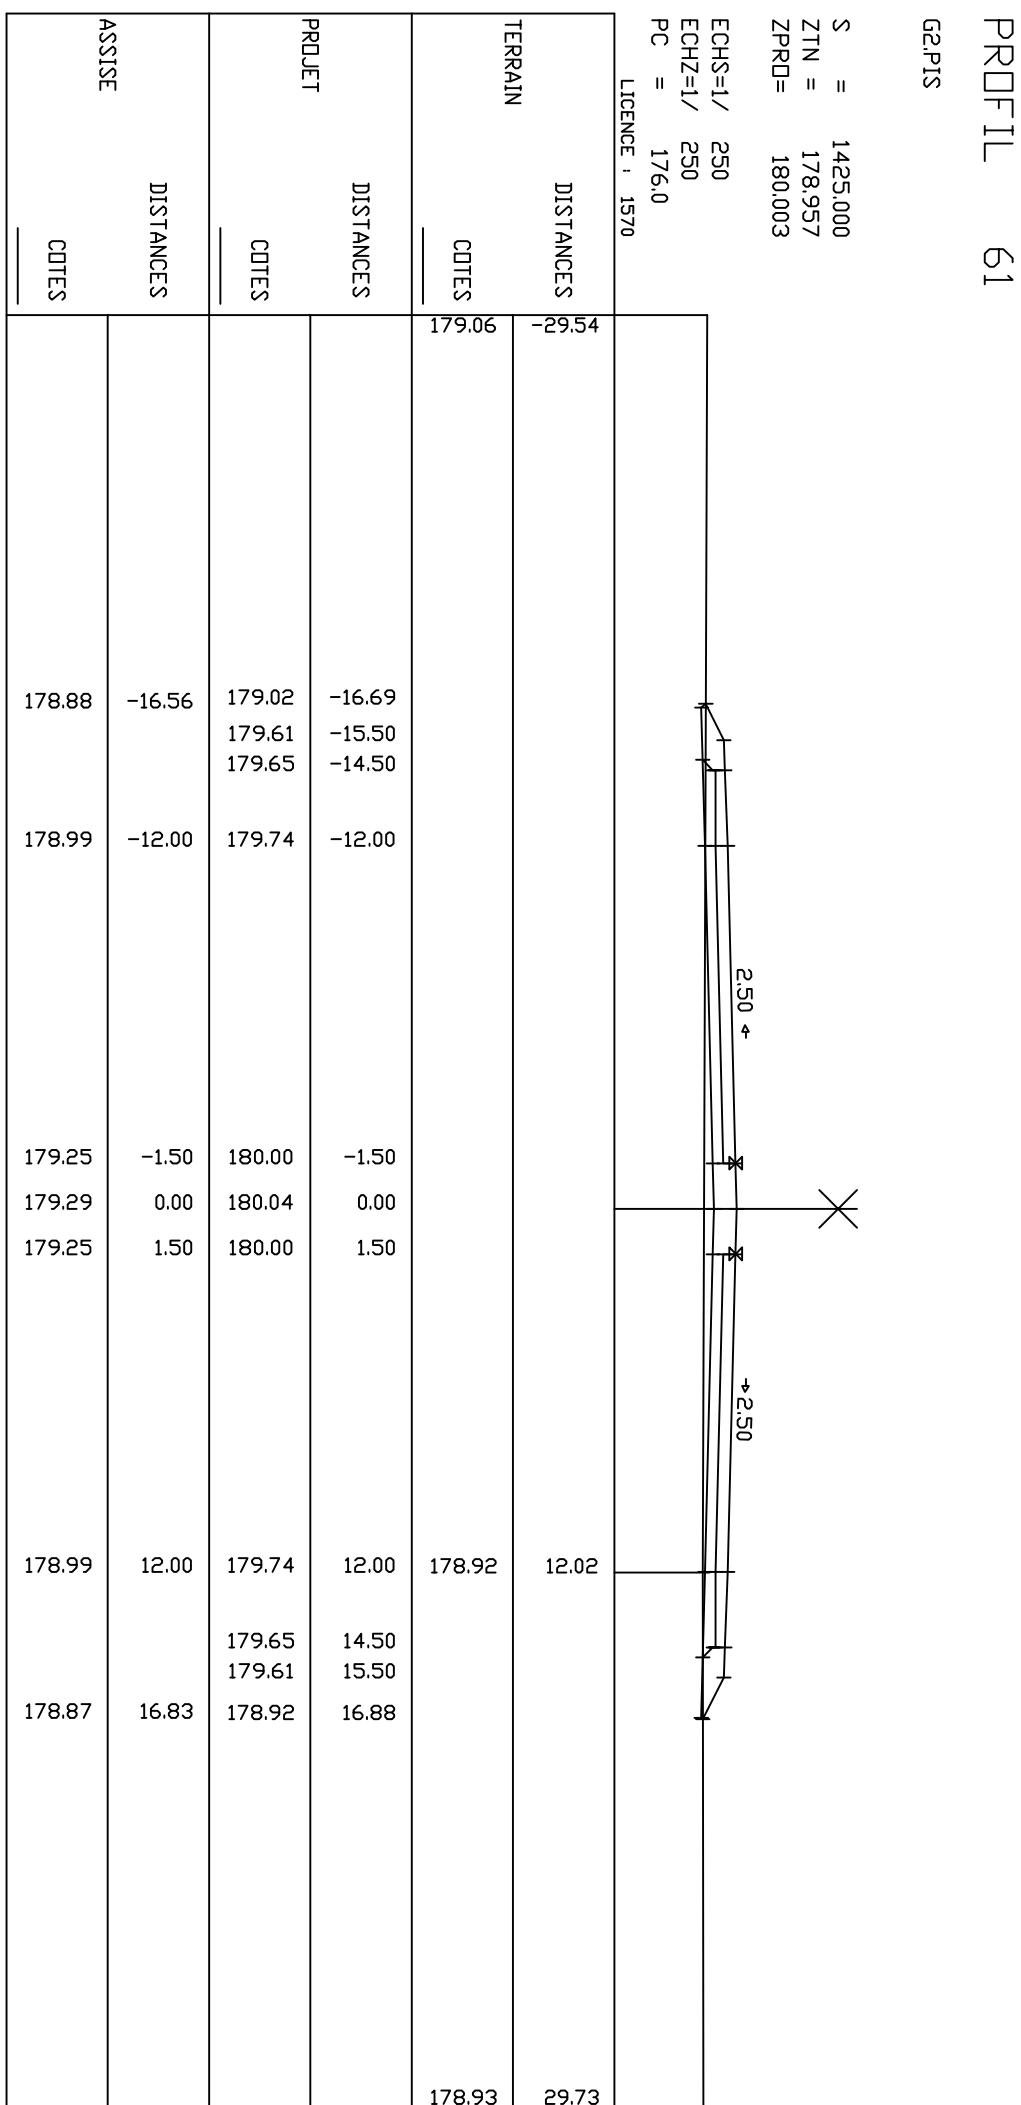

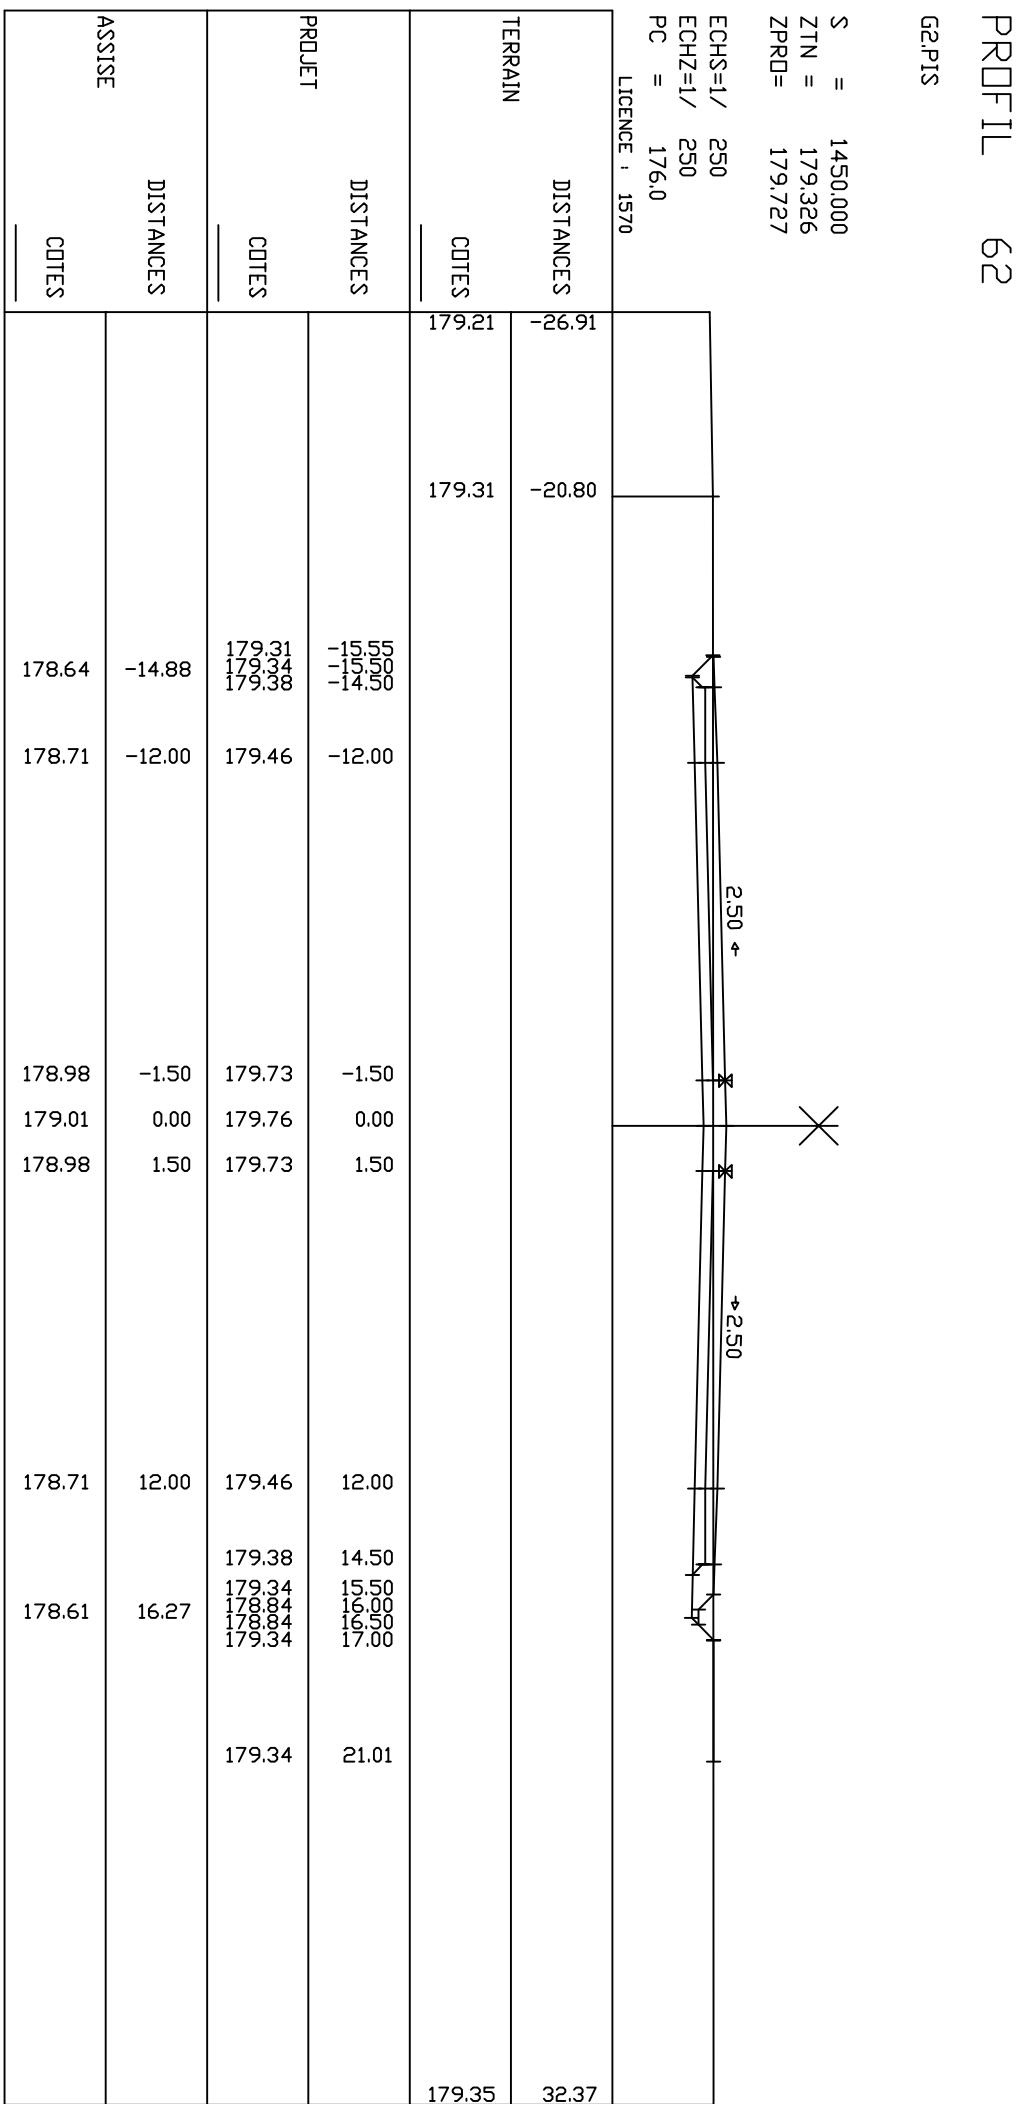

PROFIL 63

G2PIS

S = 1475.000
 ZTN = 178.721
 ZPRO= 179.503

ECHS=1/
 ECHZ=1/
 PC = 175.0
 LICENCE , 1570

TERRAIN

DISTANCES

COTES

178.27 -30.13

DISTANCES

COTES

PROJECT


COTES

DISTANCES

COTES

ASSISE

COTES

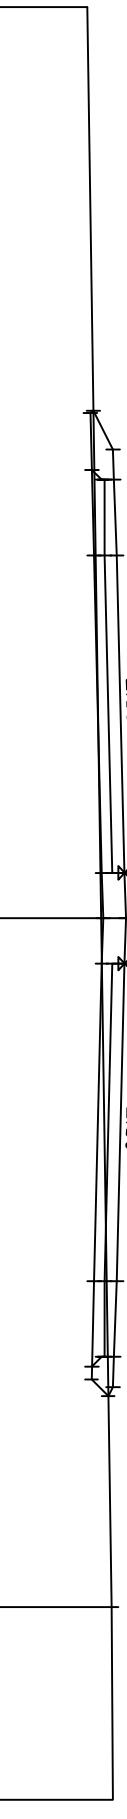

PROFIL 64

G2PIS

S = 1491959
 ZTN = 177.991
 ZPRO= 179.378


ECH\$=1/ 250


ECHZ=1/ 250


PC = 175.0

LICENCE , 1570

		DISTANCES		DISTANCES		DISTANCES		DISTANCES		DISTANCES	
		COTES		COTES		COTES		COTES		COTES	
PROJECT											
ASSISE		DISTANCES	COTES	DISTANCES	COTES	DISTANCES	COTES	DISTANCES	COTES	DISTANCES	COTES
178.24	-16.99	177.82	177.81	-17.83	-19.77	177.66	-29.96				
178.37	-12.00	179.12	179.12	-12.00							
178.63	-1.50	179.38	179.38	-1.50							
178.67	0.00	179.42	179.42	0.00							
178.63	1.50	179.38	179.38	1.50							
178.37	12.00	179.12	179.12	12.00							
178.24	16.99	178.15	178.15	17.17	178.18	178.29	20.68	29.31			

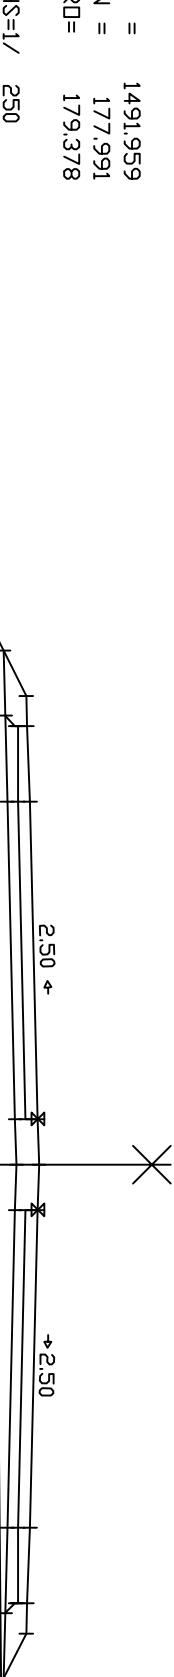

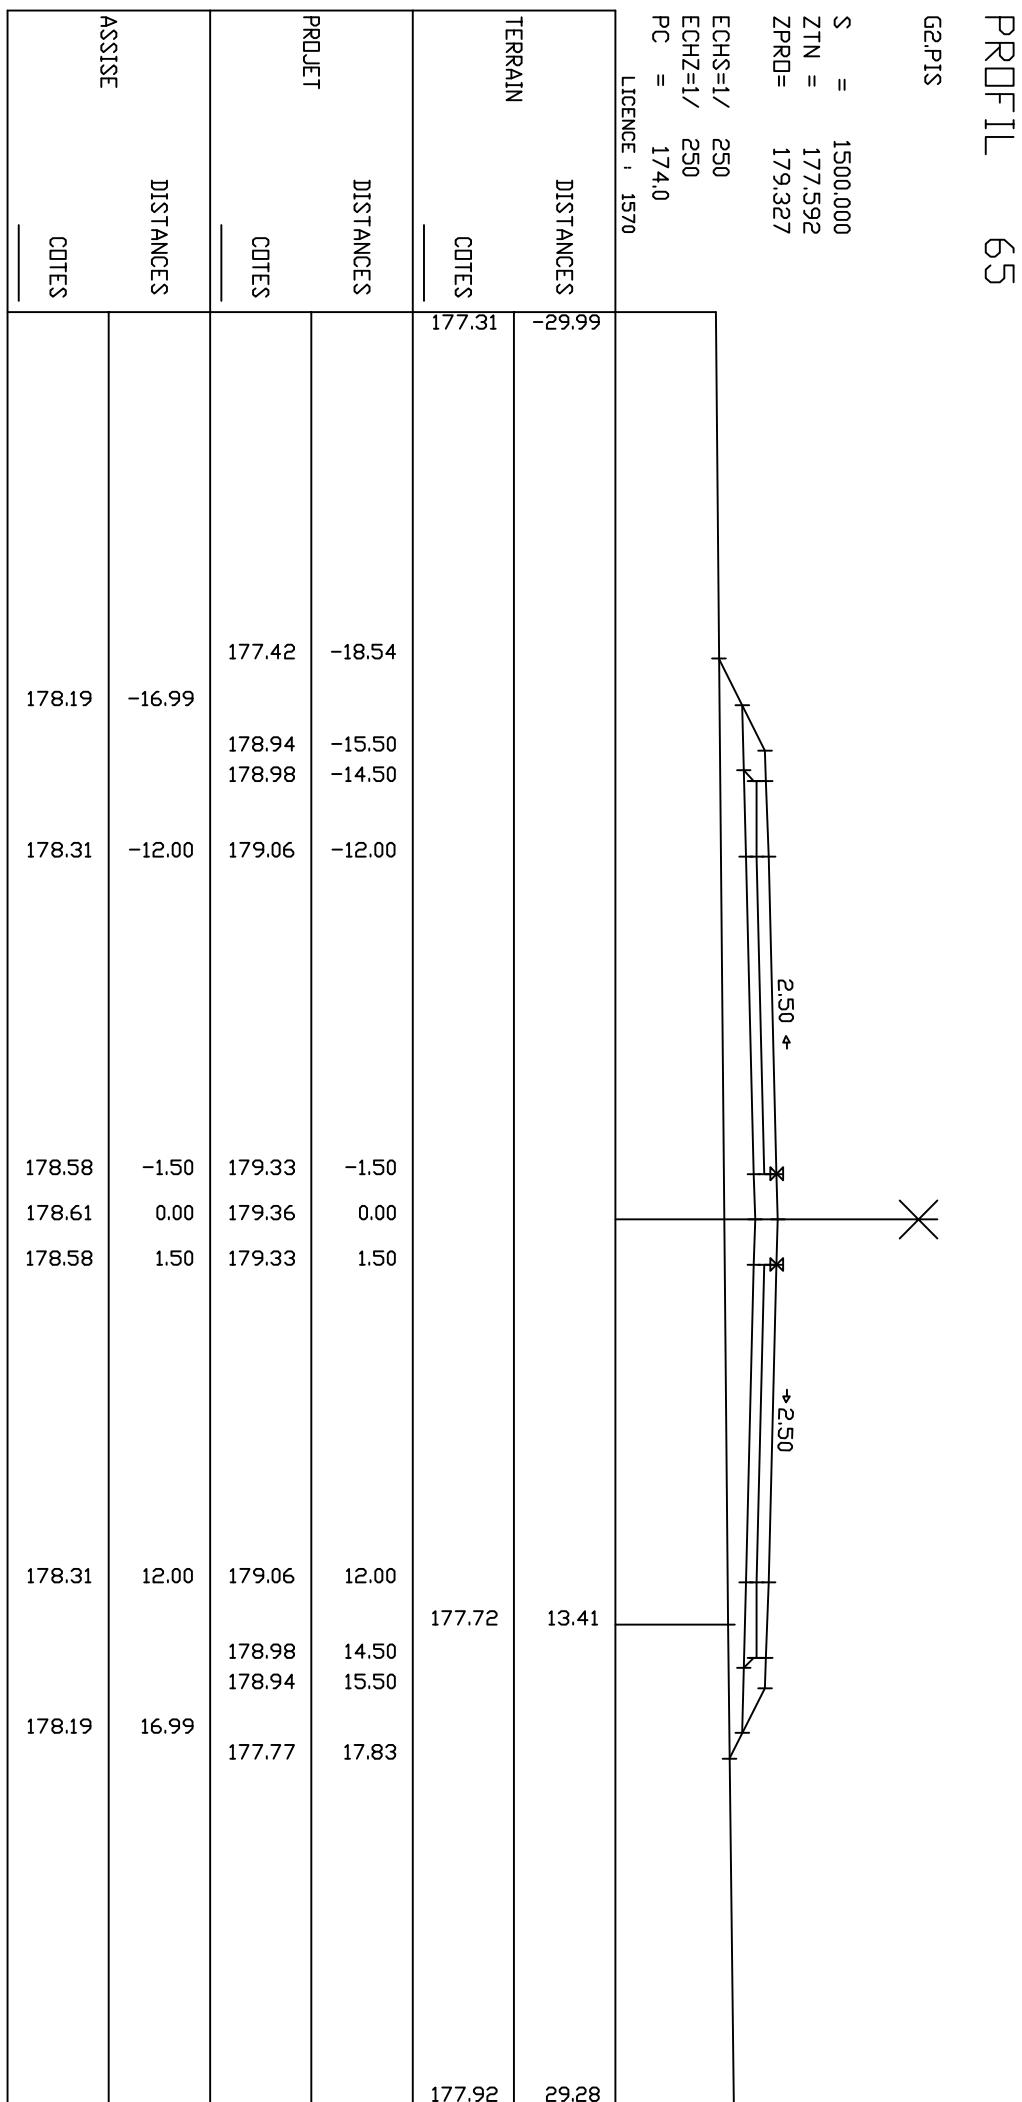

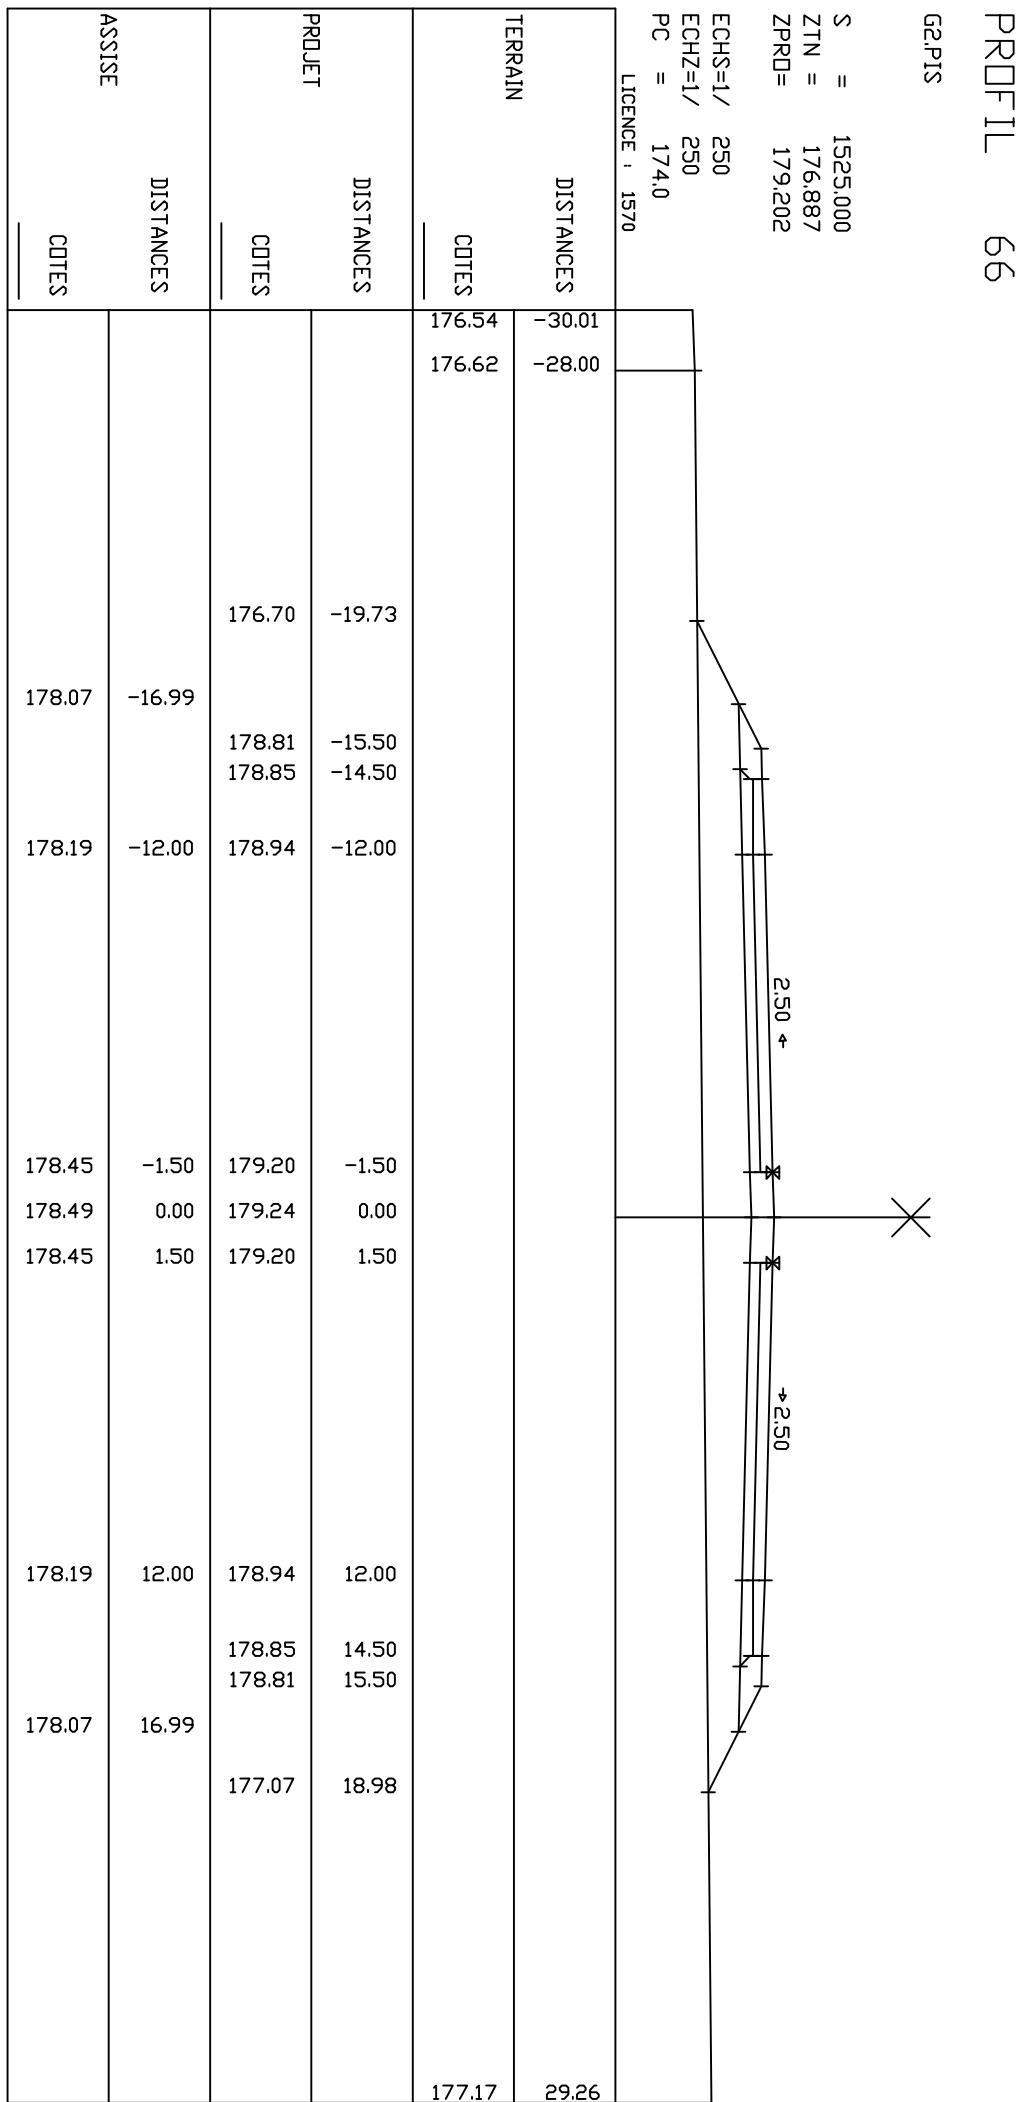

PROFIL 67

G2PIS

S = 1550.000
 ZTN = 176.244
 ZPRO= 179.128

ECHS=1/
 ECHZ=1/
 PC = 172.0
 LICENCE , 1570

TERRAIN

DISTANCES

COTES

175.22
175.28

-30.49


-29.74

PROFIL 68

G2PIS

S = 1575.000
 ZTN = 175.103
 ZPRO= 179.102


ECHS=1/
 ECHZ=1/
 PC = 171.0
 LICENCE , 1570

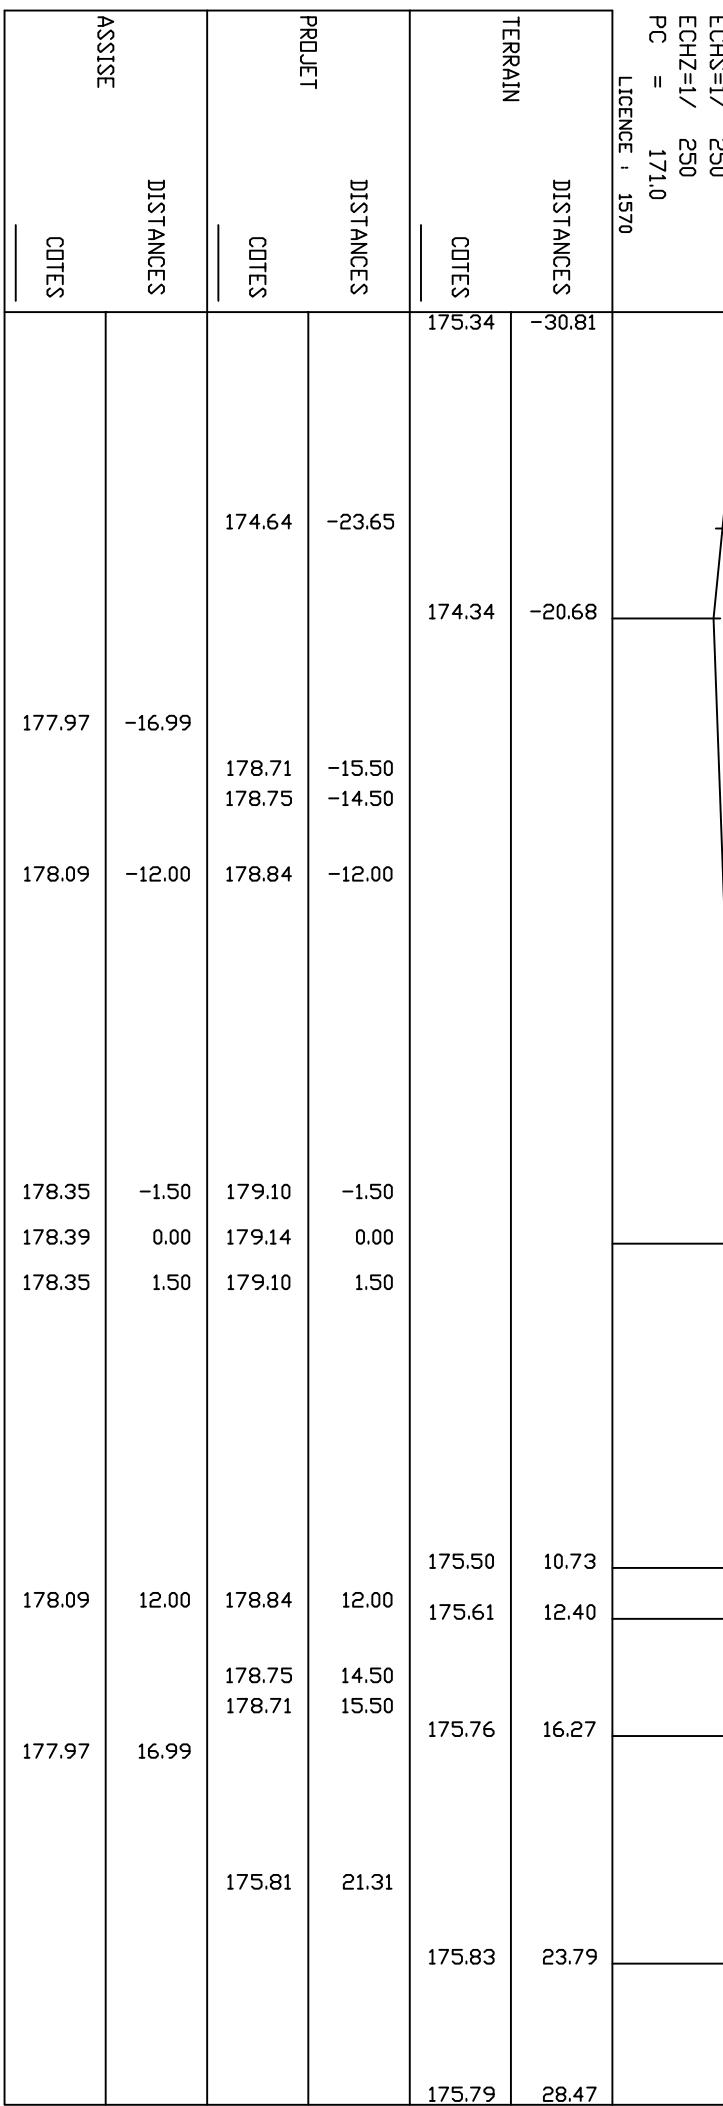

PROFIL 69

G2,PIS

S	=	1600.00
ZTN	=	173815
ZPRD	=	179128
ECHS=1/	250	
ECHZ=1/	250	
PC	=	171.0
LICENCE	,	1570

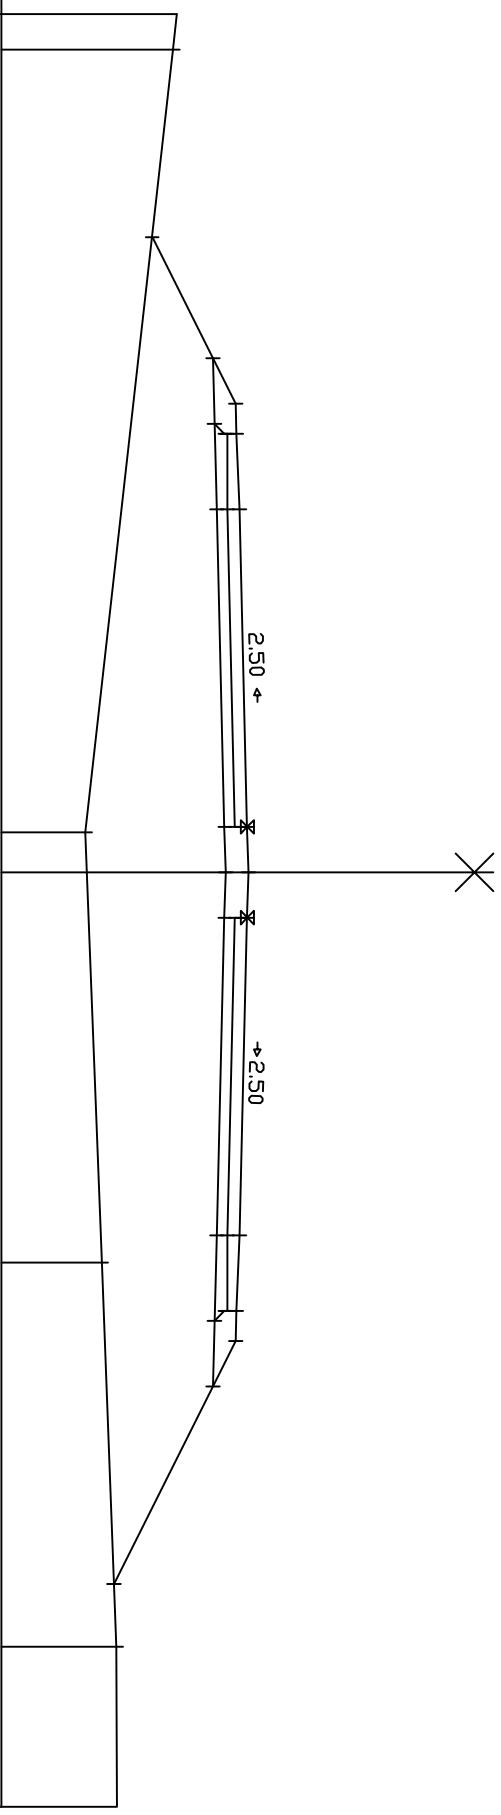

PROFIL 70

G2PIS

S = 1625.000
 ZTN = 174.844
 ZPRO= 179.202

ECHS=1/
 ECHZ=1/
 PC = 171.0
 LICENCE , 1570

TERRAIN

DISTANCES

COTES

177.28 -27.35

DISTANCES

COTES

176.85 -21.45

DISTANCES

COTES

174.76 -3.38

DISTANCES

COTES

175.02 7.35

DISTANCES

COTES


174.26 27.36

DISTANCES

COTES

174.07 31.93

ASSISE	DISTANCES	COTES	PROJECT		DISTANCES	COTES	DISTANCES	COTES
			DISTANCES	COTES				
178.07	-16.99	178.81	-15.50	176.66	-19.81	176.85	-21.45	
178.19	-12.00	178.85	-14.50	178.94	-12.00	174.76	-3.38	
178.45	-1.50	179.20	-1.50					
178.49	0.00	179.24	0.00					
178.45	1.50	179.20	1.50					
178.19	12.00	178.94	12.00					
178.07	16.99	178.85	14.50					
		178.81	15.50					
		174.37	24.38					

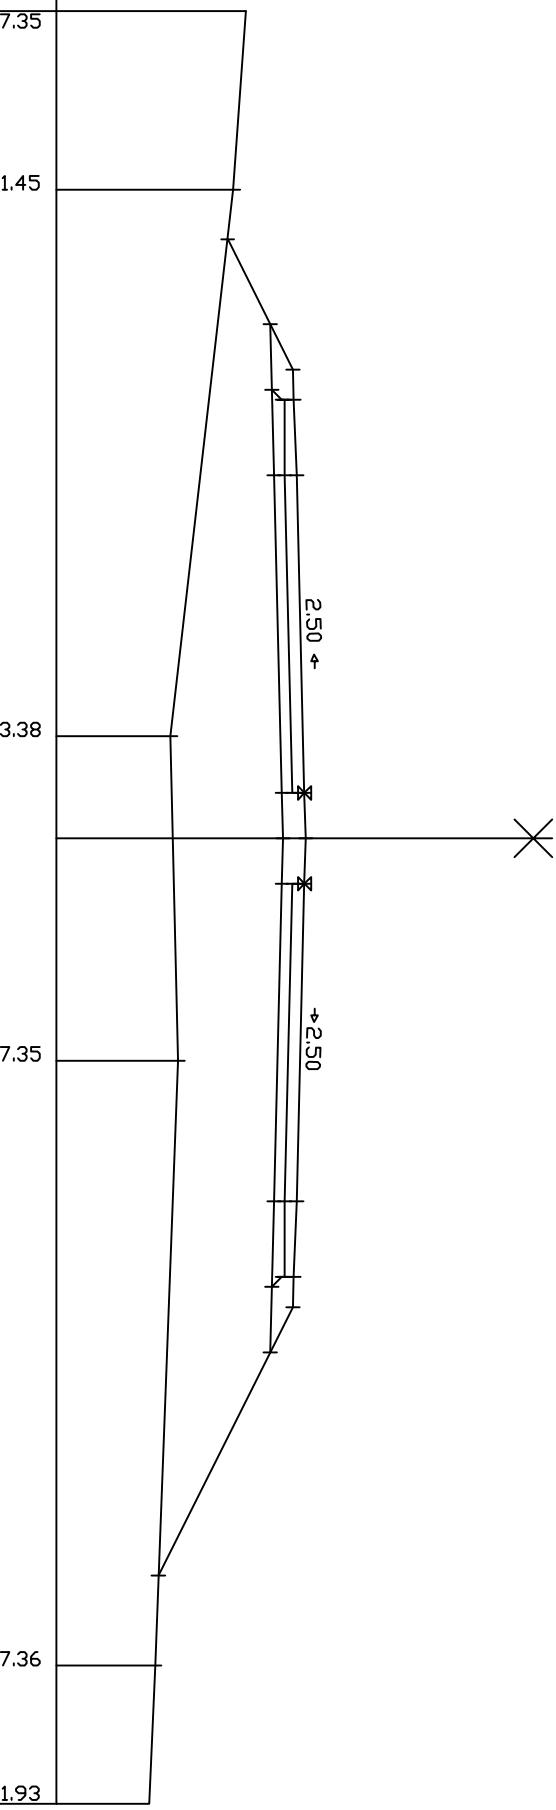

PROFIL 71

G2PIS

S = 1650.000
 ZTN = 175.359
 ZPRO= 179.327

ECHS=1/
 ECHZ=1/
 PC = 171.0
 LICENCE , 1570

TERRAIN

DISTANCES

COTES

177.03 -27.45

TERRAIN

DISTANCES

COTES

176.28 -16.66

TERRAIN

DISTANCES

COTES

175.13 4.21

TERRAIN

DISTANCES

COTES

174.22 16.94

TERRAIN

DISTANCES

COTES

174.42 22.88

TERRAIN

DISTANCES

COTES

174.05 31.83

TERRAIN

DISTANCES

COTES

178.19 -16.99

TERRAIN

DISTANCES

COTES

178.31 -12.00

TERRAIN

DISTANCES

COTES

178.58 -1.50

TERRAIN

DISTANCES

COTES

178.61 0.00

TERRAIN

DISTANCES

COTES

178.58 1.50

TERRAIN

DISTANCES

COTES

178.31 12.00

TERRAIN

DISTANCES

COTES

178.19 16.99

TERRAIN

DISTANCES

COTES

178.98 178.94

TERRAIN

DISTANCES

COTES

174.34 24.69

TERRAIN

DISTANCES

COTES

174.05 31.83

TERRAIN

DISTANCES

COTES

178.94 14.50

TERRAIN

DISTANCES

COTES

174.42 22.88

TERRAIN

DISTANCES

COTES

174.22 16.94

TERRAIN

DISTANCES

COTES

175.13 4.21

TERRAIN

DISTANCES

COTES

176.28 -16.66

TERRAIN

DISTANCES

COTES

177.03 -27.45

TERRAIN

DISTANCES

COTES

178.19 -16.99

TERRAIN

DISTANCES

COTES

178.31 -12.00

TERRAIN

DISTANCES

COTES

178.58 -1.50

TERRAIN

DISTANCES

COTES

178.61 0.00

TERRAIN

DISTANCES

COTES

178.58 1.50

TERRAIN

DISTANCES

COTES

178.31 12.00

TERRAIN

DISTANCES

COTES

178.19 16.99

TERRAIN

DISTANCES

COTES

178.94 14.50

TERRAIN

DISTANCES

COTES

174.34 24.69

TERRAIN

DISTANCES

COTES

174.05 31.83

TERRAIN

DISTANCES

COTES

178.94 14.50

TERRAIN

DISTANCES

COTES

174.42 22.88

TERRAIN

DISTANCES

COTES

174.22 16.94

TERRAIN

DISTANCES

COTES

175.13 4.21

TERRAIN

DISTANCES

COTES

TERRAIN

DISTANCES

COTES

178.19 16.99

TERRAIN

DISTANCES

COTES

178.94 14.50

TERRAIN

DISTANCES

COTES

174.34 24.69

TERRAIN

DISTANCES

COTES

174.05 31.83

TERRAIN

DISTANCES

COTES

178.94 14.50

TERRAIN

DISTANCES


COTES

174.42 22.88

BIBLIOTHECA
72

G2,PIS

S = 16/3,000
ZTN = 176.002
ZPRD= 179.503

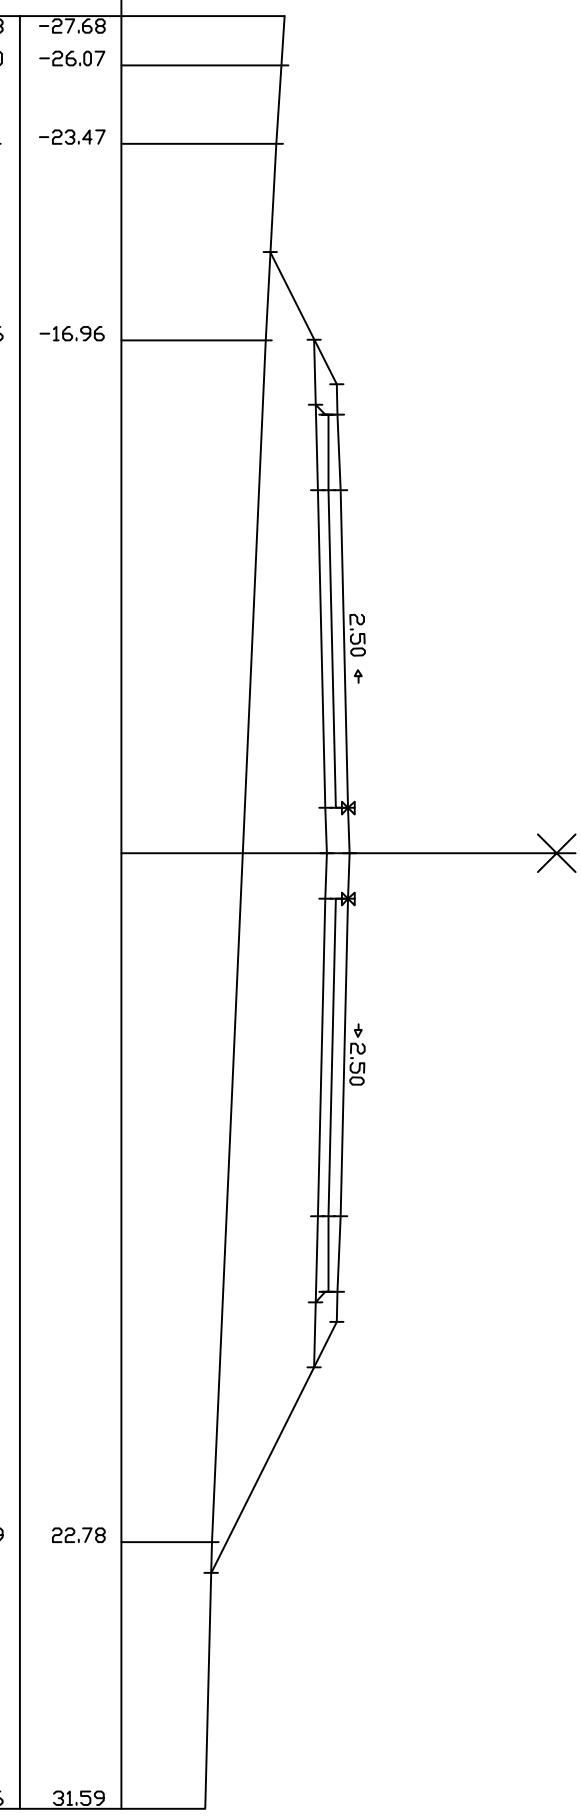



PROFIL 73

G2PIS

S = 1700.000
 ZTN = 177.157
 ZPRO= 179.727

ECHS=1/
 ECHZ=1/
 PC = 173.0
 LICENCE , 1570

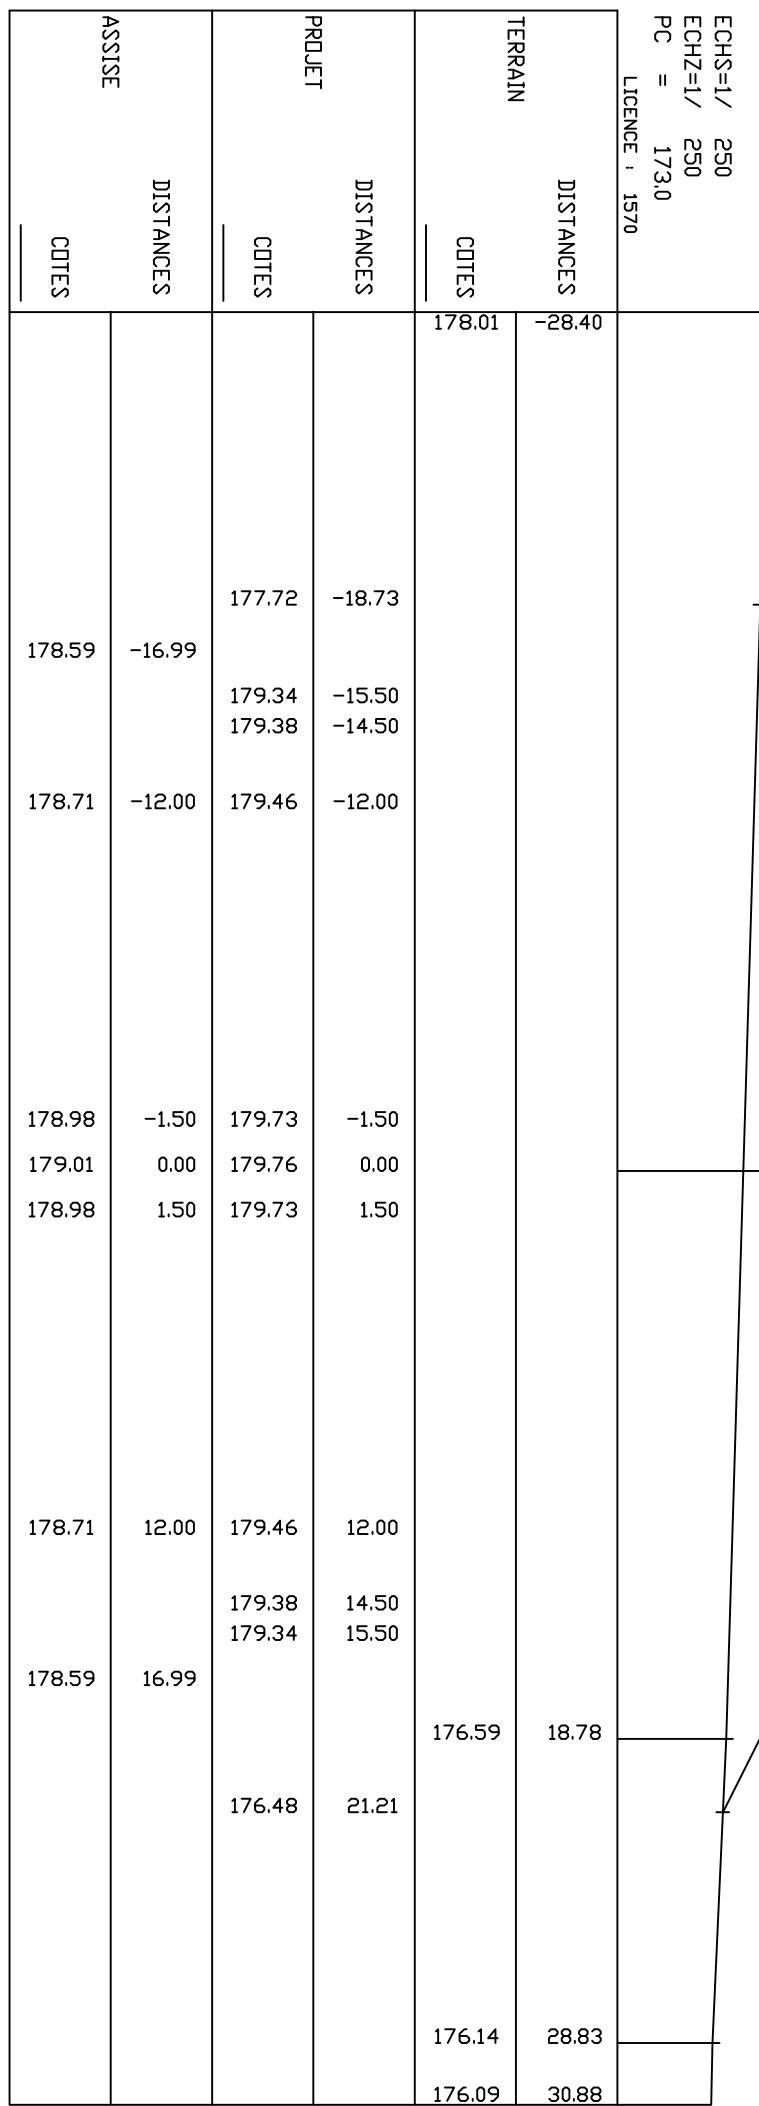

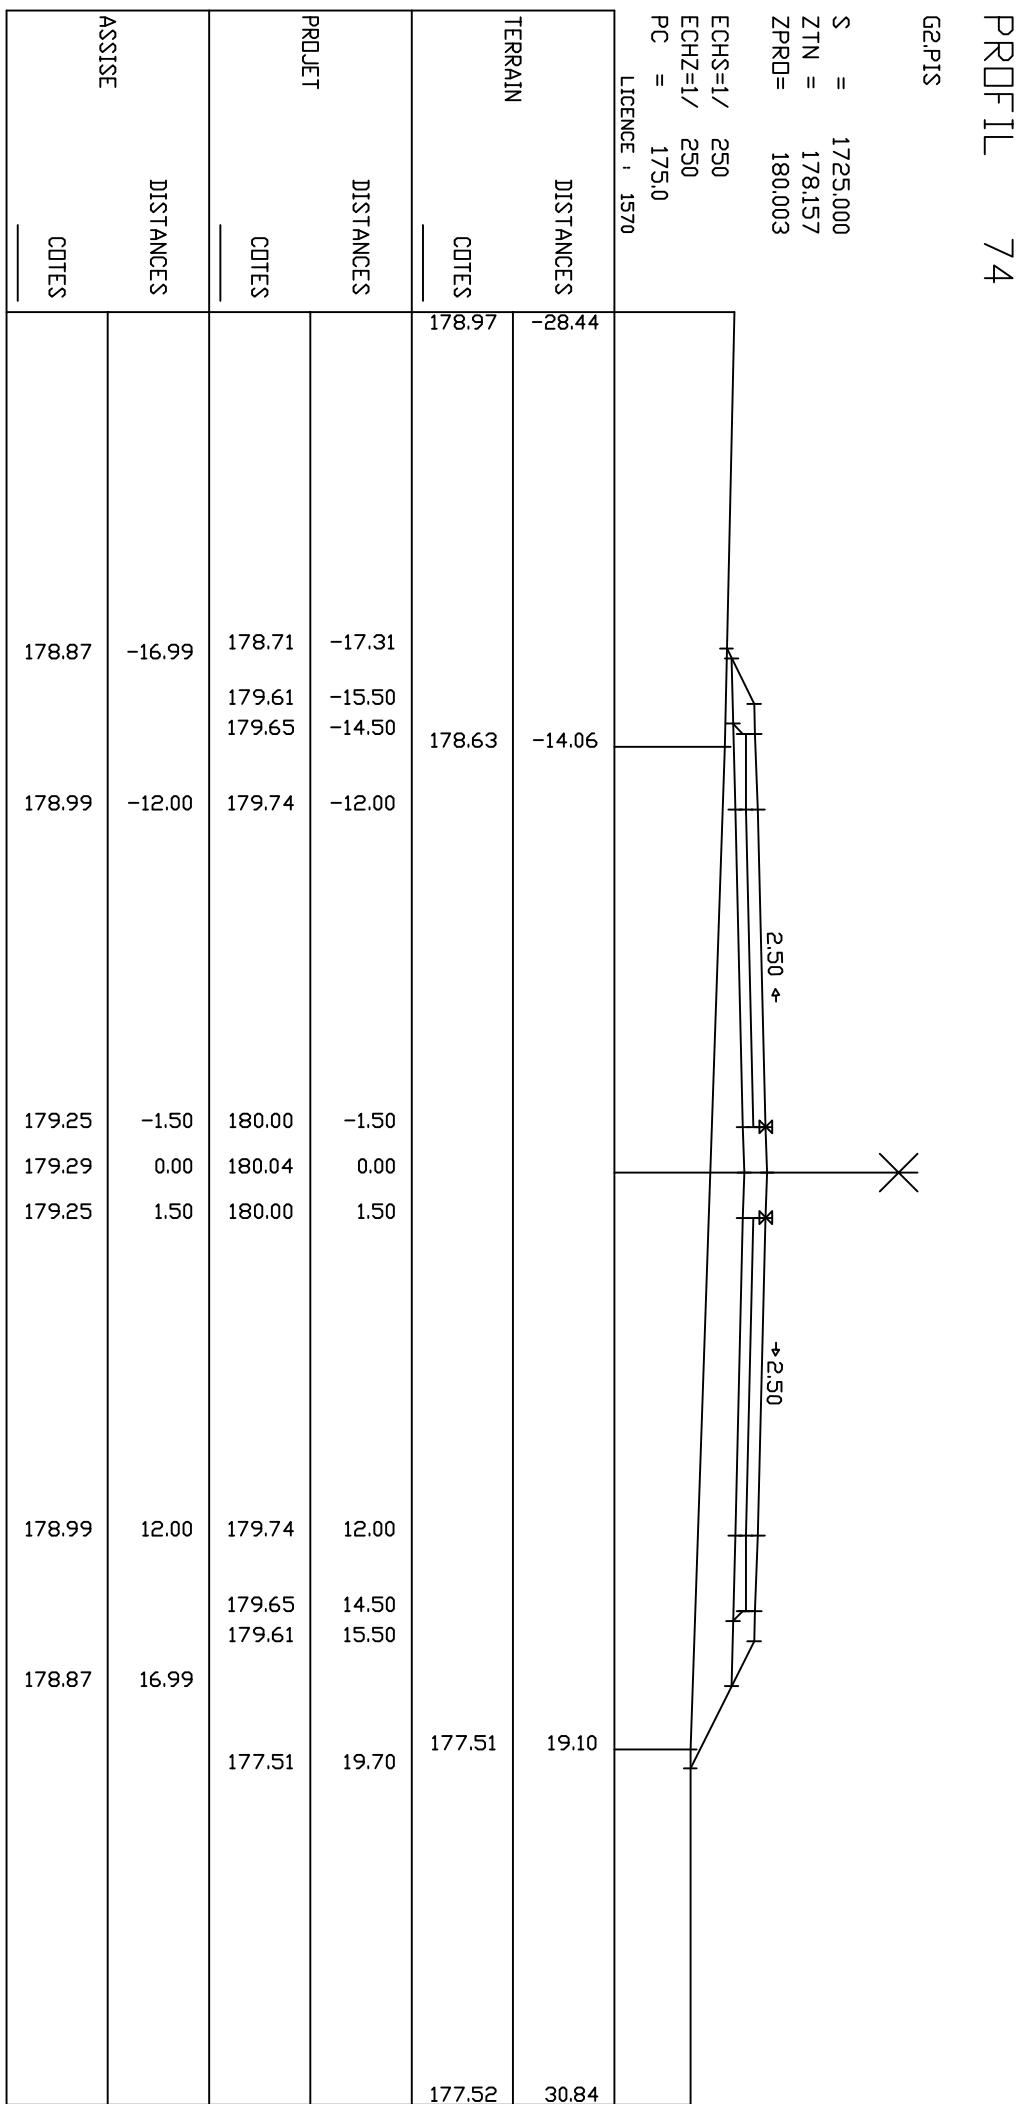


PROFIL 75

G2,PIS

S = 1750.000
ZTN = 179.089
ZPRO = 180.327

ECHS=1/ 250
ECHZ=1/ 250
PC = 176.0

LICENCE , 1570

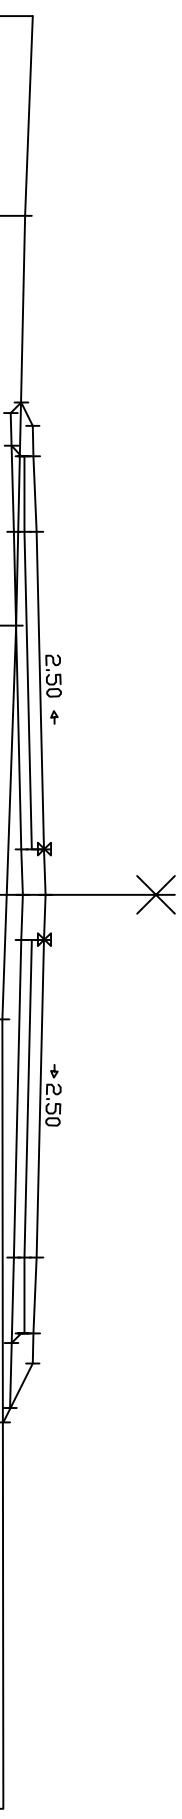

ASSISE		DISTANCES		TERRAIN		DISTANCES	
PROJET	COTES	DISTANCES	COTES	TERRAIN	COTES	DISTANCES	COTES
179.22	-15.91	179.56 179.94 179.98	-16.25 -15.50 -14.50	179.94	-29.04		
179.31	-12.00	180.06	-12.00	179.70	-22.43		
				179.39	-8.88		
179.58	-1.50	180.33	-1.50				
179.61	0.00	180.36	0.00				
179.58	1.50	180.33	1.50	178.95	4.14		
179.31	12.00	180.06	12.00				
		179.98 179.94	14.50 15.50				
179.19	16.99	178.96	17.45				
				178.98	30.24		

PROFIL 76

G2PIS

S = 1775.000
 ZTN = 180.073
 ZPRO= 180.702

ECHS=1/
 ECHZ=1/
 PC = 177,0
 LICENCE , 1570

TERRAIN

DISTANCES

COTES

181.23 -32.26

PROJECT DISTANCES COTES

ASSISE DISTANCES COTES


179.58	-16.27	180.86	-21.82	
		180.86	-17.82	
		180.31	-17.00	
		179.81	-16.50	
		179.81	-16.00	
		180.31	-15.50	
		180.35	-14.50	
179.69	-12.00	180.44	-12.00	
179.95	-1.50	180.70	-1.50	
179.99	0.00	180.74	0.00	
179.95	1.50	180.70	1.50	
				179.97 2.82
179.69	12.00	180.44	12.00	
		180.35	14.50	
		180.31	15.50	
		179.77	16.58	
				179.62 27.02

PROFIL 77

G2PIS

S = 1800.000
 ZTN = 180.717
 ZR0= 181.128

ECHS=1/
 ECHZ=1/
 PC = 177,0
 LICENCE , 1570

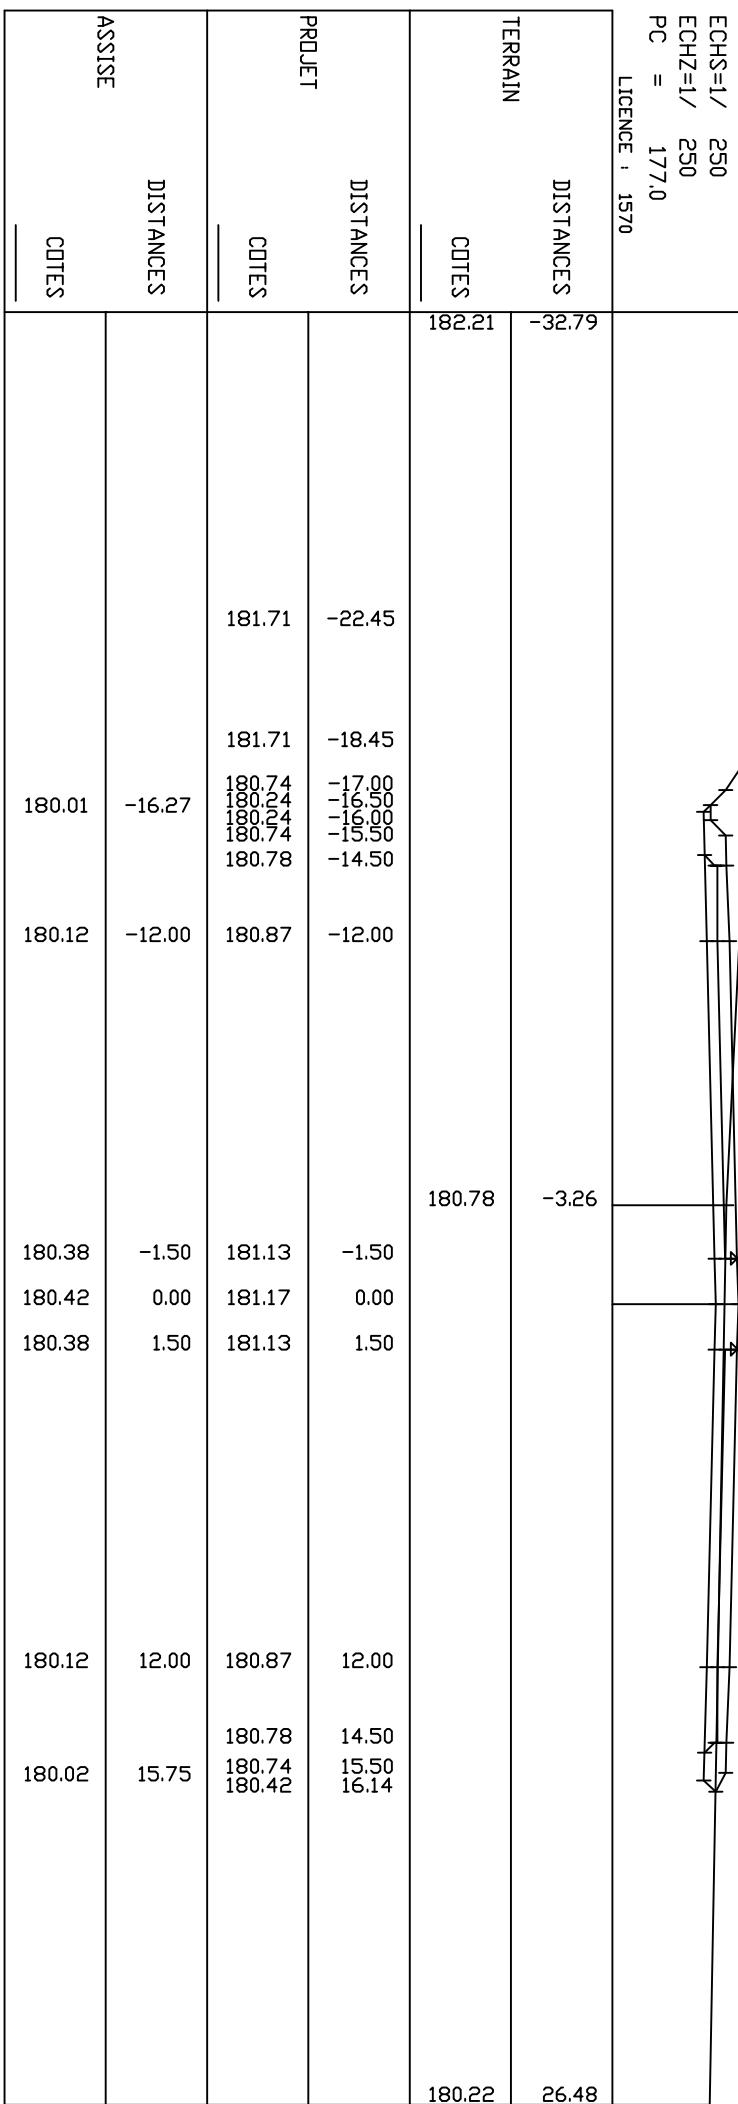


PROFIL 78

G2PIS

S = 1825.000
 ZTN = 181.411
 ZR0= 181.602

ECHS=1/
 ECHZ=1/
 PC = 177.0
 LICENCE , 1570

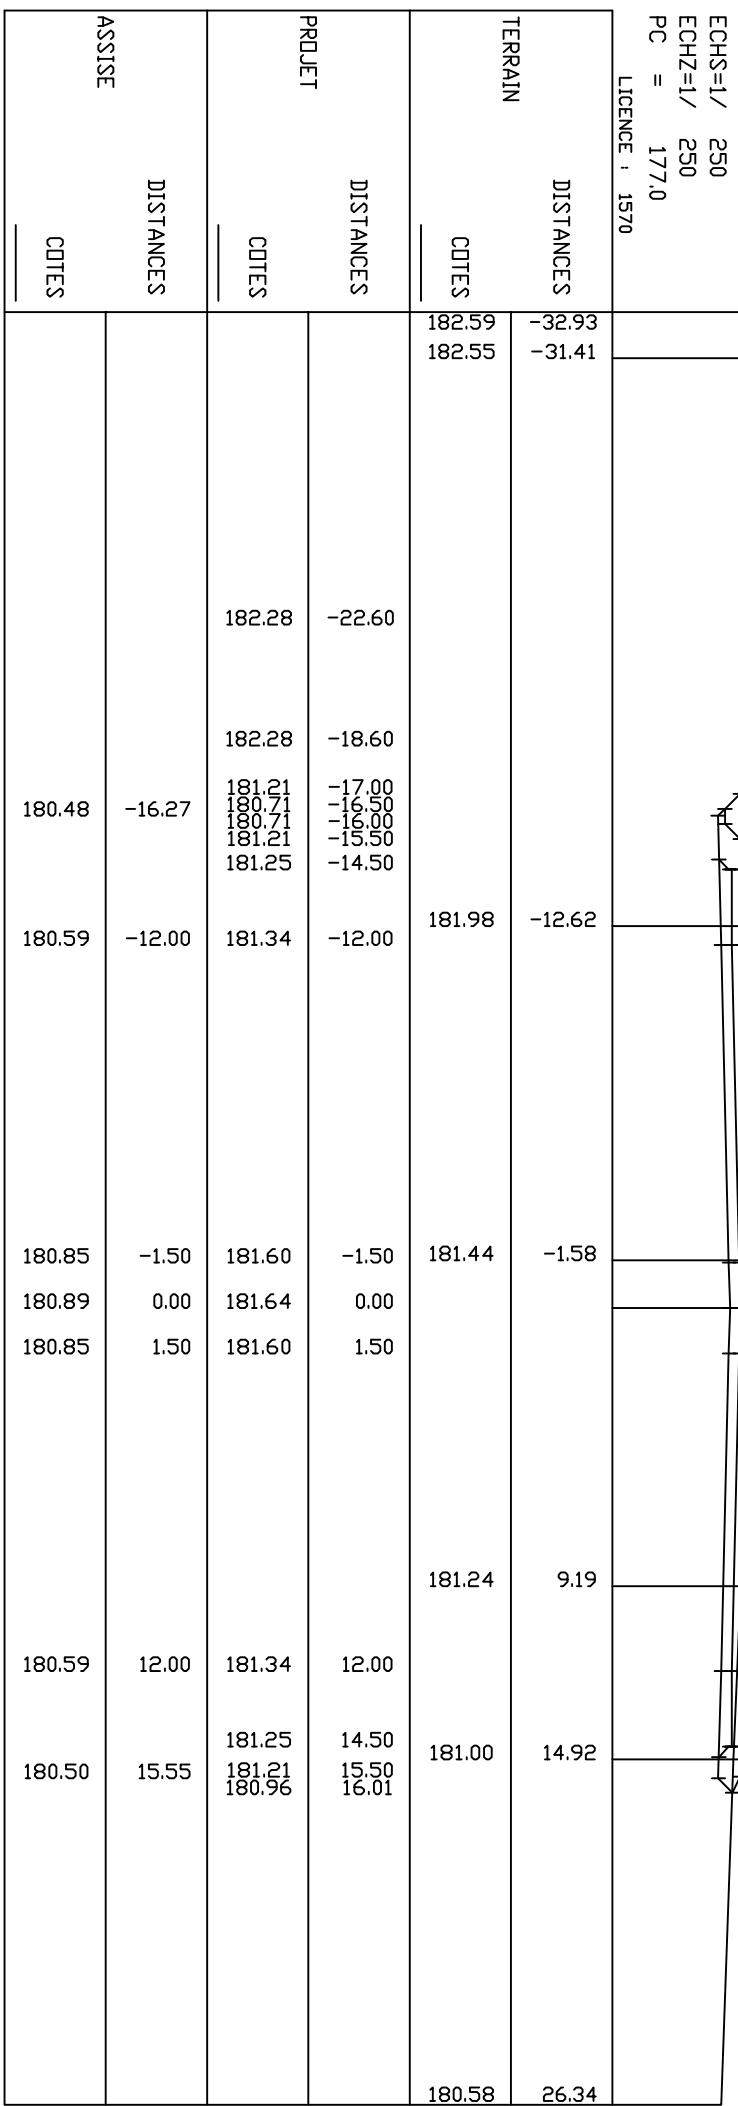

PROFIL 79

G2PIS

S = 1850.000
 ZTN = 181.832
 ZPRO= 182.128

ECH\$=1/
 ECHZ=1/
 PC = 178.0
 LICENCE , 1570

TERRAIN

DISTANCES

COTES

182.62 -32.35

DISTANCES

COTES

182.32 -20.58

DISTANCES

COTES

182.05 -5.95

DISTANCES

COTES

181.73 2.79

DISTANCES

COTES

181.30 14.89

DISTANCES

COTES


180.86 26.92


ASSISE	DISTANCES	COTES		
			PROJECT	DISTANCES COTES
181.01	-16.27	182.35	182.35	-21.92
		181.74	181.74	-17.92
		181.24	181.24	-17.00
		181.24	181.24	-16.50
		181.74	181.74	-16.50
		181.78	181.78	-15.50
				-14.50
181.12	-12.00	181.87	181.87	-12.00
181.38	-1.50	182.13	182.13	-1.50
181.42	0.00	182.17	182.17	0.00
181.38	1.50	182.13	182.13	1.50
181.12	12.00	181.87	181.87	12.00
181.01	16.25	181.78	181.30	14.50
		181.74		15.50
		181.24		16.49

PROFIL 80

S = 1875.000
ZTN = 182.054
ZPRO = 182.698


LICENCE : 1570

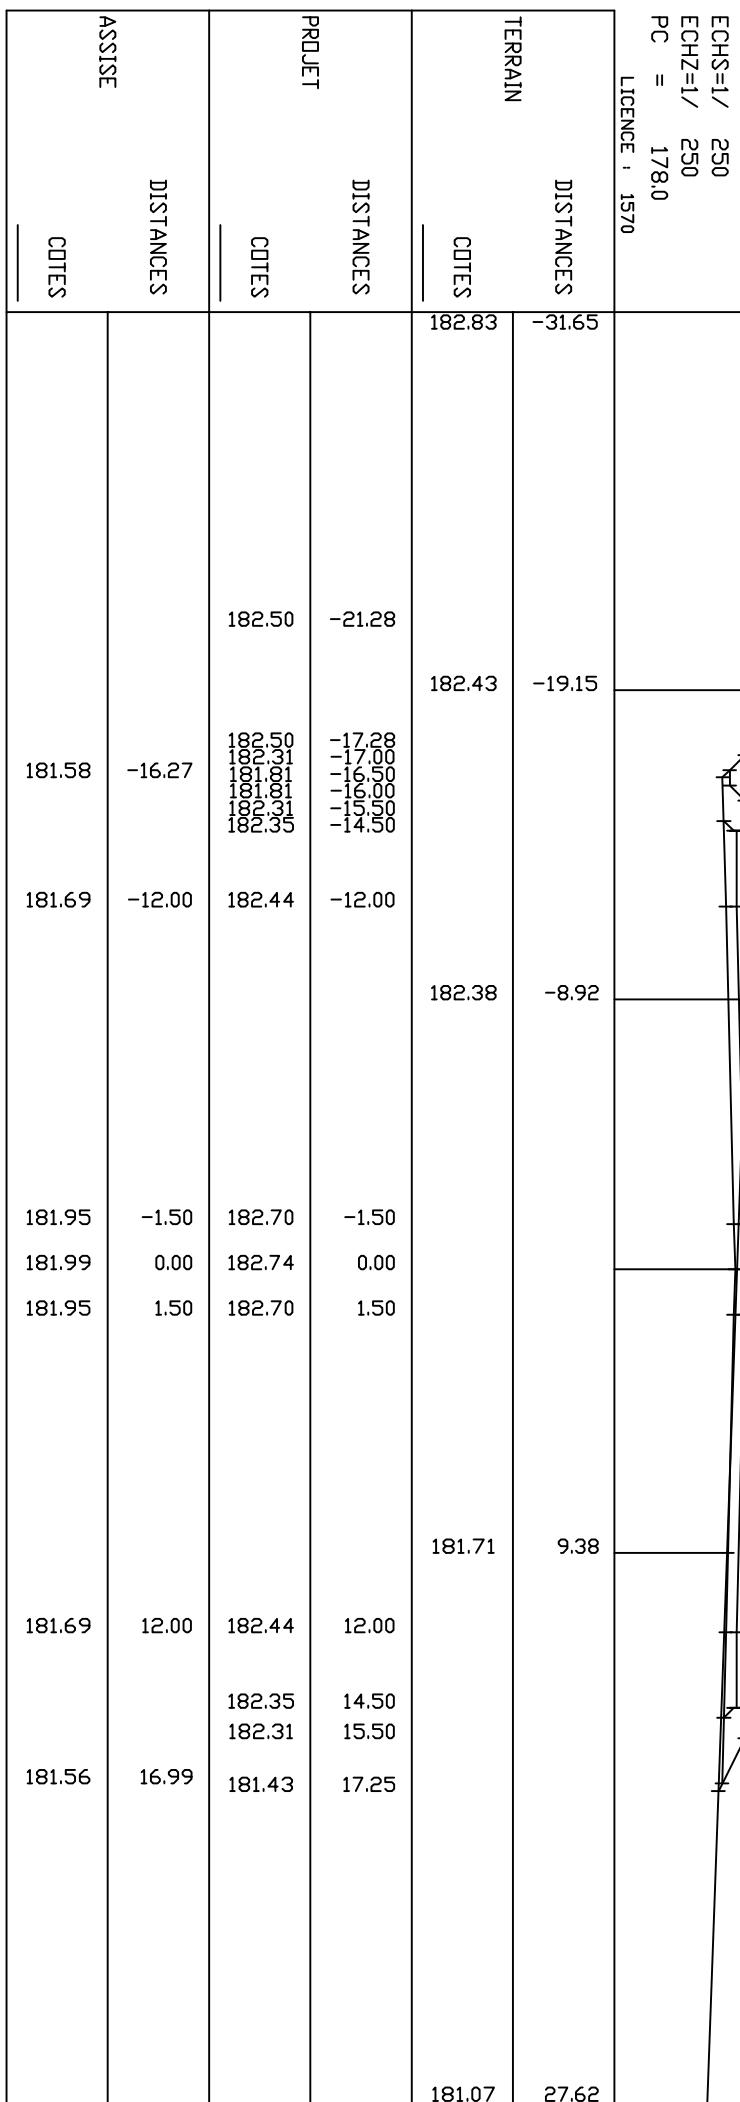

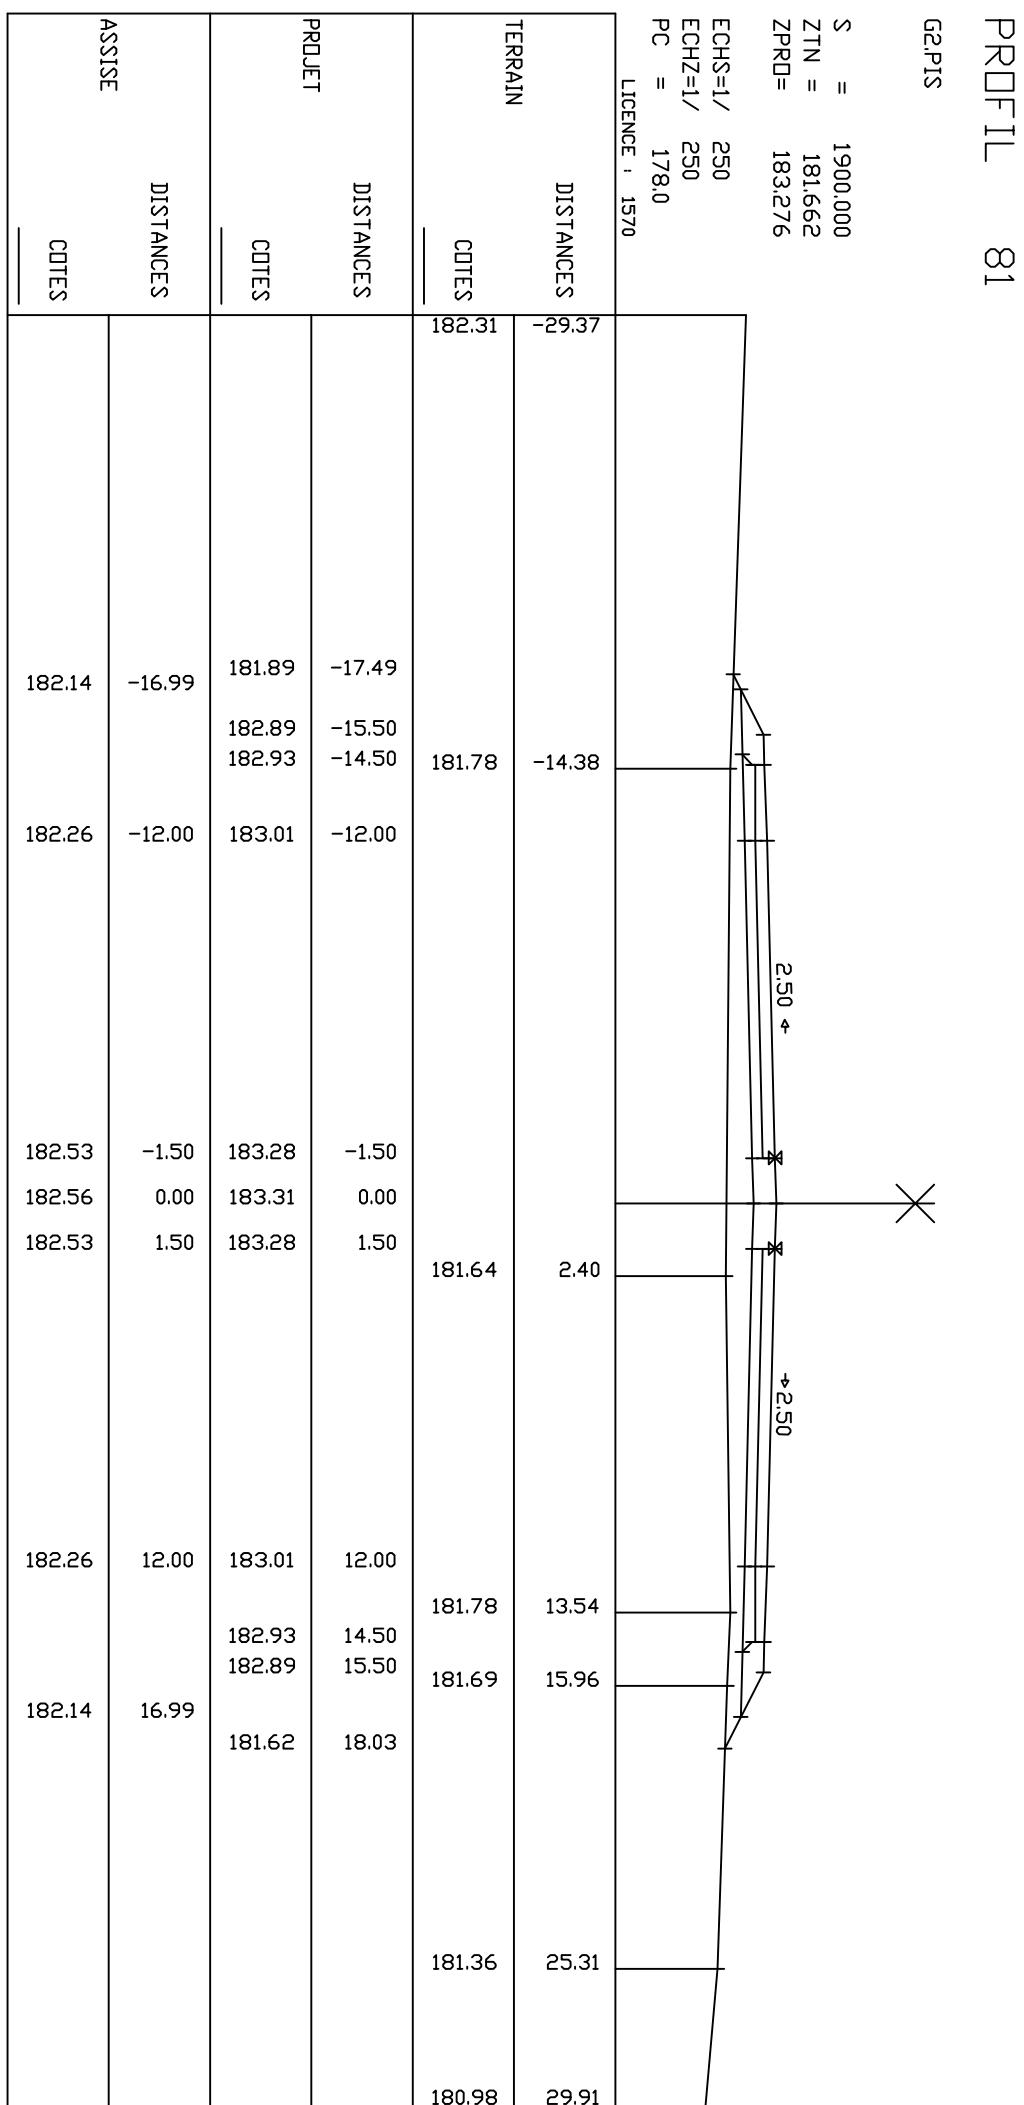

PROFIL 82


S = 1925.000
 ZTN = 181.718
 ZPRO = 183.855

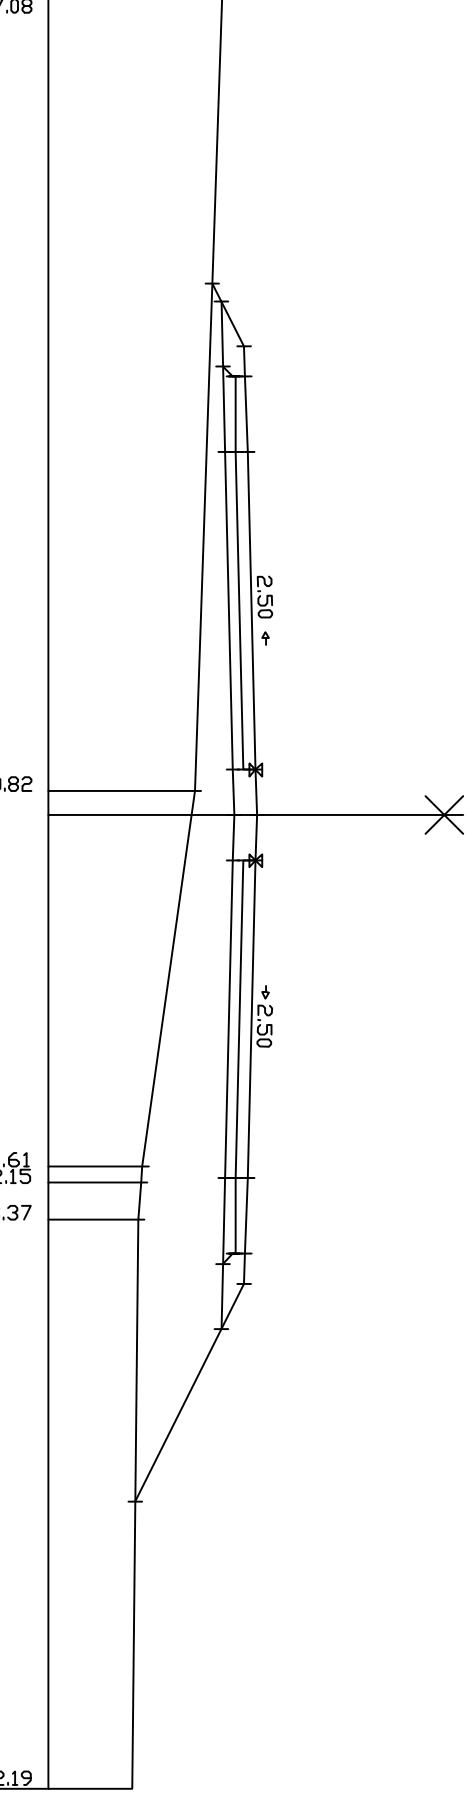

		DISTANCES		TERRAIN		PC = 177.0 LICENCE : 1570	
		COTES	DISTANCES	COTES	DISTANCES	COTES	
		PROJECT		COTES			
ASSISE	COTES						
182.72	-16.99	182.42	-17.59			182.75	-27.08
		183.46	-15.50				
		183.50	-14.50				
182.84	-12.00	183.59	-12.00				
183.10	-1.50	183.85	-1.50				
183.14	0.00	183.89	0.00			181.83	-0.82
183.10	1.50	183.85	1.50				
182.84	12.00	183.59	12.00	180.10	180.06	11.61	12.15
		183.50	14.50				
		183.46	15.50	179.96			
182.72	16.99						
		179.87	22.70				
						179.77	32.19

G2.PIS

S = 1950.000
ZTN = 181.542
ZPRO= 184.433

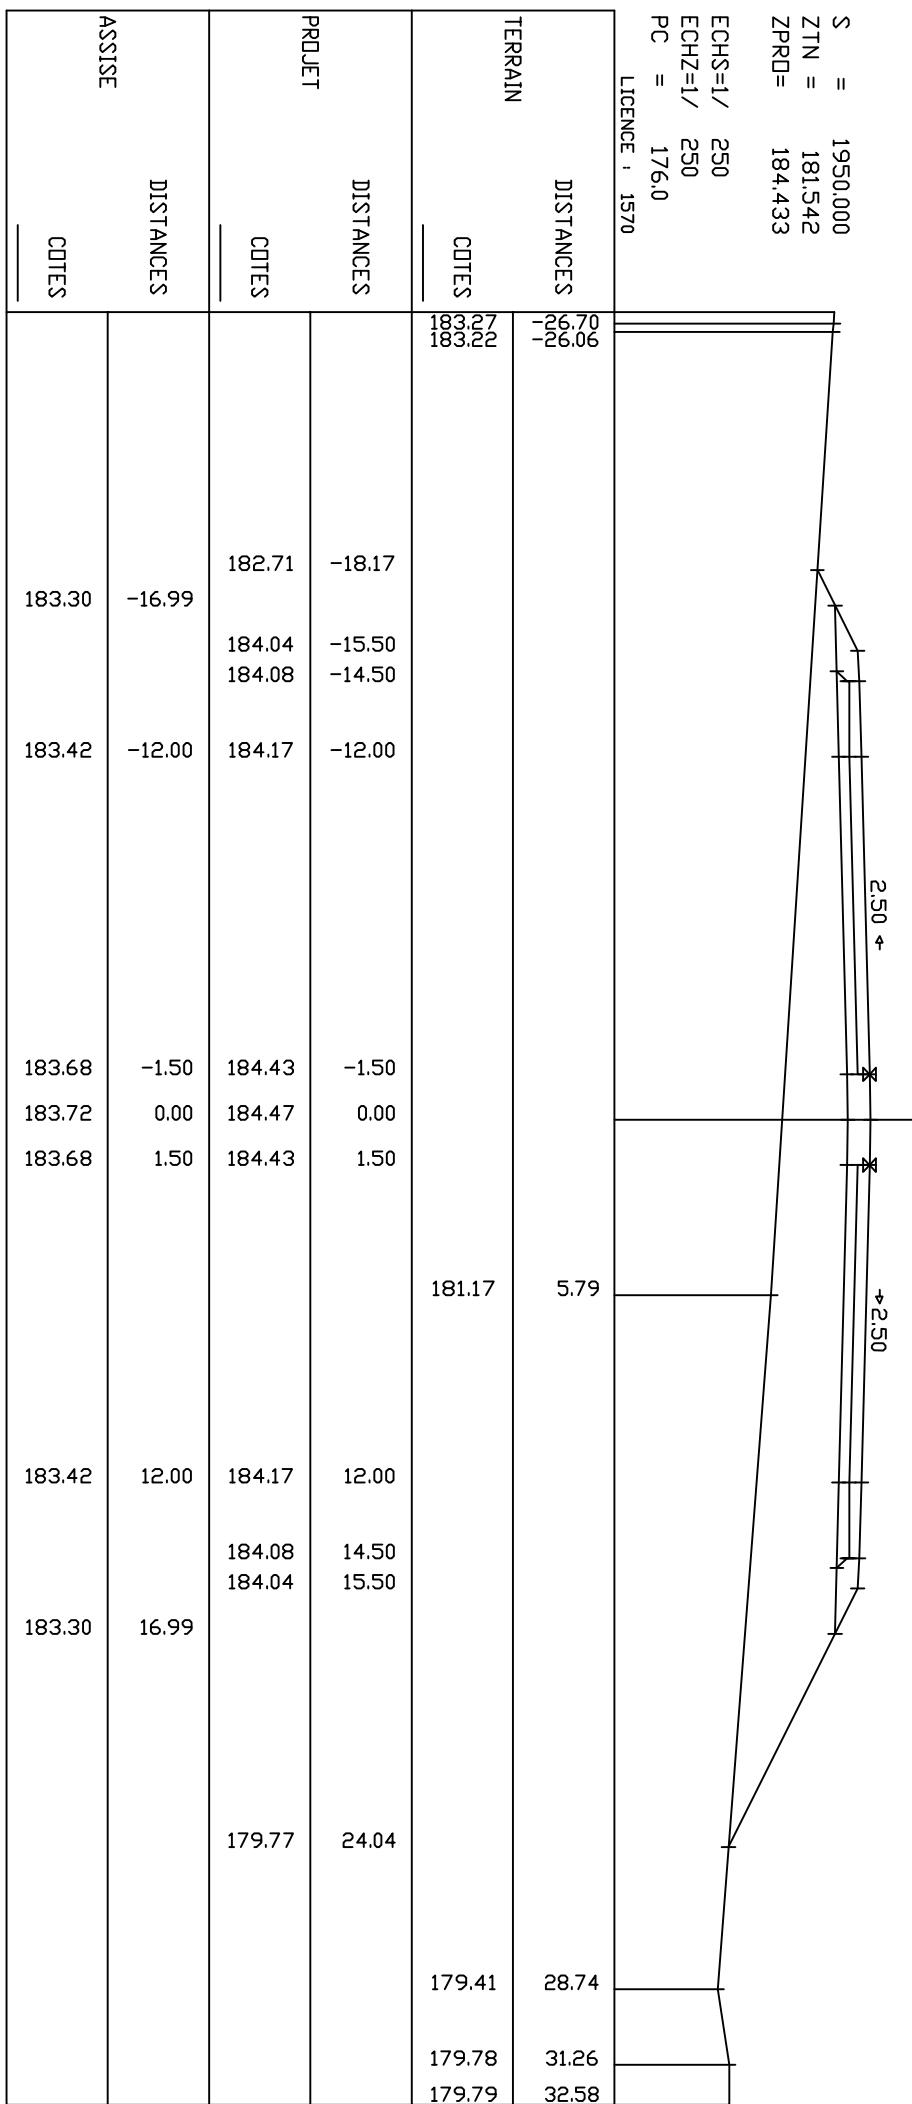


PROFIL 84


G2PIS

S = 1975.000
 ZTN = 182.417
 ZPRD= 185.012

ECHS=1/
 ECHZ=1/
 PC = 177.0
 LICENCE , 1570

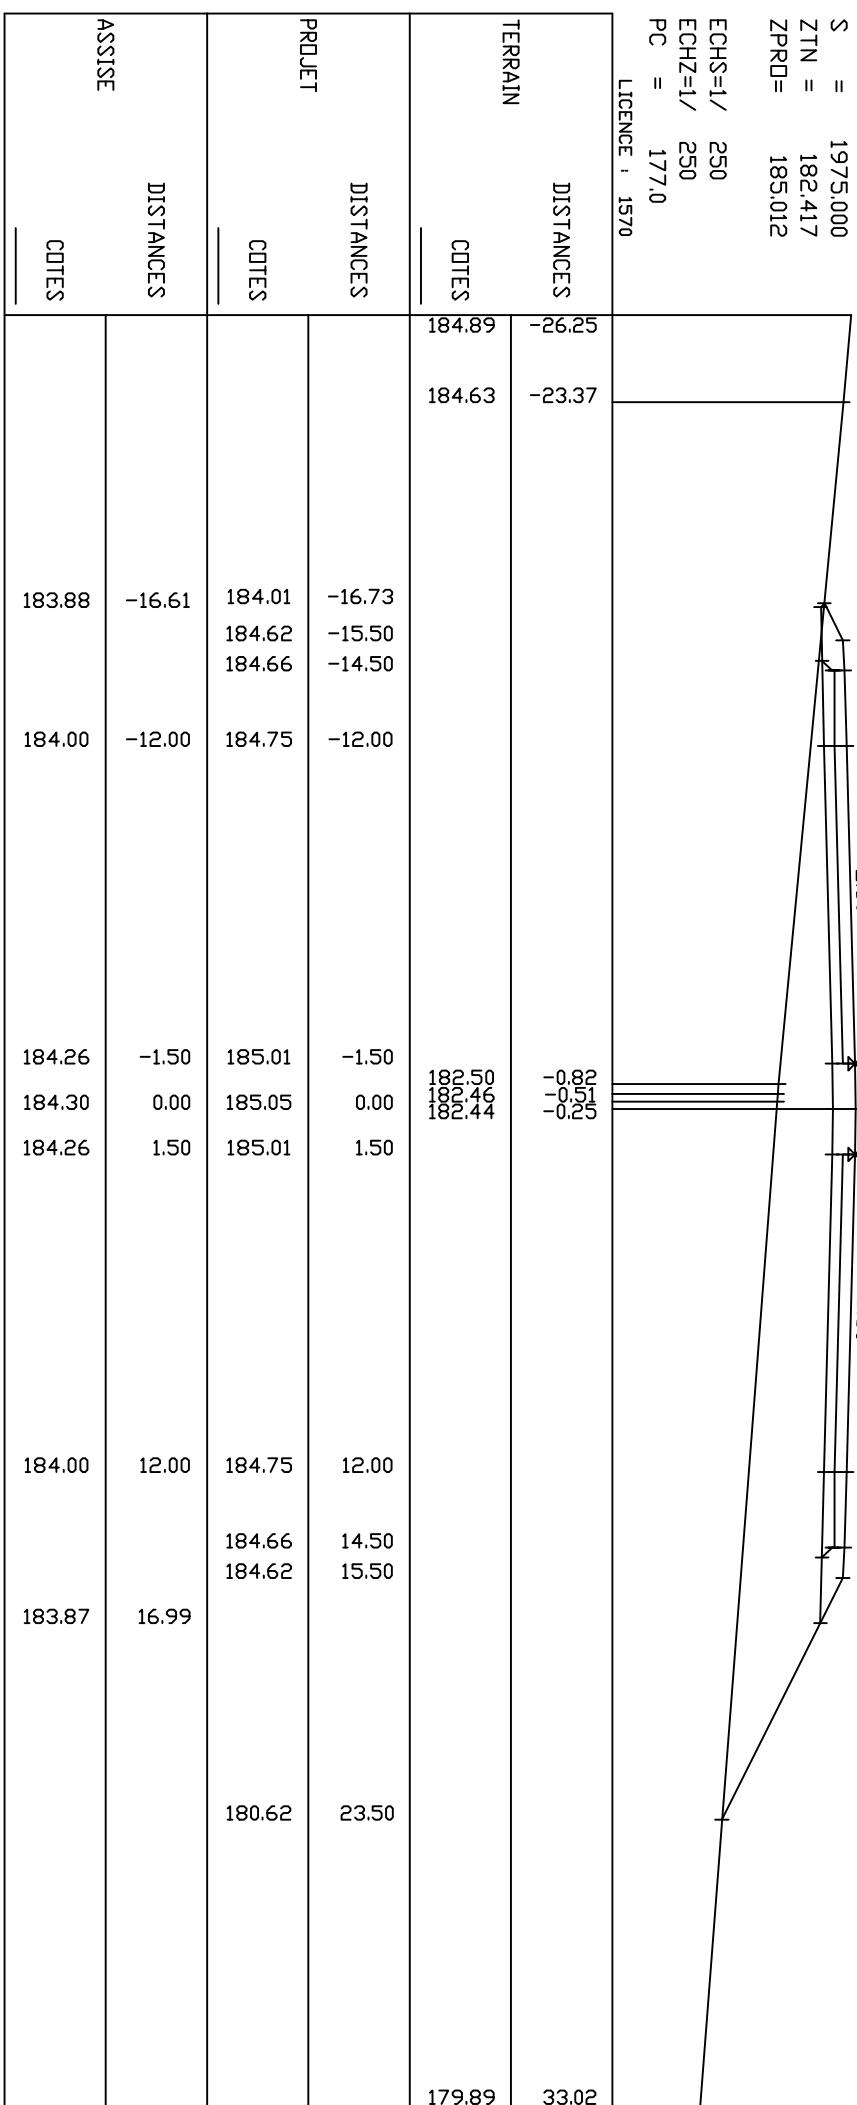

S	=	2000.000
ZTN	=	183.422
ZPRO	=	185.590

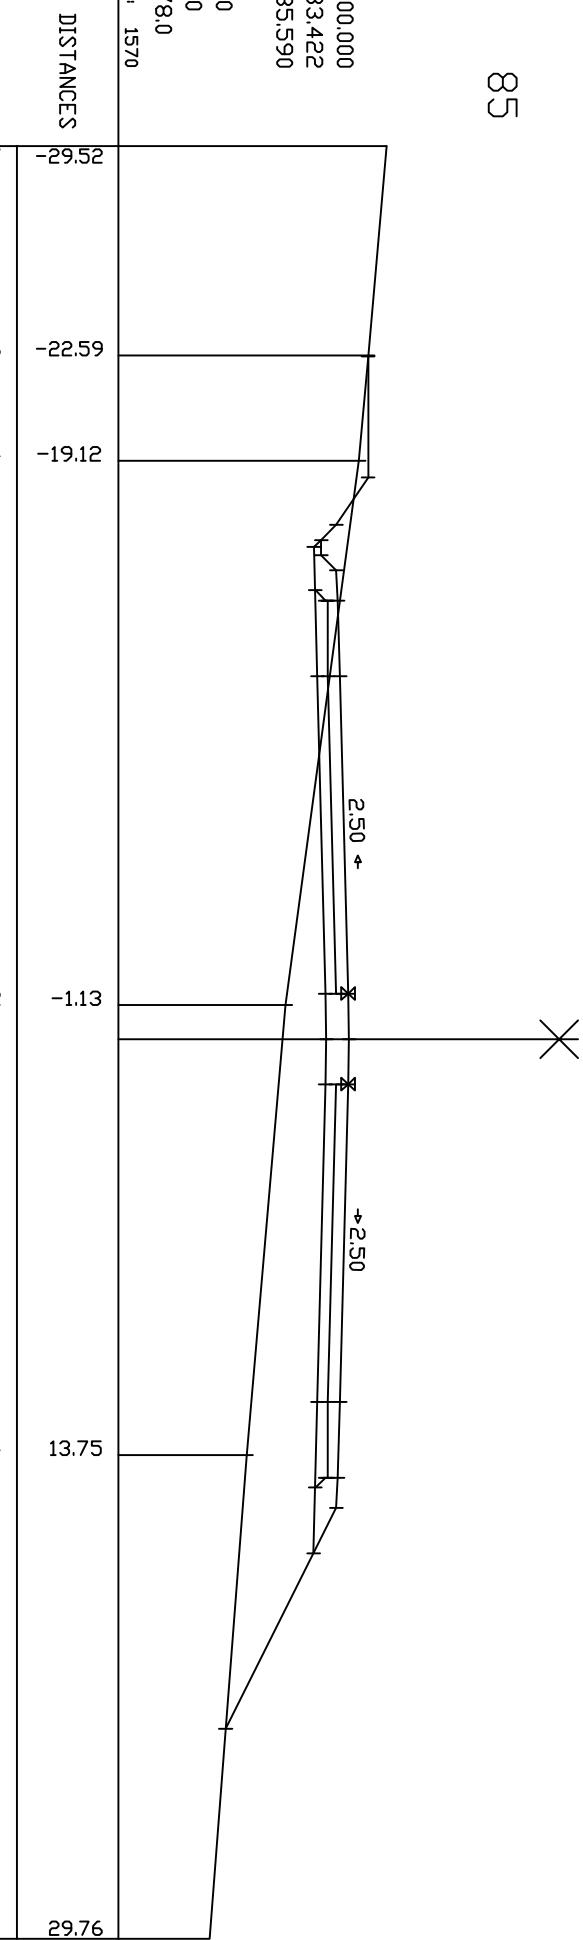


ASSISE	COTES	DISTANCES	COTES	DISTANCES	COTES	PROJECT
						186.82
						185.90
184.47	-16.27	186.26 185.20 184.70 184.70 185.20 185.24	186.26 -22.58 -18.58 -17.00 -16.50 -16.00 -15.50 -14.50			
184.58	-12.00	185.33		-12.00		
184.84	-1.50	185.59		-1.50		183.50
184.88	0.00	185.63		0.00		
184.84	1.50	185.59		1.50		
184.58	12.00	185.33		12.00		182.20
184.45	16.99	185.24 185.20		14.50 15.50		
		181.54		22.82		
						181.00

		PROFIL 86		G2PIS	
				S = 2025.000 ZTN = 184.433 ZPRO= 186.169	
				ECH\$=1/ ECHZ=1/ PC = 179.0 LICENCE , 1570	
		DISTANCES		DISTANCES	
TERRAIN		COTES		COTES	
PROJECT		DISTANCES		DISTANCES	
PROJET		COTES		COTES	
ASSISE		DISTANCES		DISTANCES	
COTES					
185.05	-16.27	187.61	-23.73	188.56	-30.65
185.16	-12.00	187.61	-19.73		
		185.78	-17.00		
		185.78	-16.00		
		185.78	-15.50		
		185.82	-14.50		
185.42	-1.50	186.17	-1.50	185.39	-7.59
185.46	0.00	186.21	0.00		
185.42	1.50	186.17	1.50	184.70	-2.89
				184.33	1.15
				184.33	
185.16	12.00	185.91	12.00	183.28	13.33
185.03	16.99	185.82	14.50		
		185.78	15.50		
		182.68	21.71	182.61	22.68
				182.03	27.74
				181.97	28.62

G2,PIS

S =
ZTN = 2050.000
ZPRO= 185.522
186.747

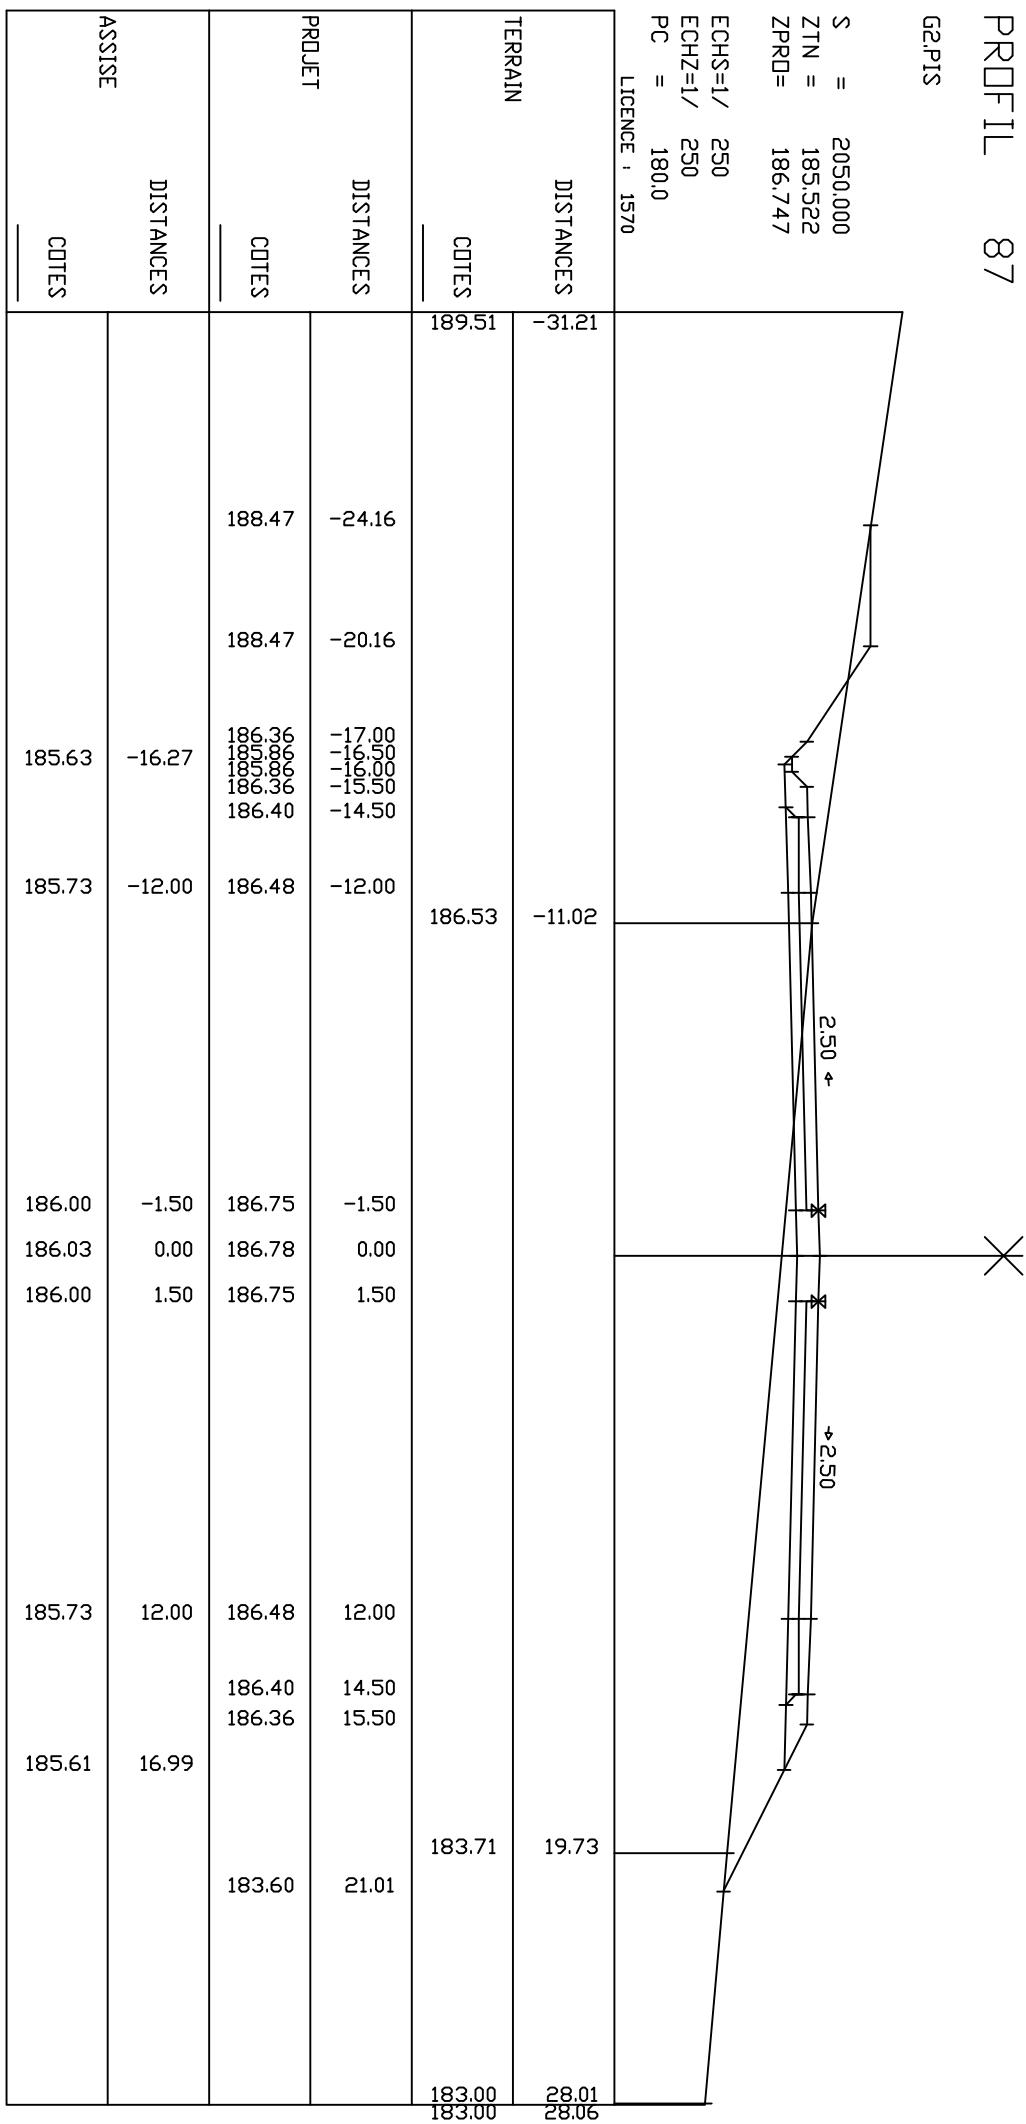

PROFIL 88

G2PIS

S = 2075.000
 ZTN = 186.526
 ZPRO= 187.326

ECHS=1/
 ECHZ=1/
 PC = 181.0
 LICENCE , 1570

TERRAIN

DISTANCES

COTES

189.18 -31.36

COTES

188.79 -28.01

COTES

188.70 -23.92

COTES

188.36 -20.45

COTES

188.25 -18.79

COTES

188.18 -18.11

COTES

188.03 -15.88

COTES

187.06 -12.00

COTES

187.33 -1.50

COTES

187.36 0.00

COTES

187.33 1.50

COTES

187.06 12.00

COTES

186.98 14.50

COTES

186.94 15.50


COTES

184.61 20.15

COTES


183.87 27.92

ASSISE	DISTANCES	DISTANCES		DISTANCES	DISTANCES
		COTES	COTES		
186.21	-16.27	186.94 186.44 186.44 186.94 186.98	-17.00 -16.50 -16.00 -15.50 -14.50	188.67 188.67 188.67 188.67 188.67	-23.59 -19.59 -17.00 -16.50 -16.00
186.31	-12.00	187.06	-12.00		
186.58	-1.50	187.33	-1.50		
186.61	0.00	187.36	0.00		
186.58	1.50	187.33	1.50		
186.31	12.00	187.06	12.00		
186.19	16.99	186.98 186.94 184.61	14.50 15.50 20.15		

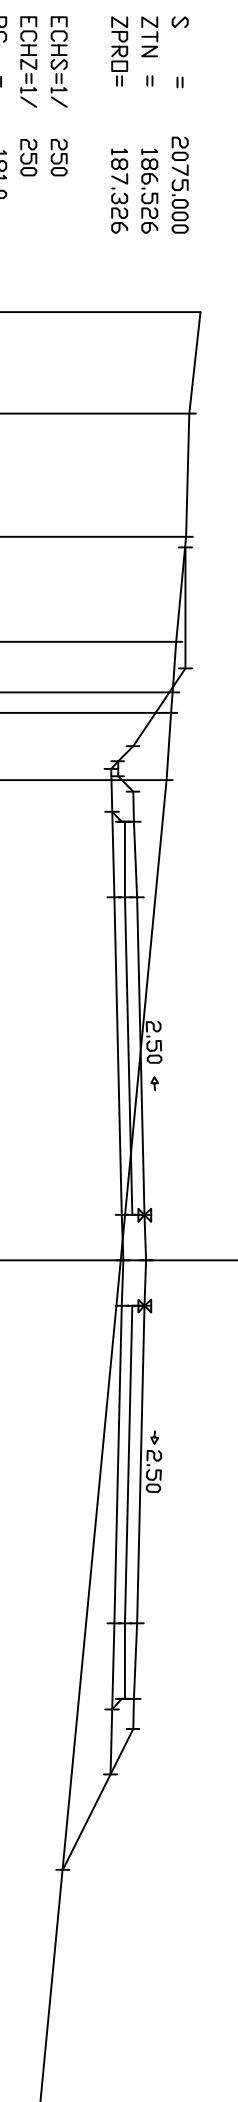

G2.PIS

S = 2100.000
 ZTN = 187.009
 ZPRO= 187.901
 ECHS=1/ 250
 ECHZ=1/ 250
 PC = 182.0
 LICENCE , 1570

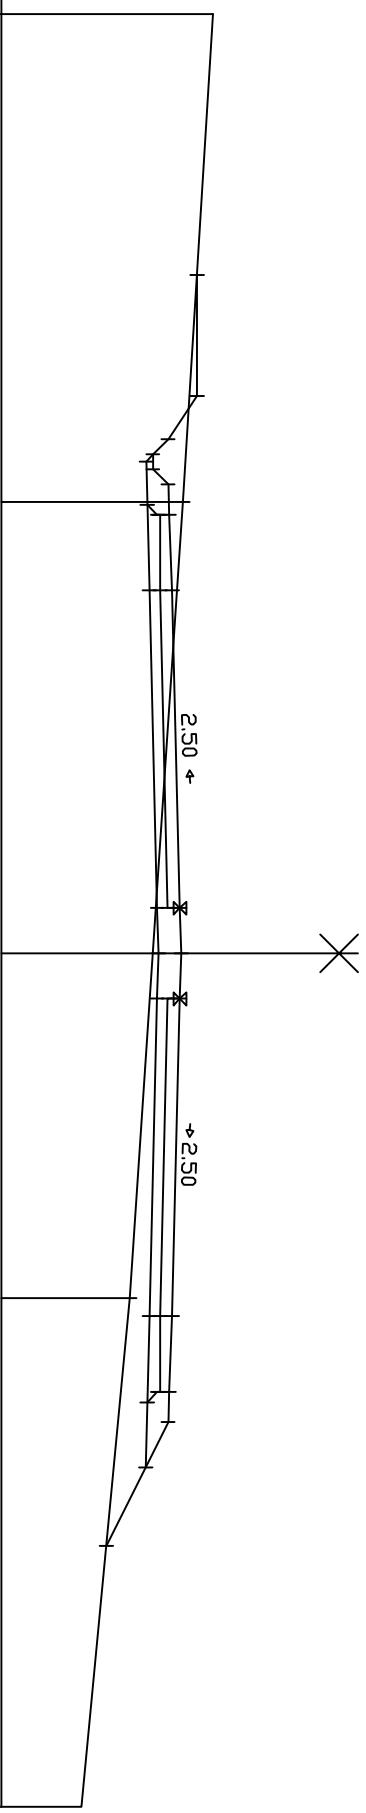

PROFIL 90

G2PIS

S = 2125.000
 ZTN = 187.041
 ZPRO= 188.374

ECHS=1/
 ECHZ=1/
 PC = 182.0
 LICENCE , 1570

TERRAIN

DISTANCES

COTES

189.13 -30.44

188.67 -25.47

188.44 -21.67

187.82 -11.76

187.37 -1.50

188.41 0.00

188.37 1.50

188.11 12.00

188.02 14.50

187.98 15.50

185.70 20.06


185.12 28.83

ASSISE	DISTANCES	DISTANCES	
		COTES	COTES
187.25	-16.27	188.44 187.98 187.48 187.48 187.98 188.02	-17.67 -17.00 -16.50 -16.50 -15.50 -14.50
187.36	-12.00	188.11	-12.00
187.62	-1.50	188.37	-1.50
187.66	0.00	188.41	0.00
187.62	1.50	188.37	1.50
187.36	12.00	188.11	12.00
187.24	16.99	188.02 187.98 185.70	14.50 15.50 20.06

PROFIL 91

G2,PIS

\hat{S} = 2150.000
 ZTN = 187.061
 ZPRD = 188.699

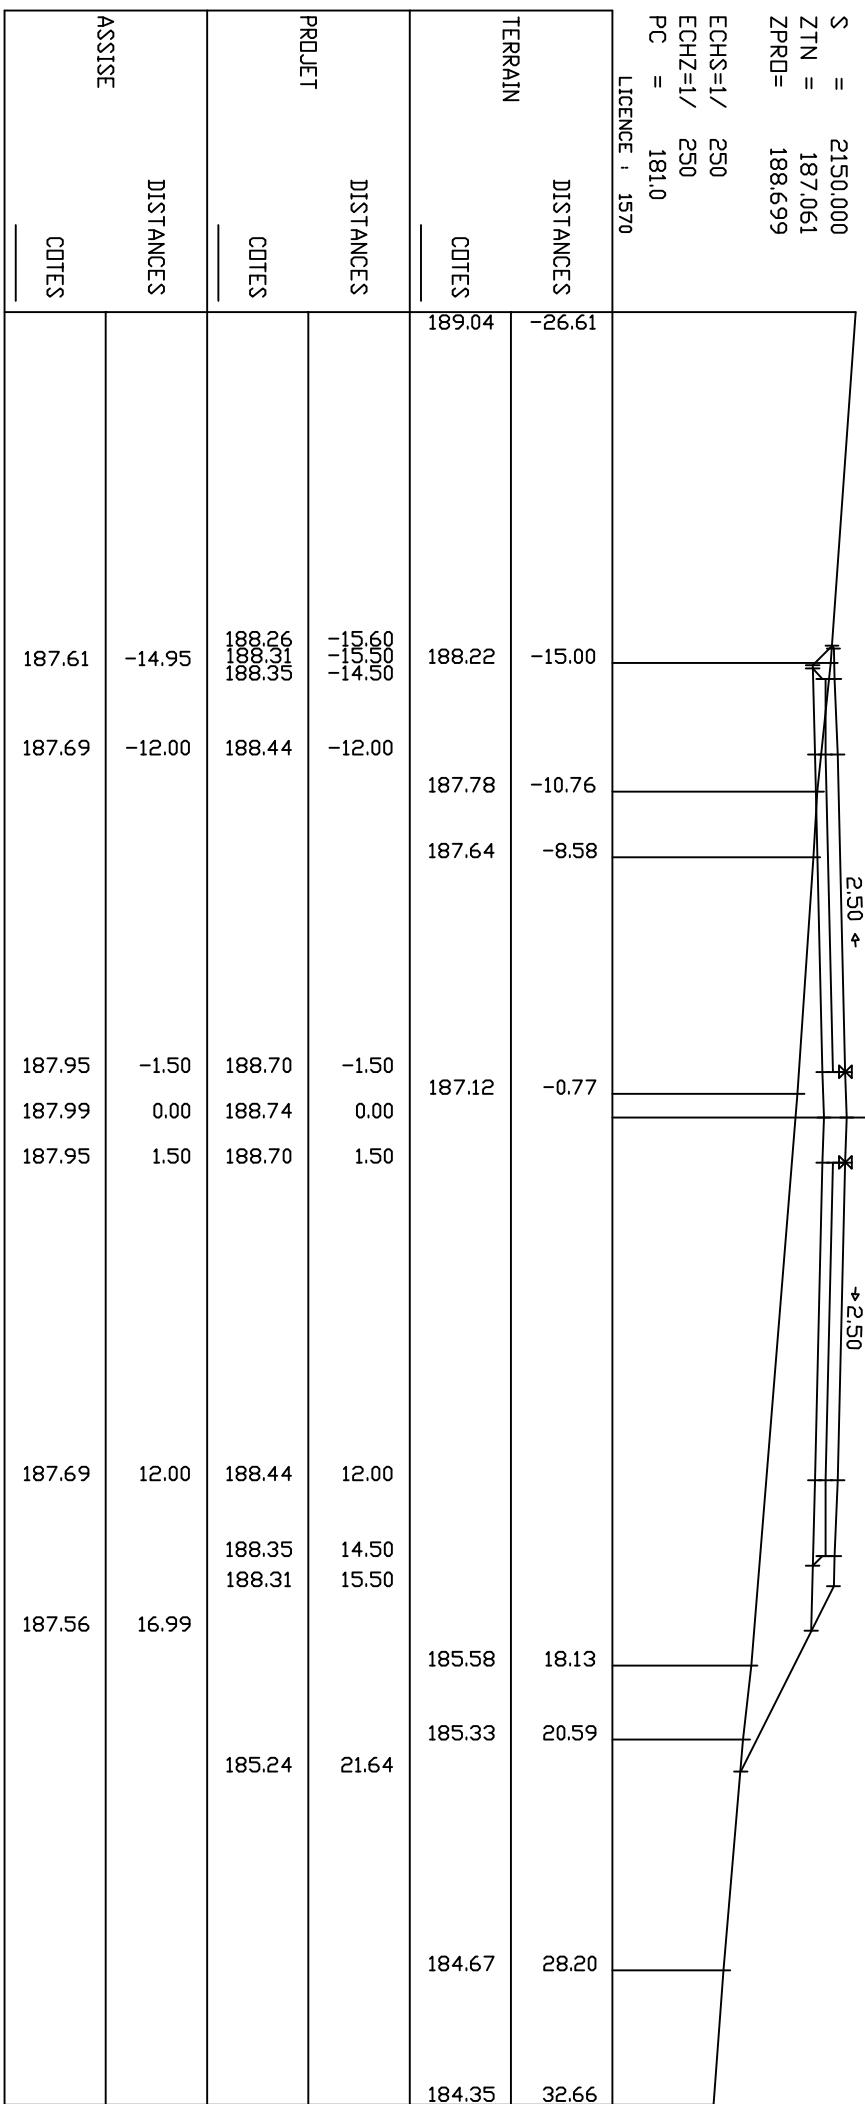


PROFIL 92

G2PIS

S = 2175.000
 ZTN = 188.347
 ZPRO= 188.875

ECHS=1/
 ECHZ=1/
 PC = 181.0
 LICENCE , 1570

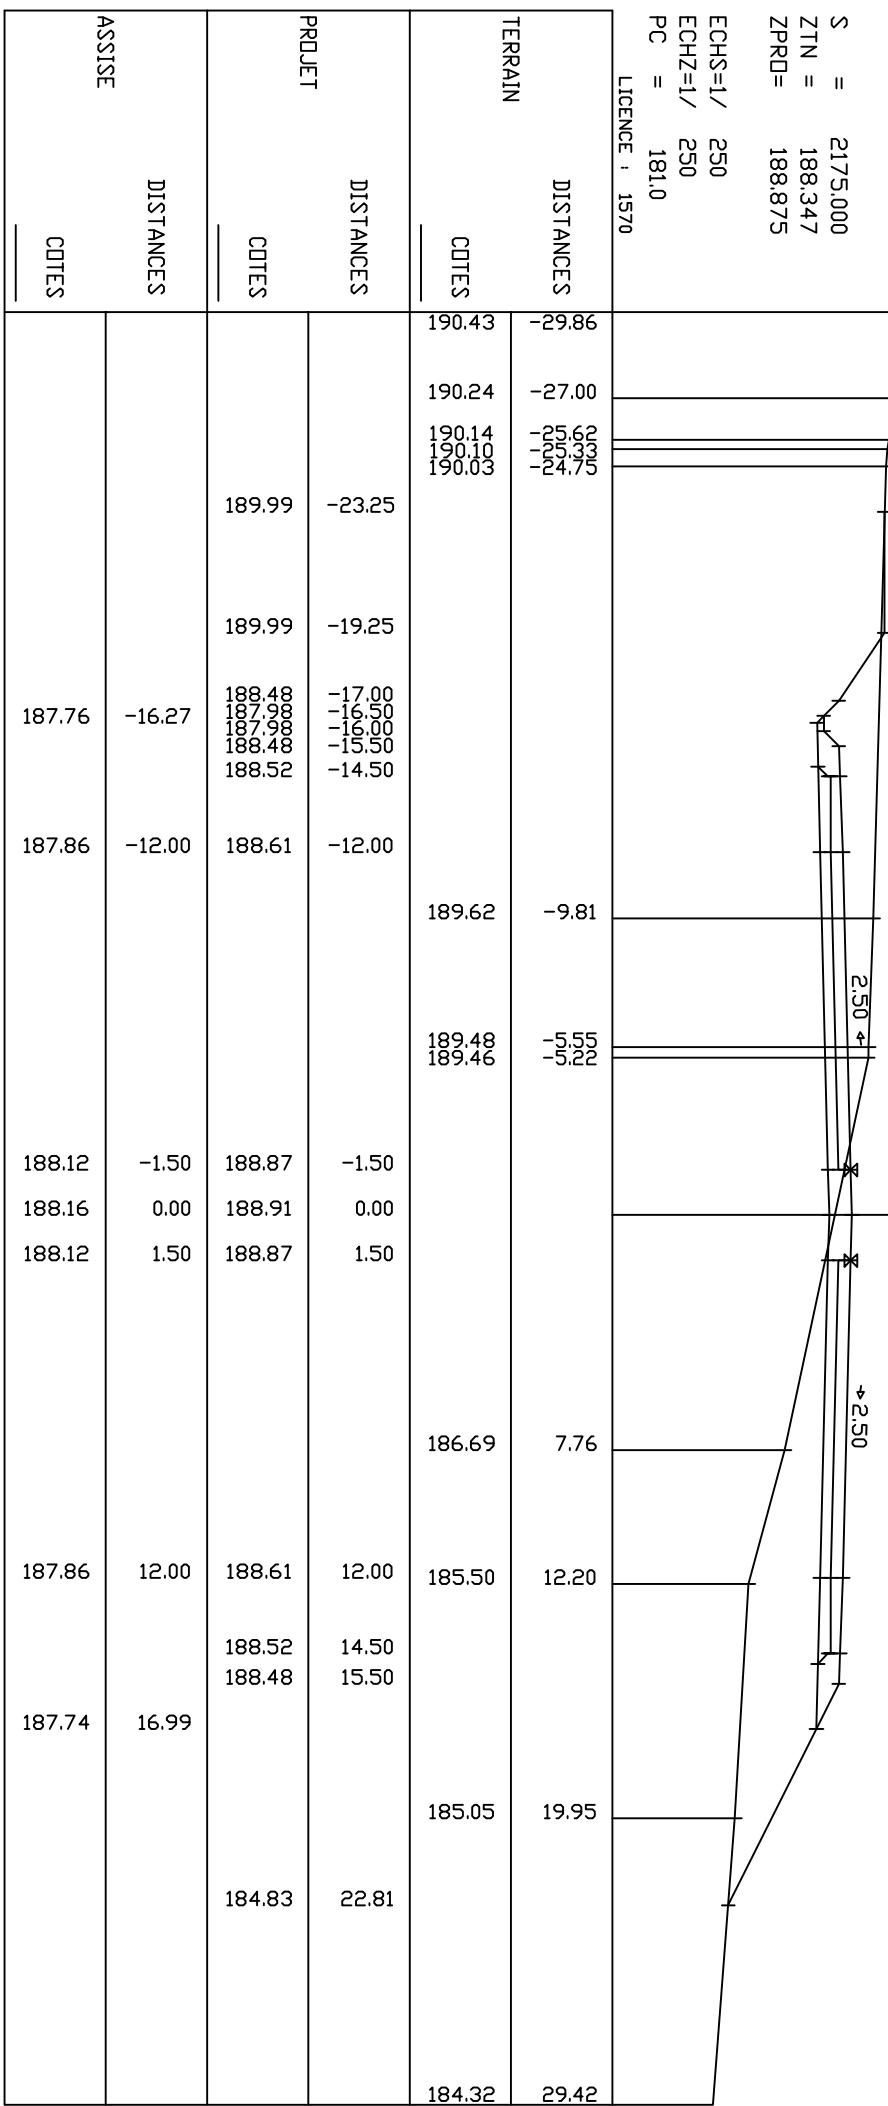


PROFIL 93

G2PIS

S = 2200.000
 ZTN = 187.225
 ZPRO= 188.901

ECHS=1/
 ECHZ=1/
 PC = 180.0
 LICENCE , 1570

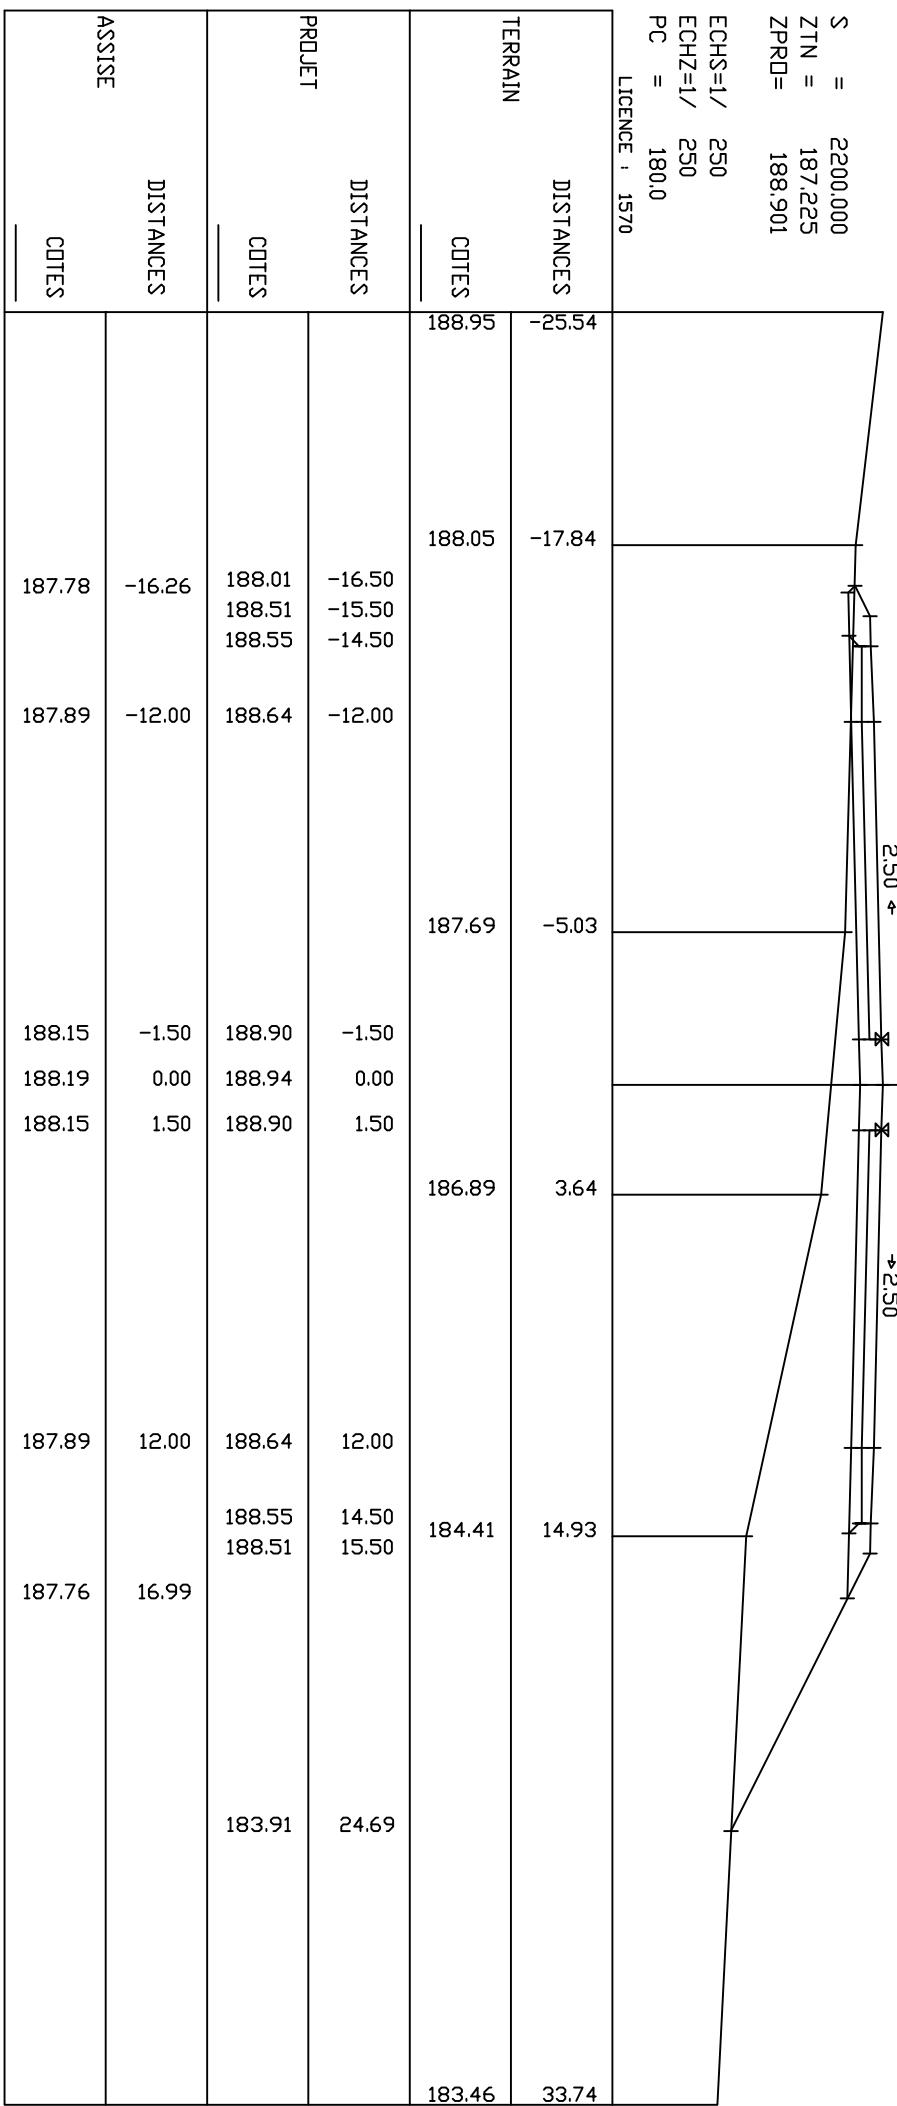


PROFIL 94

G2PIS

S = 2225.000
 ZTN = 185.456
 ZPRO= 188.827

ECHS=1/
 ECHZ=1/
 PC = 180.0
 LICENCE , 1570

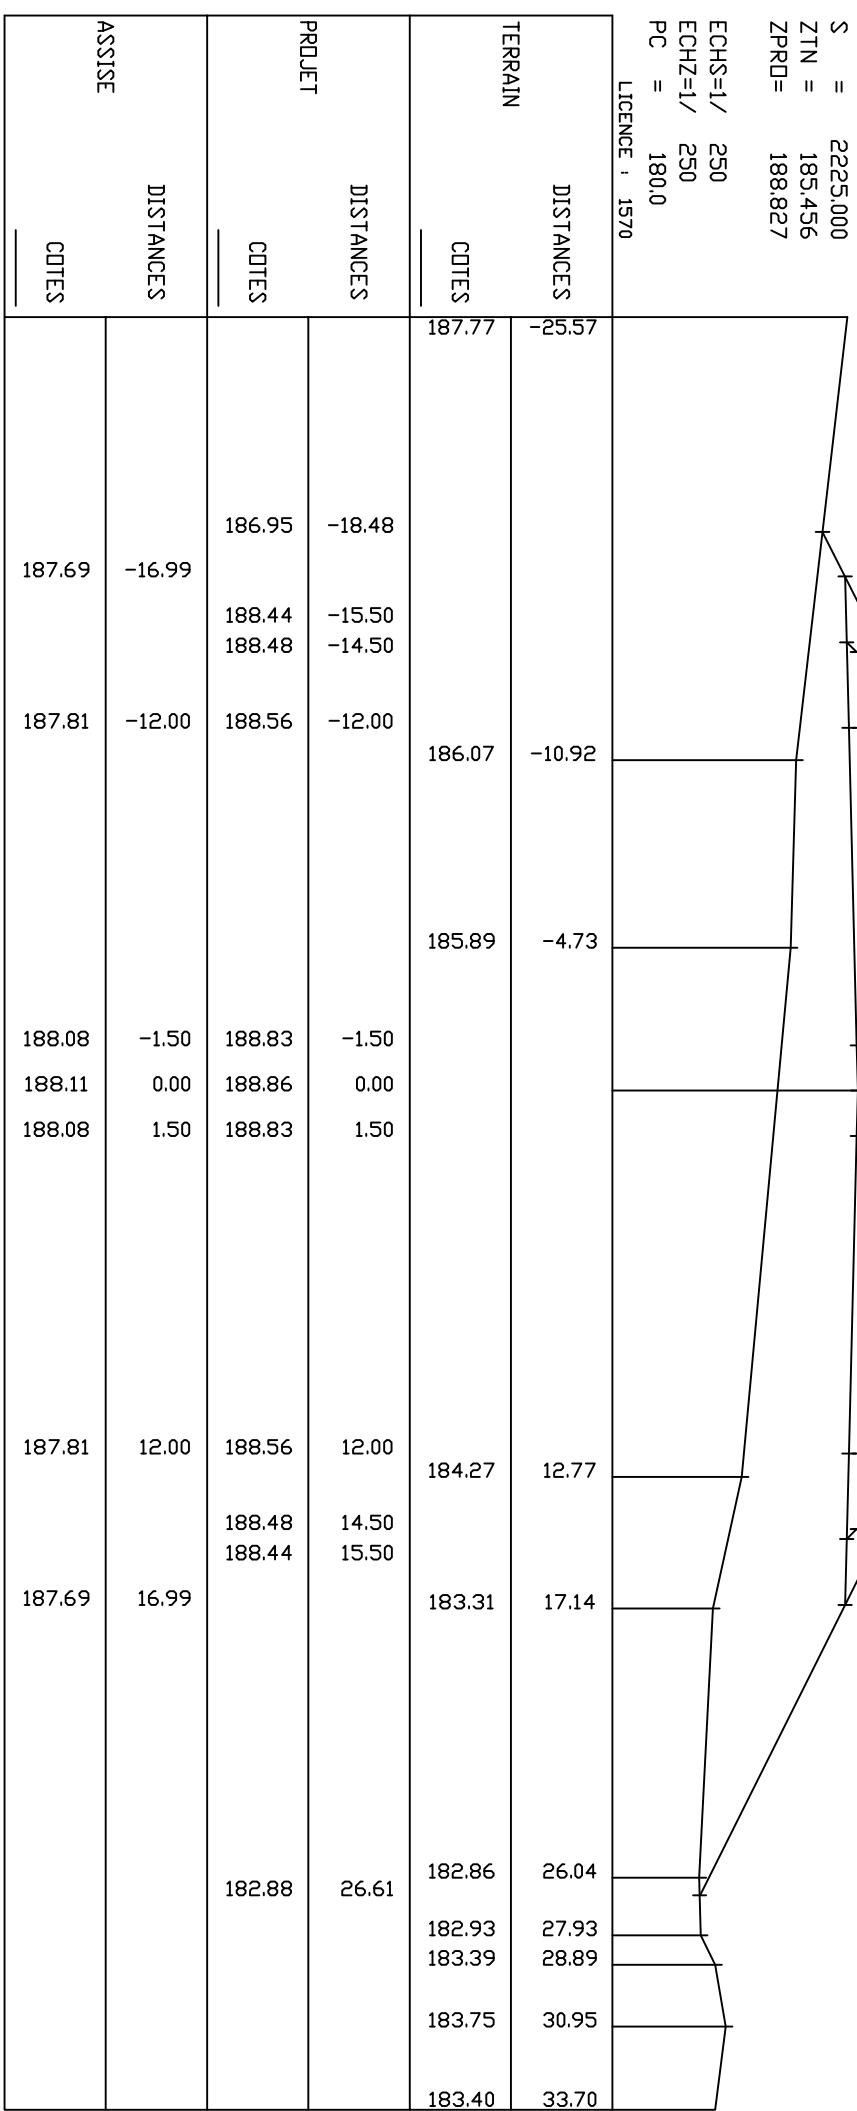


PROFIL 95

G2PIS

S = 2250.000
 ZTN = 184.061
 ZPRO= 188.748


ECHS=1/
 ECHZ=1/
 PC = 250
 LICENCE , 179.0
 1570

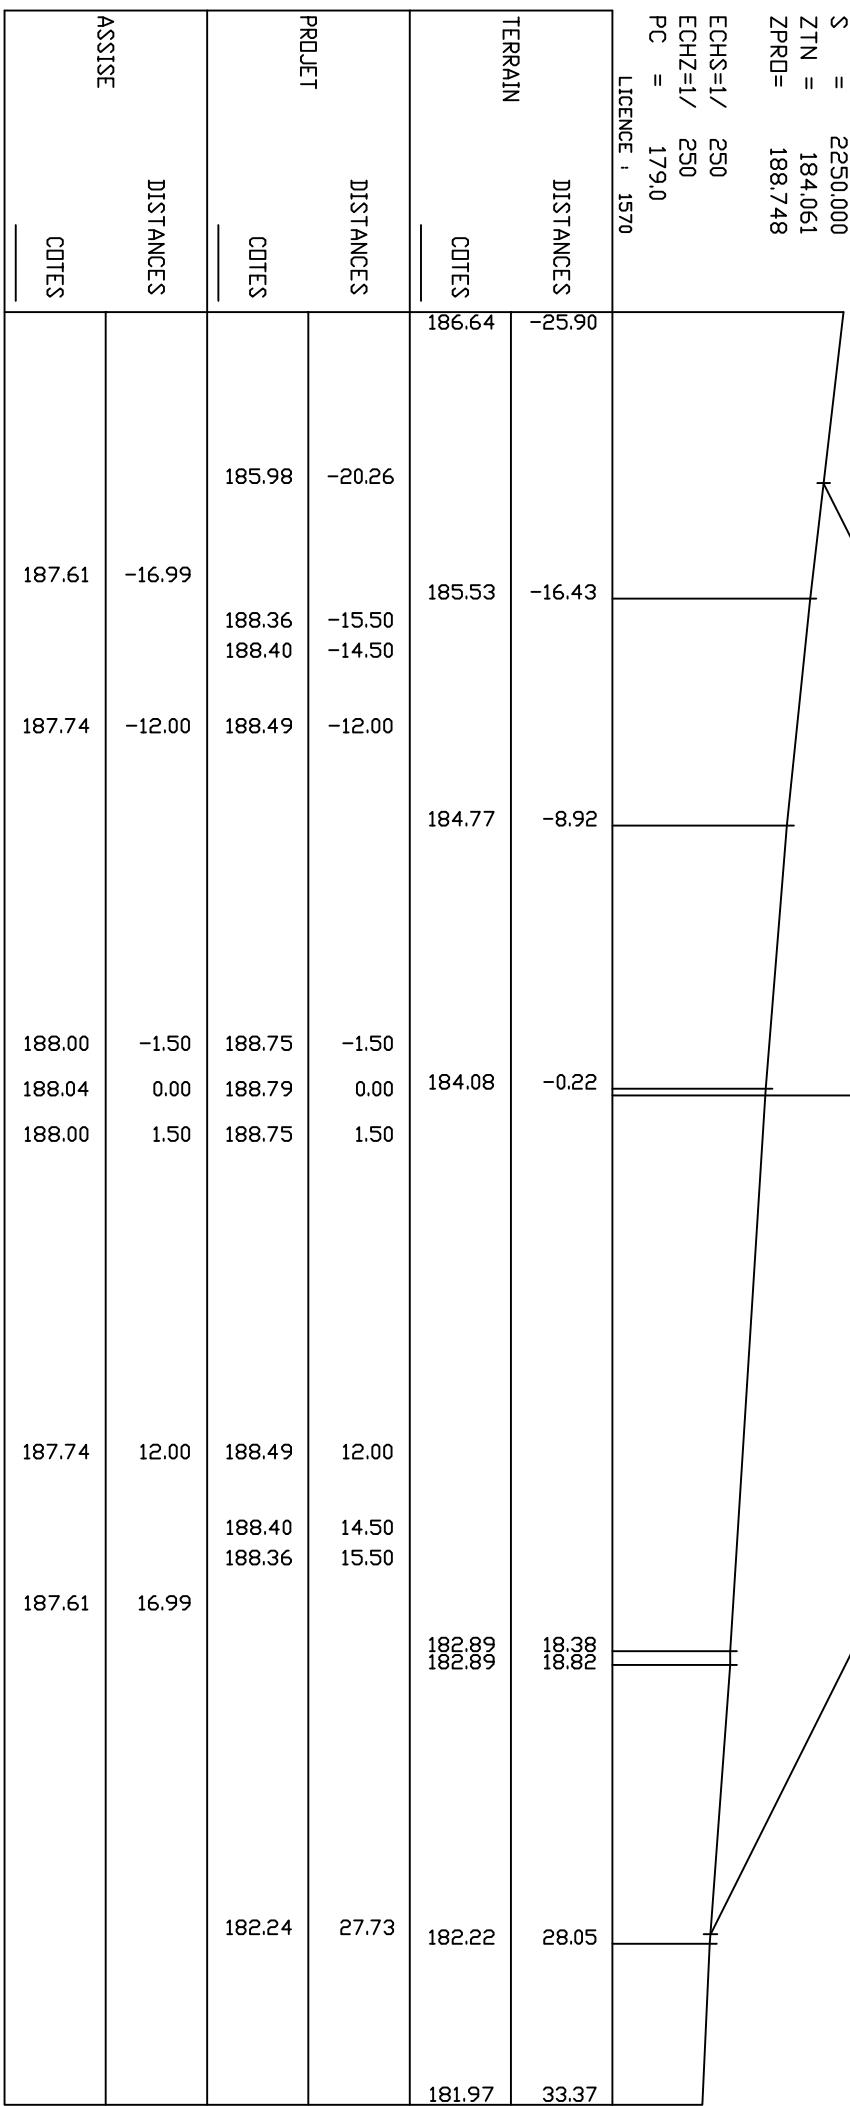

四

G2.PIS

S = 2275,000
ZTN = 185,499
ZPRO = 188,670

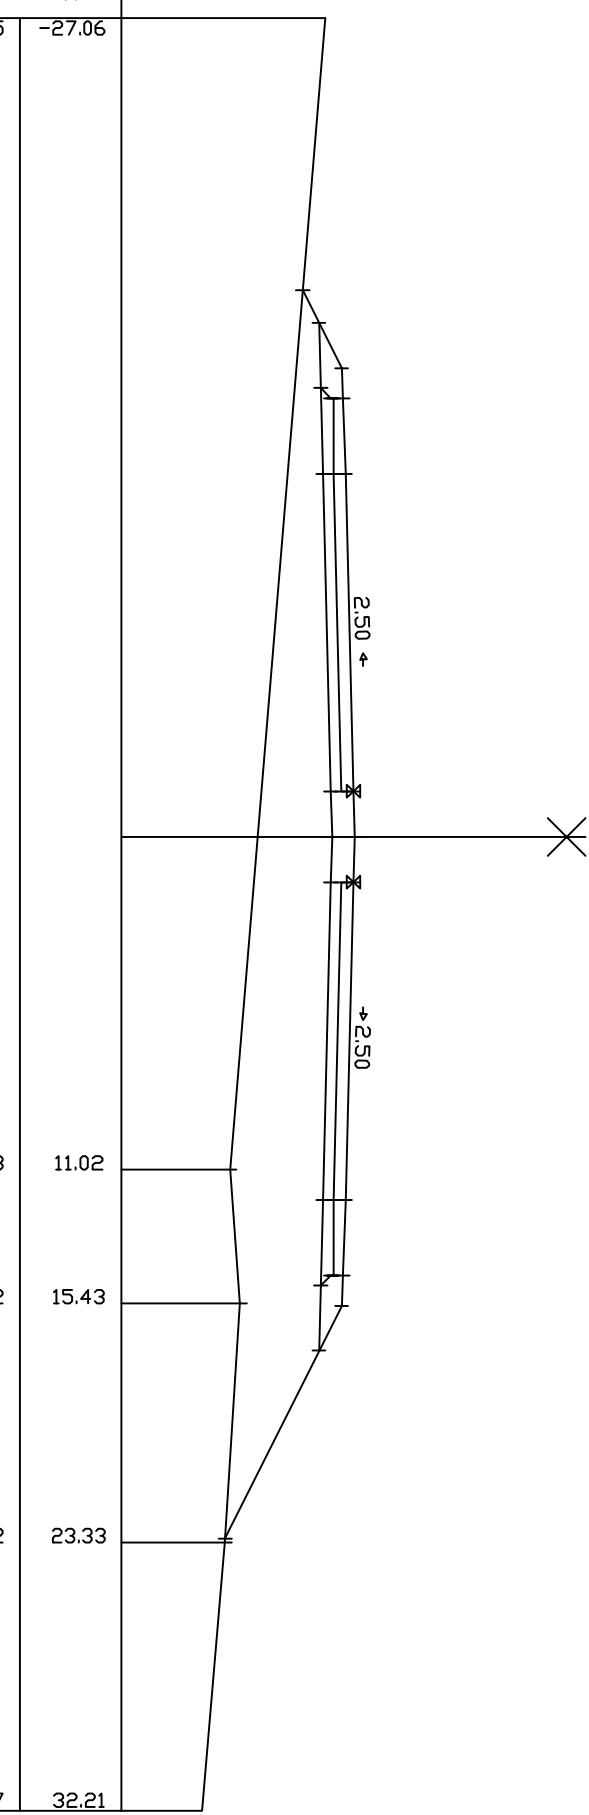

ASSISE COTES	DISTANCES COTES	DISTANCES		PROJET
		COTES	DISTANCES	
187.53	-16.99	187.00	-18.06	
		188.28	-15.50	
		188.32	-14.50	
187.66	-12.00	188.41	-12.00	
187.92	-1.50	188.67	-1.50	
187.96	0.00	188.71	0.00	
187.92	1.50	188.67	1.50	
187.66	12.00	188.41	12.00	
		188.32	14.50	
		188.28	15.50	
187.53	16.99	184.42	23.21	

PROFIL 97

G2PIS

S = 2300.000
 ZTN = 186.617
 ZPRO= 188.592

ECHS=1/
 ECHZ=1/
 PC = 182.0
 LICENCE , 1570

TERRAIN

DISTANCES

COTES

				188.51	-27.19
				188.25	-25.19

186.25

5.62

32.08

184.57

DISTANCES

COTES

PROJECT

DISTANCES

COTES

DISTANCES

COTES


ASSISE

187.47	-16.31	187.69	-16.53		
		188.20	-15.50		
		188.24	-14.50		
187.58	-12.00	188.33	-12.00		
187.84	-1.50	188.59	-1.50		
187.88	0.00	188.63	0.00		
187.84	1.50	188.59	1.50		
187.58	12.00	188.33	12.00		
		188.24	14.50		
		188.20	15.50		
187.45	16.99		21.41		
		185.25			

PROFIL 98

G2PIS


S = 2325.000
 ZTN = 187.318
 ZPRO= 188.514
 ECHS=1/
 ECHZ=1/
 PC = 183.0
 LICENCE , 1570

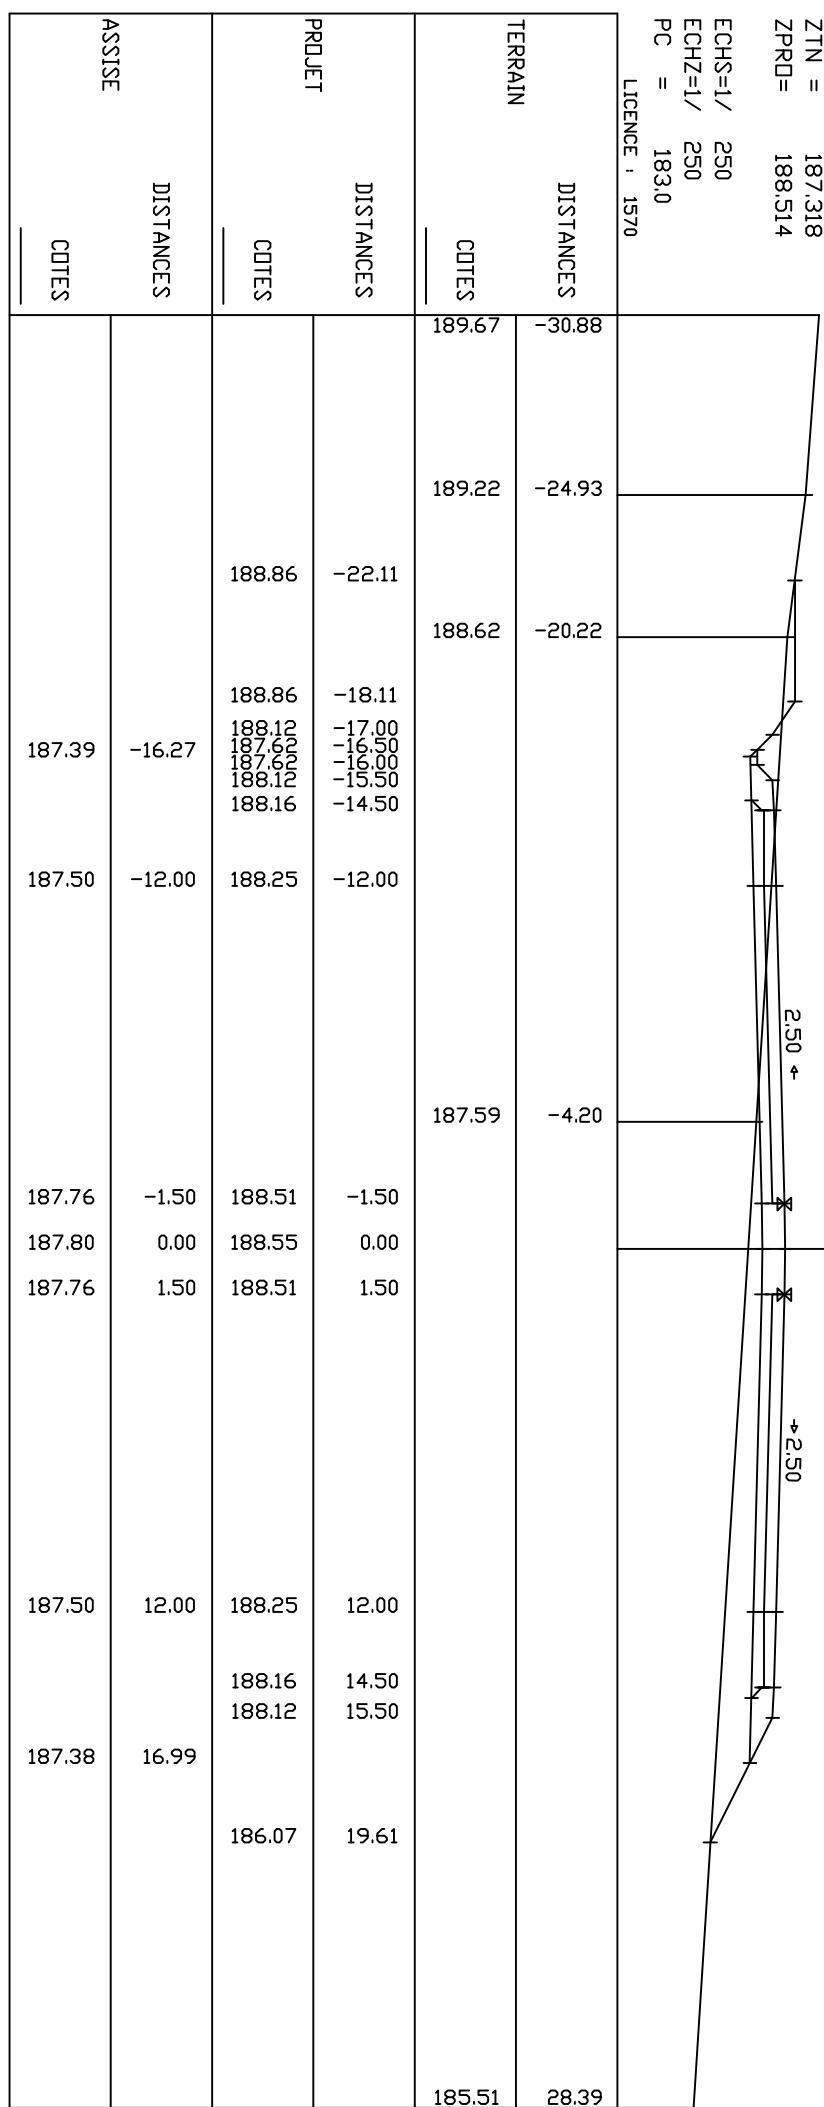

PROFIL 99

G2,PIS

S = 2350.000
 ZTN = 188.024
 ZPRO= 188.436
 ECHS=1/ 250
 ECHZ=1/ 250
 PC = 183.0
 LICENCE : 1570

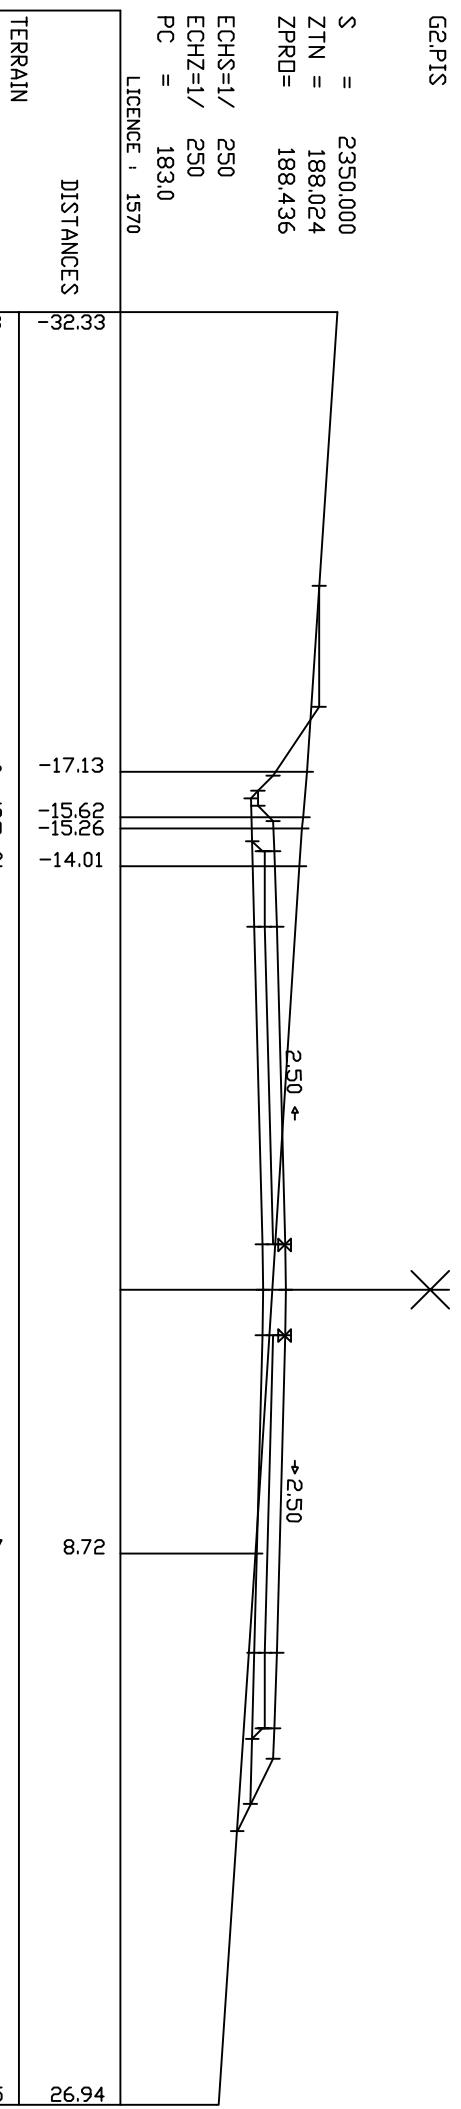

PROFIL 100

G2PIS

S = 2375.000
 ZTN = 187.592
 ZPRO= 188.358

ECHS=1/
 ECHZ=1/
 PC = 183.0
 LICENCE , 1570

TERRAIN

DISTANCES

COTES

190.13 -31.84

COTES

188.84 -14.25

COTES

187.45 1.67

COTES

185.69 27.43


COTES

PROFIL 101

G2PIS

S = 2400.000
 ZTN = 187.537
 ZPRO= 188.280

ECHS=1/
 ECHZ=1/
 PC = 182.0
 LICENCE , 1570

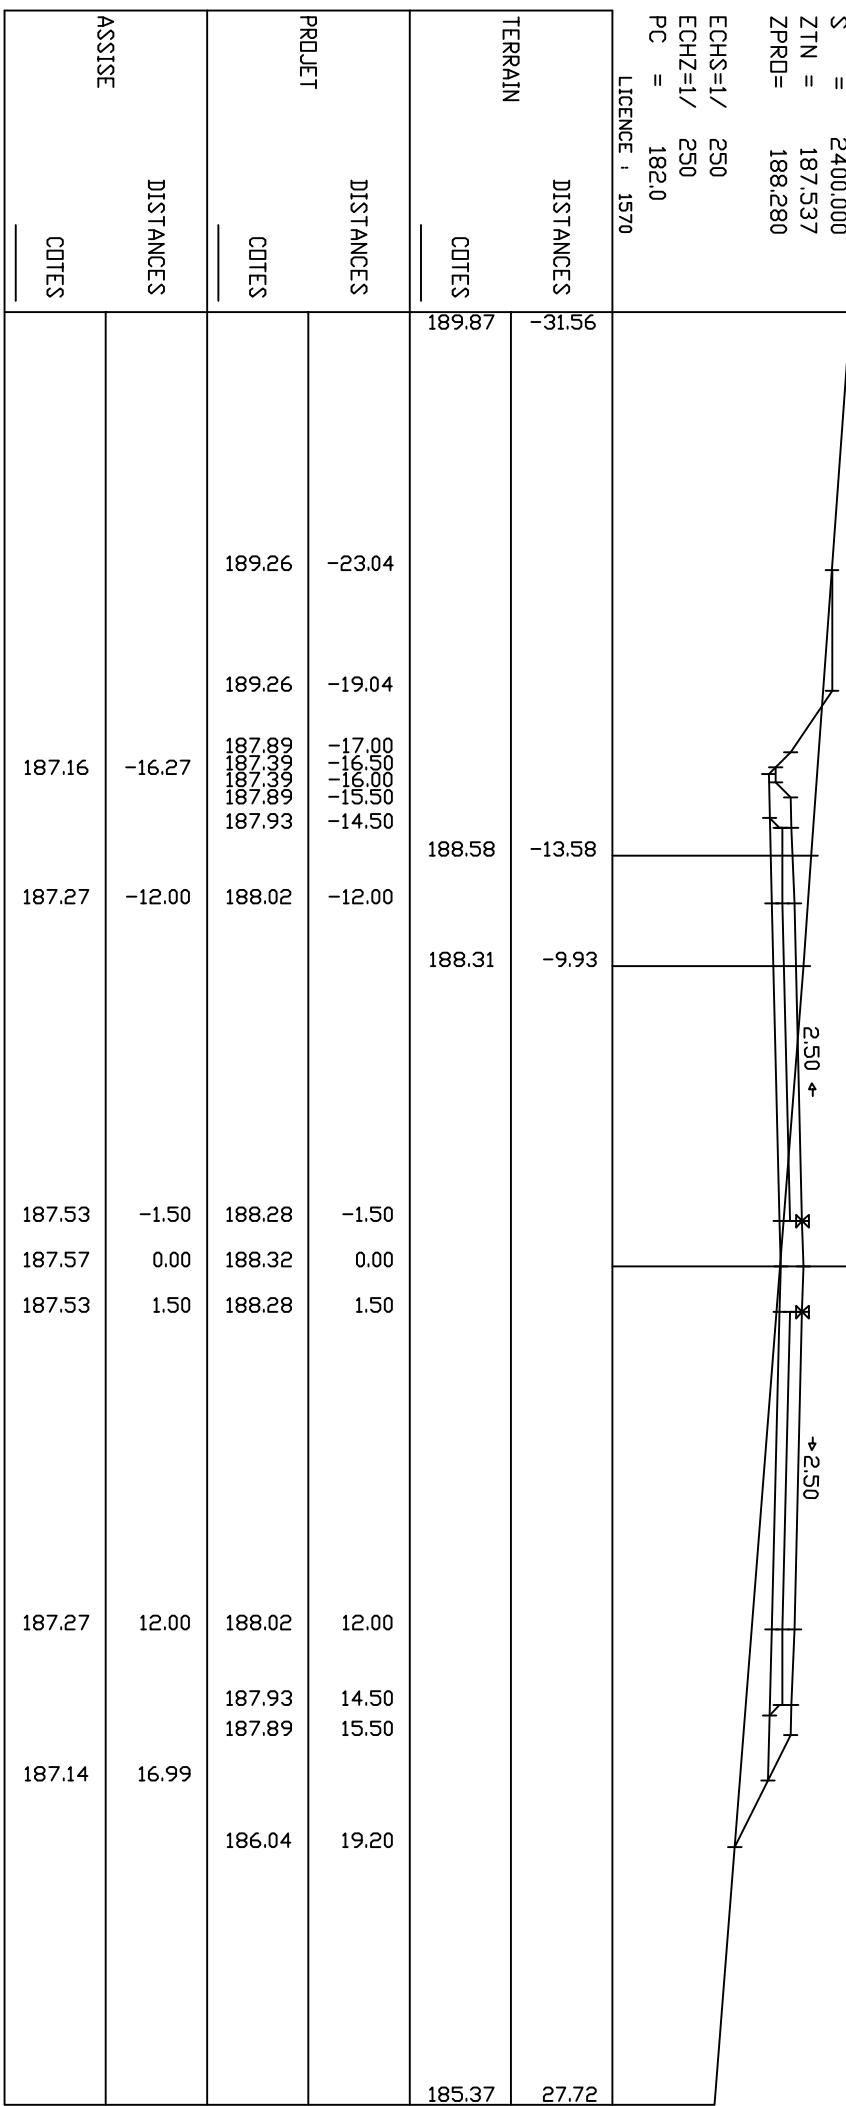

PROFIL 102

G2PIS

S = 2425.000
 ZTN = 186.636
 ZPRO= 188.201

ECHS=1/
 ECHZ=1/
 PC = 181.0
 LICENCE , 1570

TERRAIN

DISTANCES

COTES

188.59 -27.01

TERRAIN

DISTANCES

COTES

187.53 -12.43

TERRAIN

DISTANCES

COTES

187.76 -15.60

TERRAIN

DISTANCES

COTES

187.81 -14.50

TERRAIN

DISTANCES

COTES

187.94 -12.00

TERRAIN

DISTANCES

COTES

188.20 -1.50

TERRAIN

DISTANCES

COTES

188.24 0.00

TERRAIN

DISTANCES

COTES

188.20 1.50

TERRAIN

DISTANCES

COTES

187.12 -14.95

TERRAIN

DISTANCES

COTES

187.19 -12.00

TERRAIN

DISTANCES

COTES

187.19 12.00

TERRAIN

DISTANCES

COTES

187.06 16.99

TERRAIN

DISTANCES

COTES

187.85 14.50

TERRAIN

DISTANCES

COTES

187.81 15.50

TERRAIN

DISTANCES

COTES

185.13 20.86

TERRAIN

DISTANCES

COTES

184.32 32.13

TERRAIN

DISTANCES

COTES


184.31 32.27

PROFIL 103

G2PIS

S = 2450.000
 ZTN = 185.677
 ZPRO= 188.123


ECHS=1/
 ECHZ=1/
 PC = 250
 LICENCE , 180.0
 1570

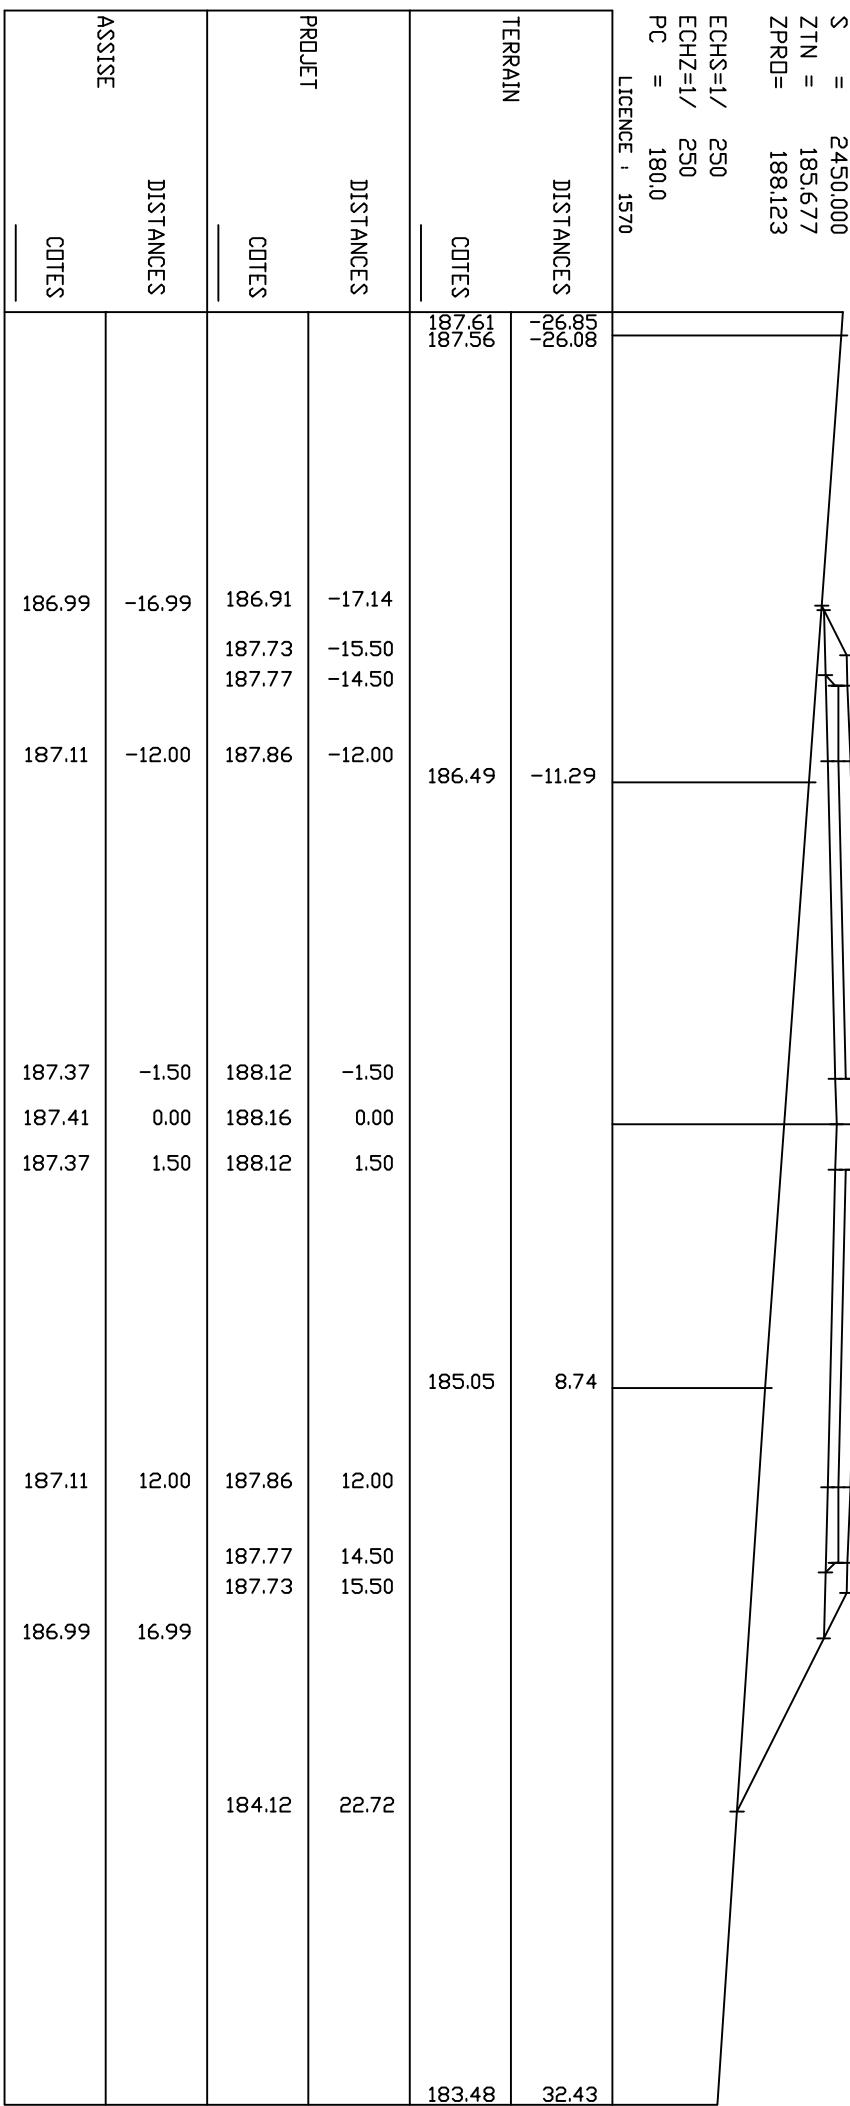

PROFIL 104

G2,PIS


S	=	2475.000
ZTN	=	184.827
ZPRD	=	188.046
ECHS=1/	250	
ECHZ=1/	250	
PC	=	180.0
LICENCE :	1570	

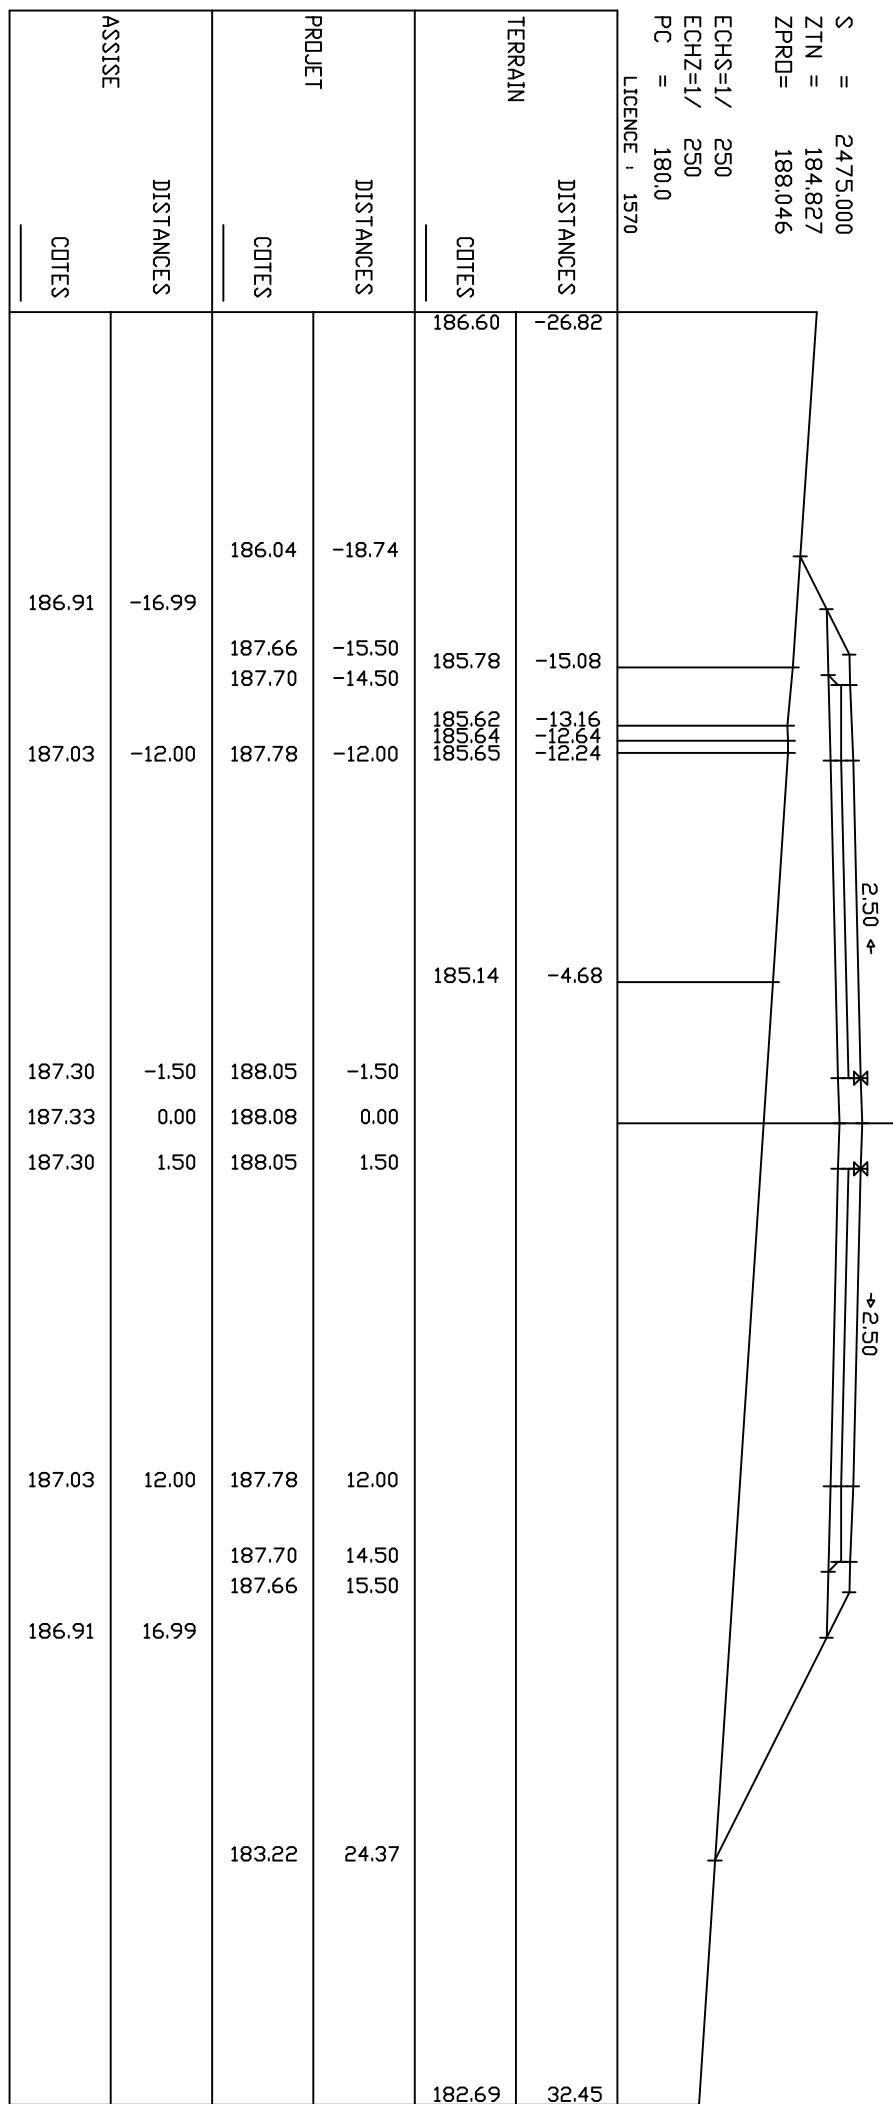

G2,PIS

ZTN = 2500.000
ZPRO= 184.184
188.001

LICENCE : 157
ECHS=1/ 250
ECHZ=1/ 250
PC = 179,0

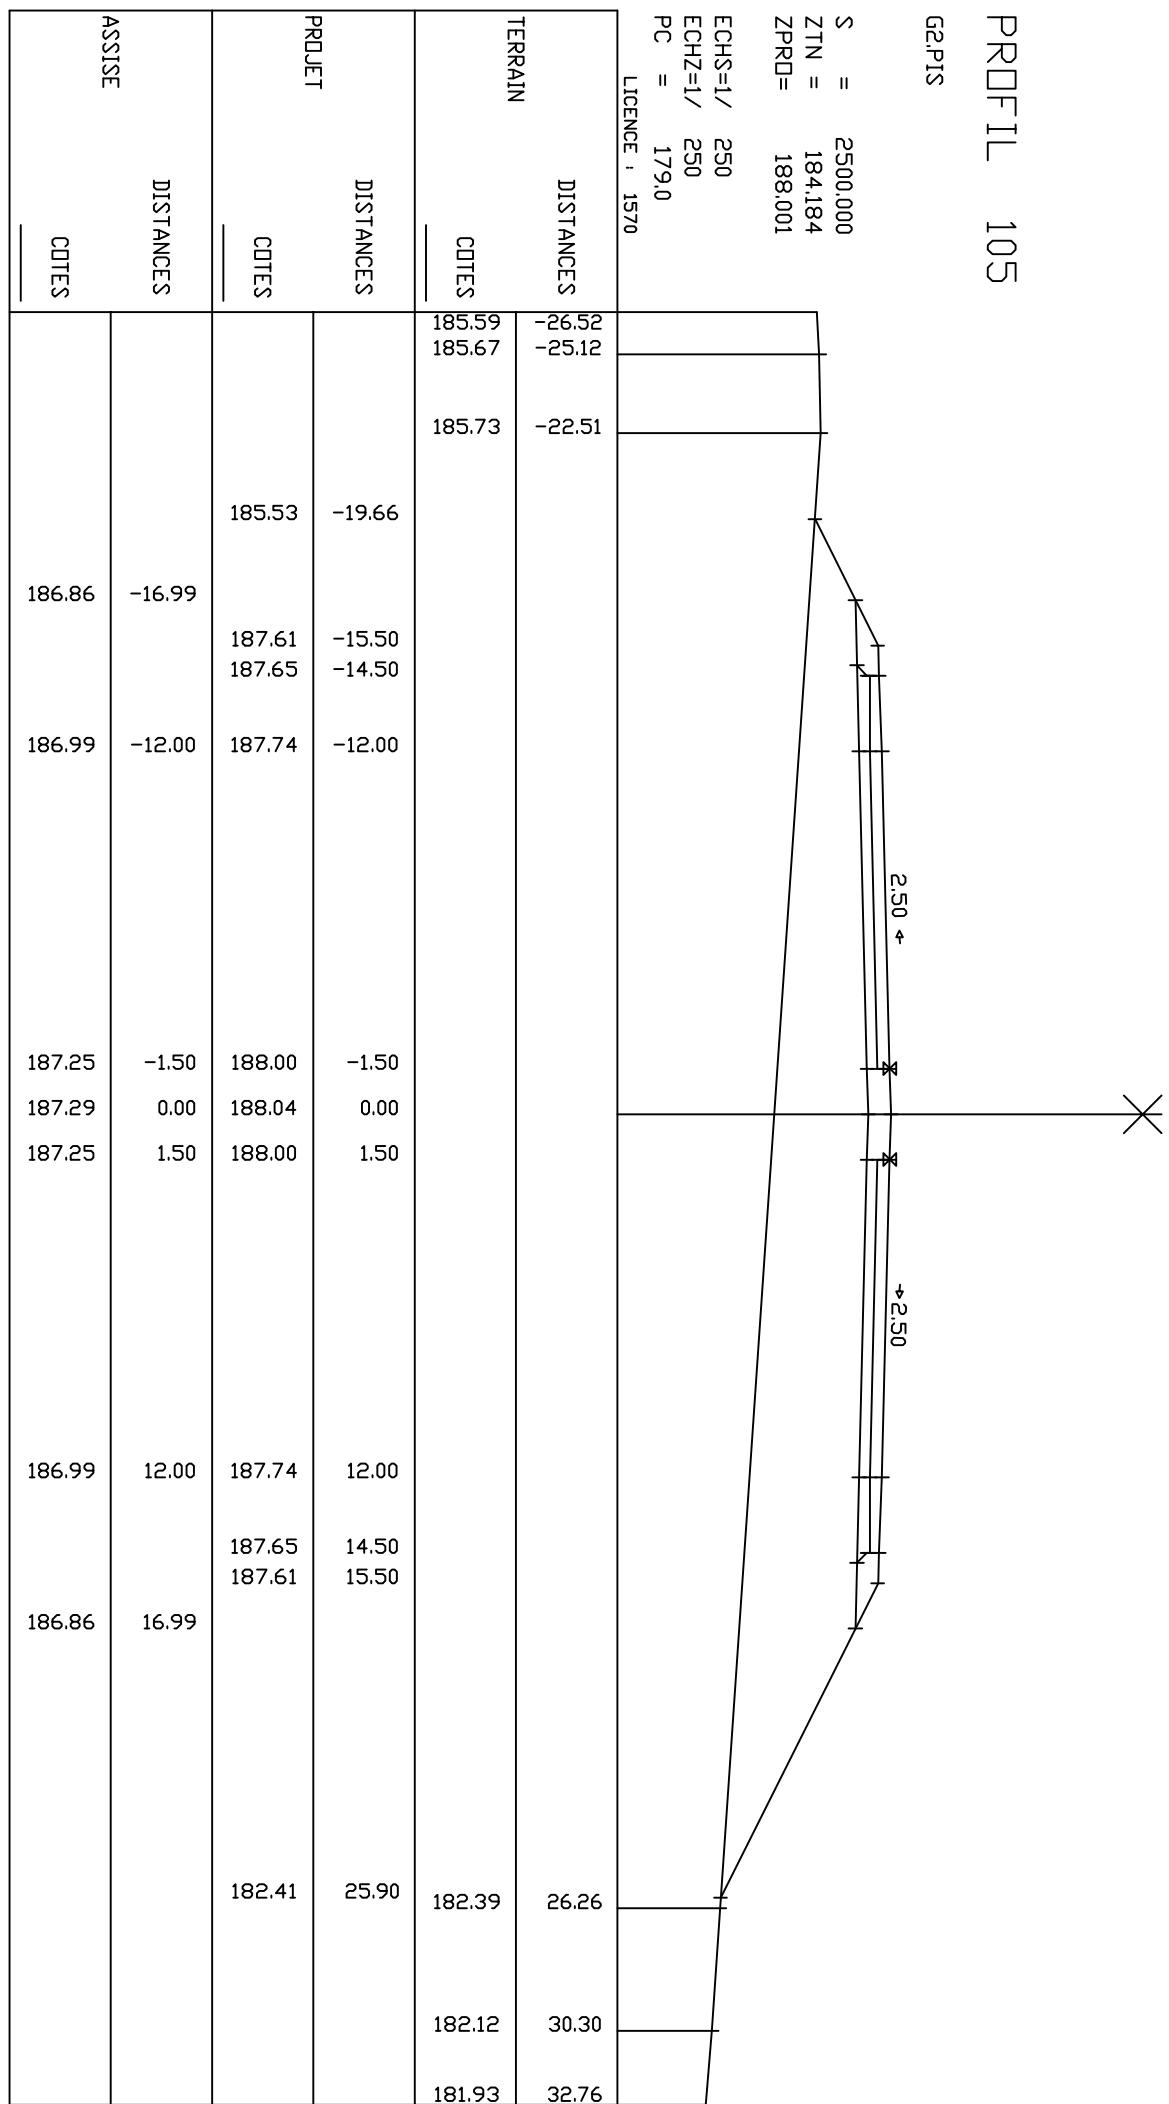


PROFIL 106

G2.PIS

S = 2525.000
ZTN = 183.889
ZPRO = 188.006

EJHS=1/
ECHZ=1/
PC = 179,0


LICENCE : 1570

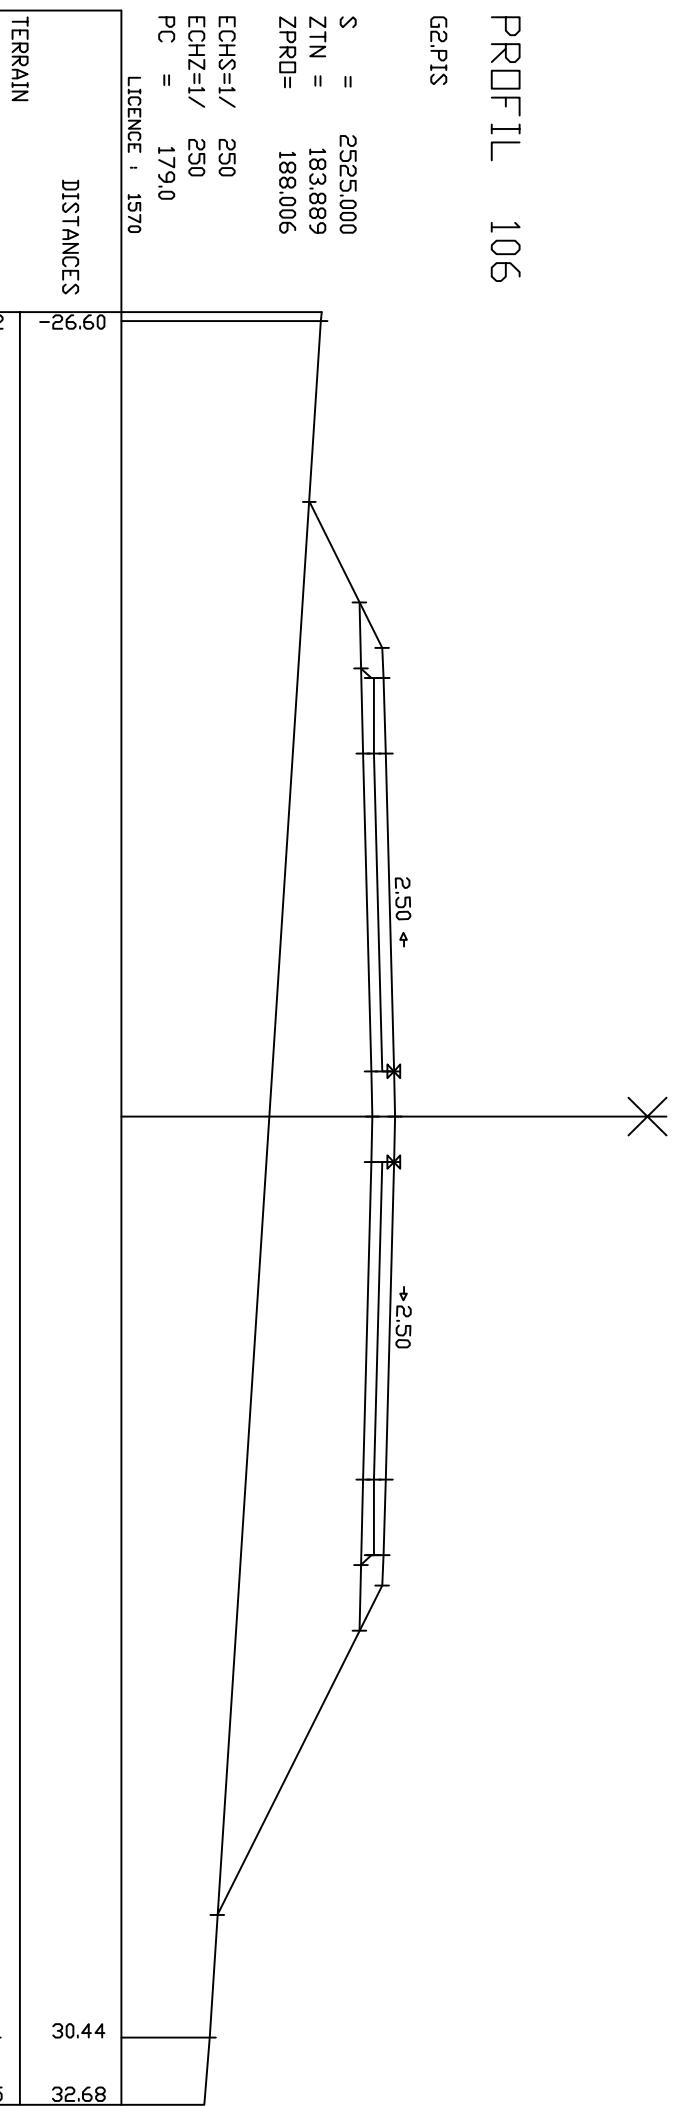

G2,PIS

S = 2550.000
ZTN = 185.084
ZPRO= 188.061

ECHS=1/ 250
ECHZ=1/ 250
PC = 180.0

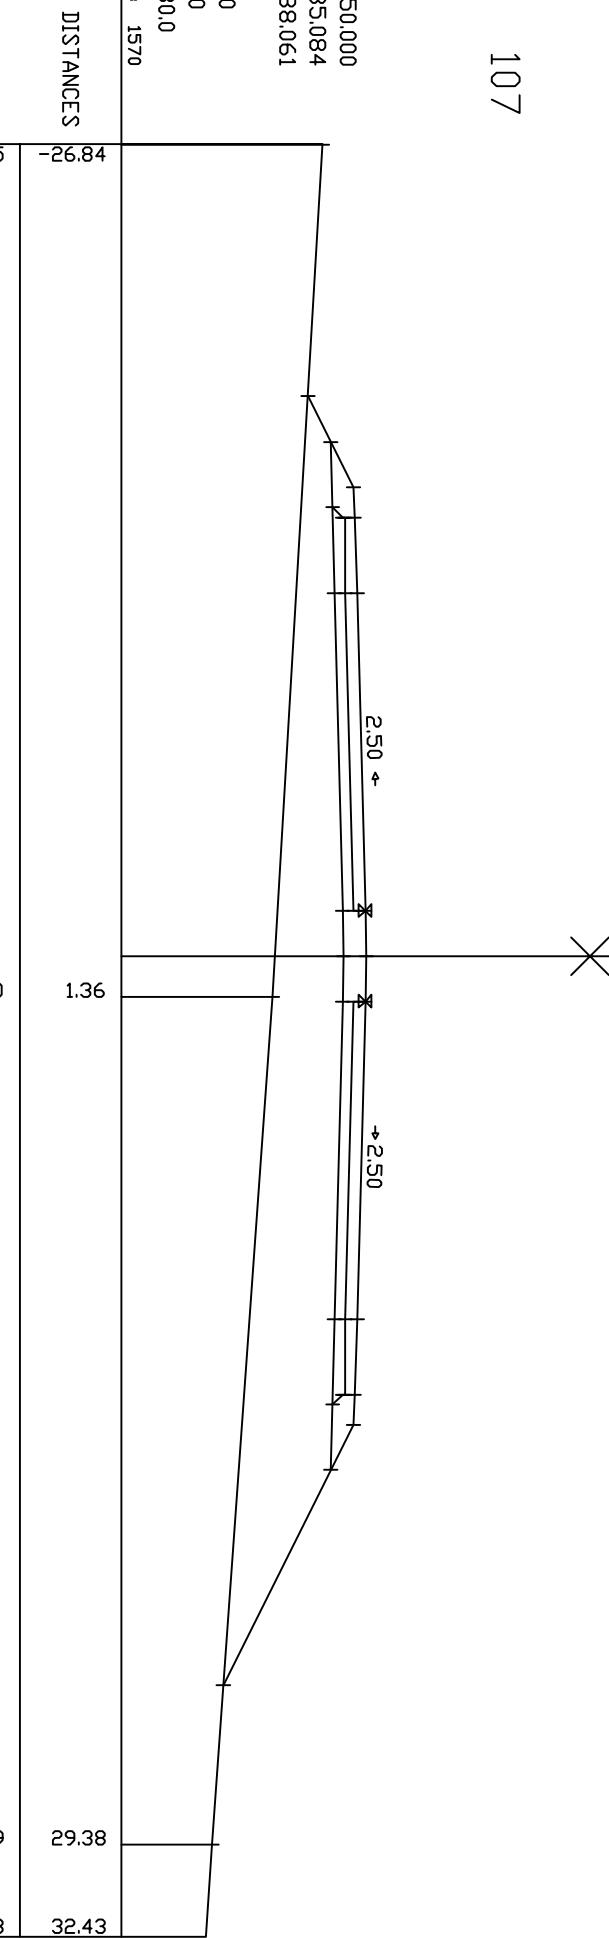

PRODUCED BY AN AUTODESK STUDENT VERSION


PRODUCED BY AN AUTODESK STUDENT VERSION

PROFIL 108

G2,PIS

S = 2575.000
ZTN = 185.817
ZPRO = 188.166

EJHS=1/
ECHZ=1/
PC = 181.0
LICENCE : 1570

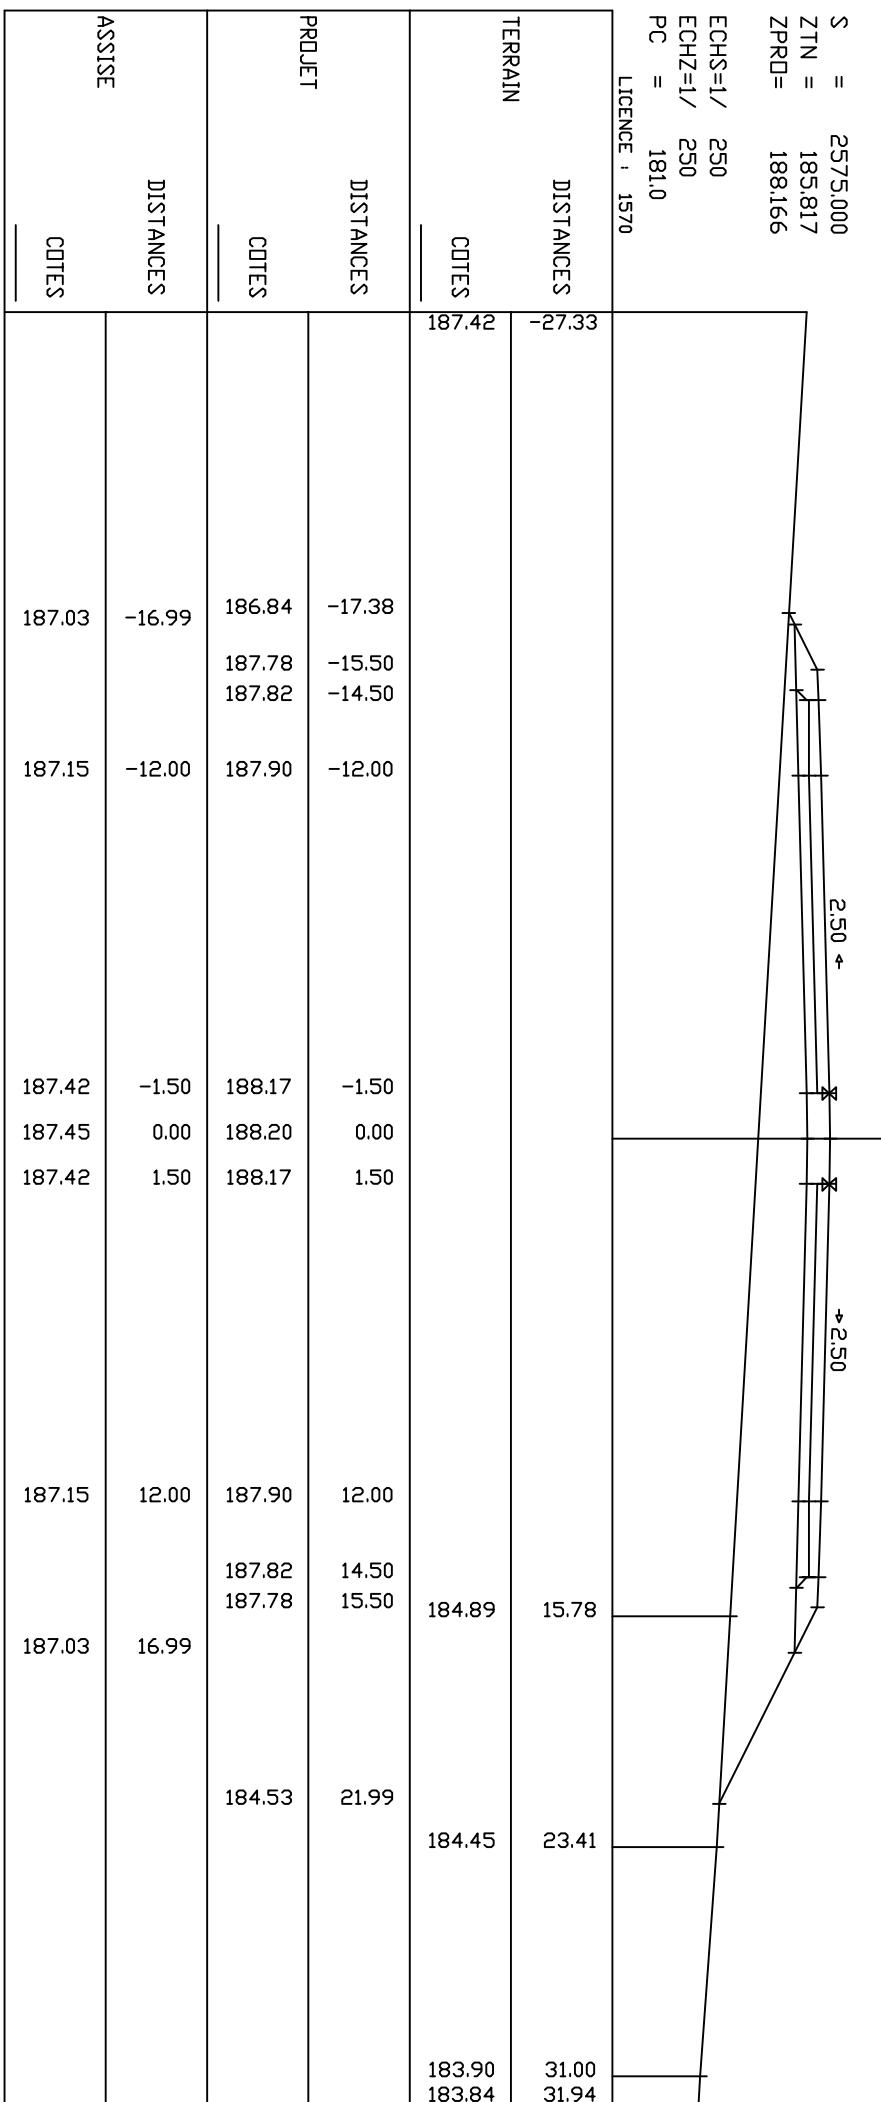


PROFIL 109

G2PIS

S = 2600.000
 ZTN = 186.555
 ZPRO= 188.304

ECHS=1/
 ECHZ=1/
 PC = 181.0
 LICENCE , 1570

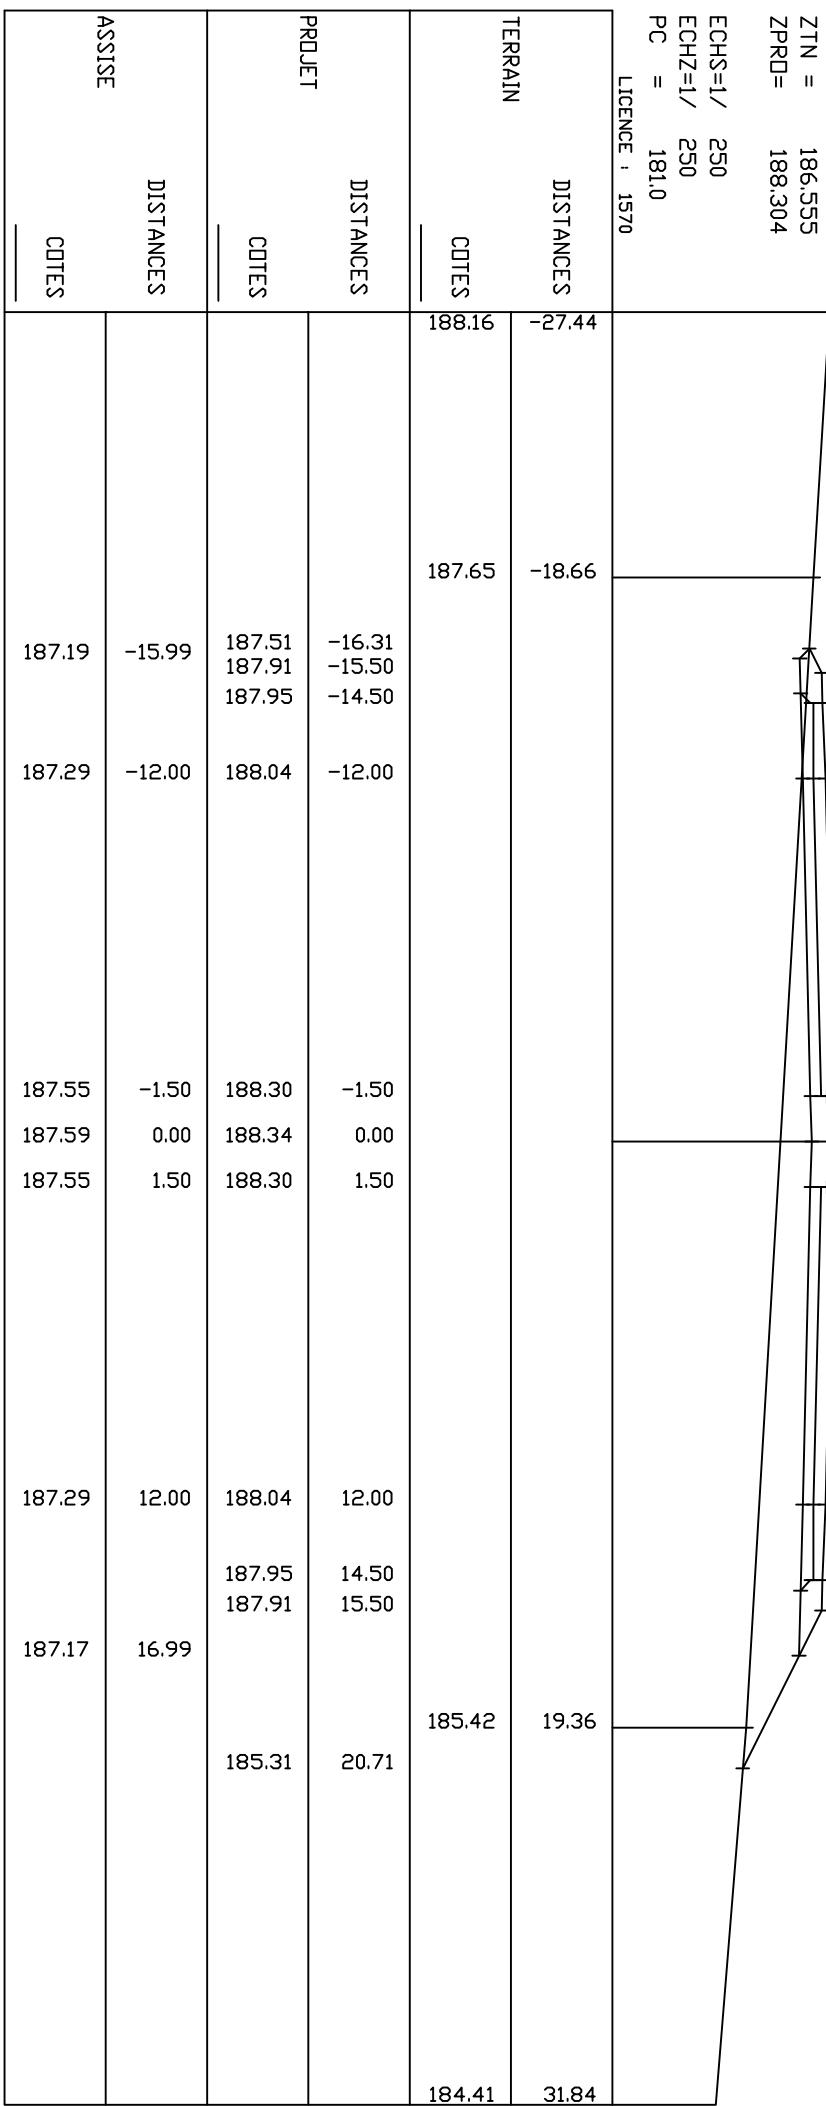

PROFIL 110

G2PIS

S = 2601538
 ZTN = 186.600
 ZPRO= 188.312

ECHS=1/
 ECHZ=1/
 PC = 181.0
 LICENCE , 1570

TERRAIN

DISTANCES

COTES

188.21 -27.42

187.68 -18.48

187.55 -16.24

187.92 -15.50

187.96 -14.50

188.05 -12.00

188.31 -1.50

188.35 0.00

188.31 1.50

188.05 12.00

187.96 14.50


187.92 15.50

185.54 18.16

20.68 31.86

184.42


ASSISE	DISTANCES	COTES	DISTANCES		COTES
			PROJECT	TERRAIN	
187.20	-15.89	187.55 187.92 187.96	-16.24 -15.50 -14.50	188.21 187.68 187.55	-27.42 -18.48 -1.50
187.30	-12.00	188.05	-12.00		
187.56	-1.50	188.31	-1.50		
187.60	0.00	188.35	0.00		
187.56	1.50	188.31	1.50		
187.30	12.00	188.05	12.00		
187.17	16.99	187.96 187.92 185.33	14.50 15.50 20.68	185.54 18.16 31.86	

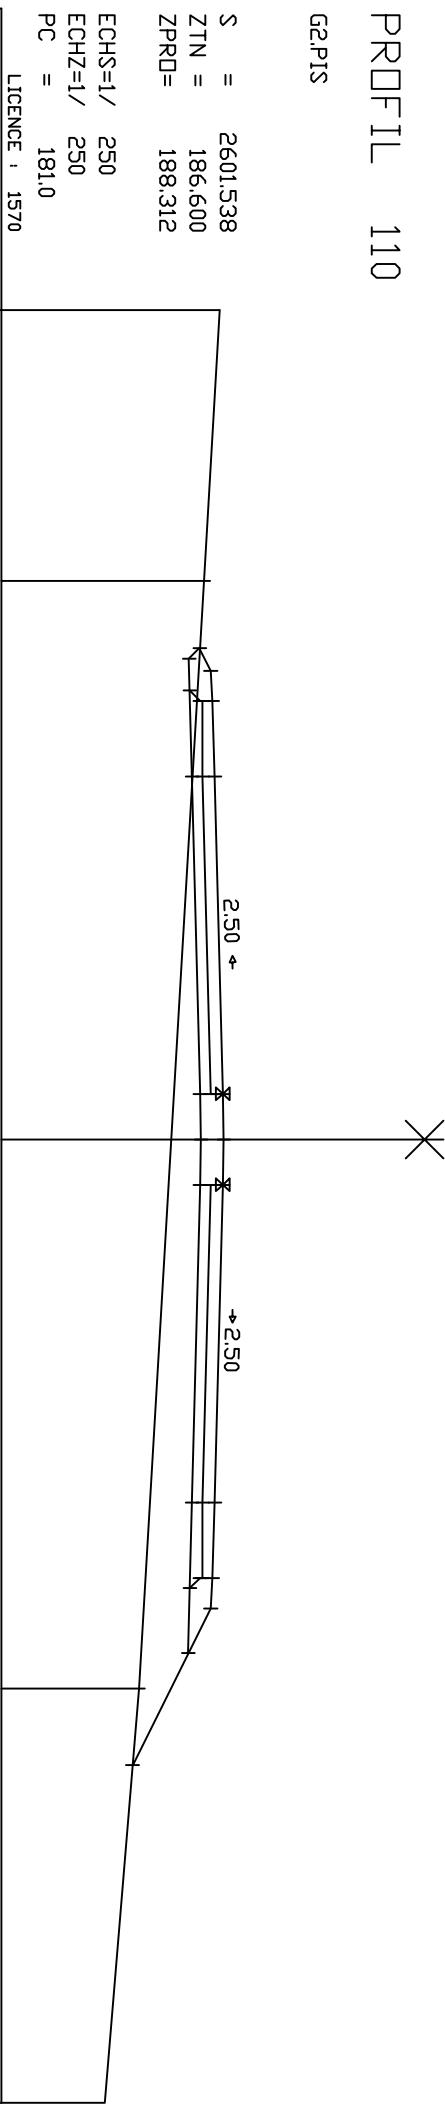

PROFIL 111

G2,PIS

S = 2625.000
ZTN = 187,310
ZPRO = 188,442

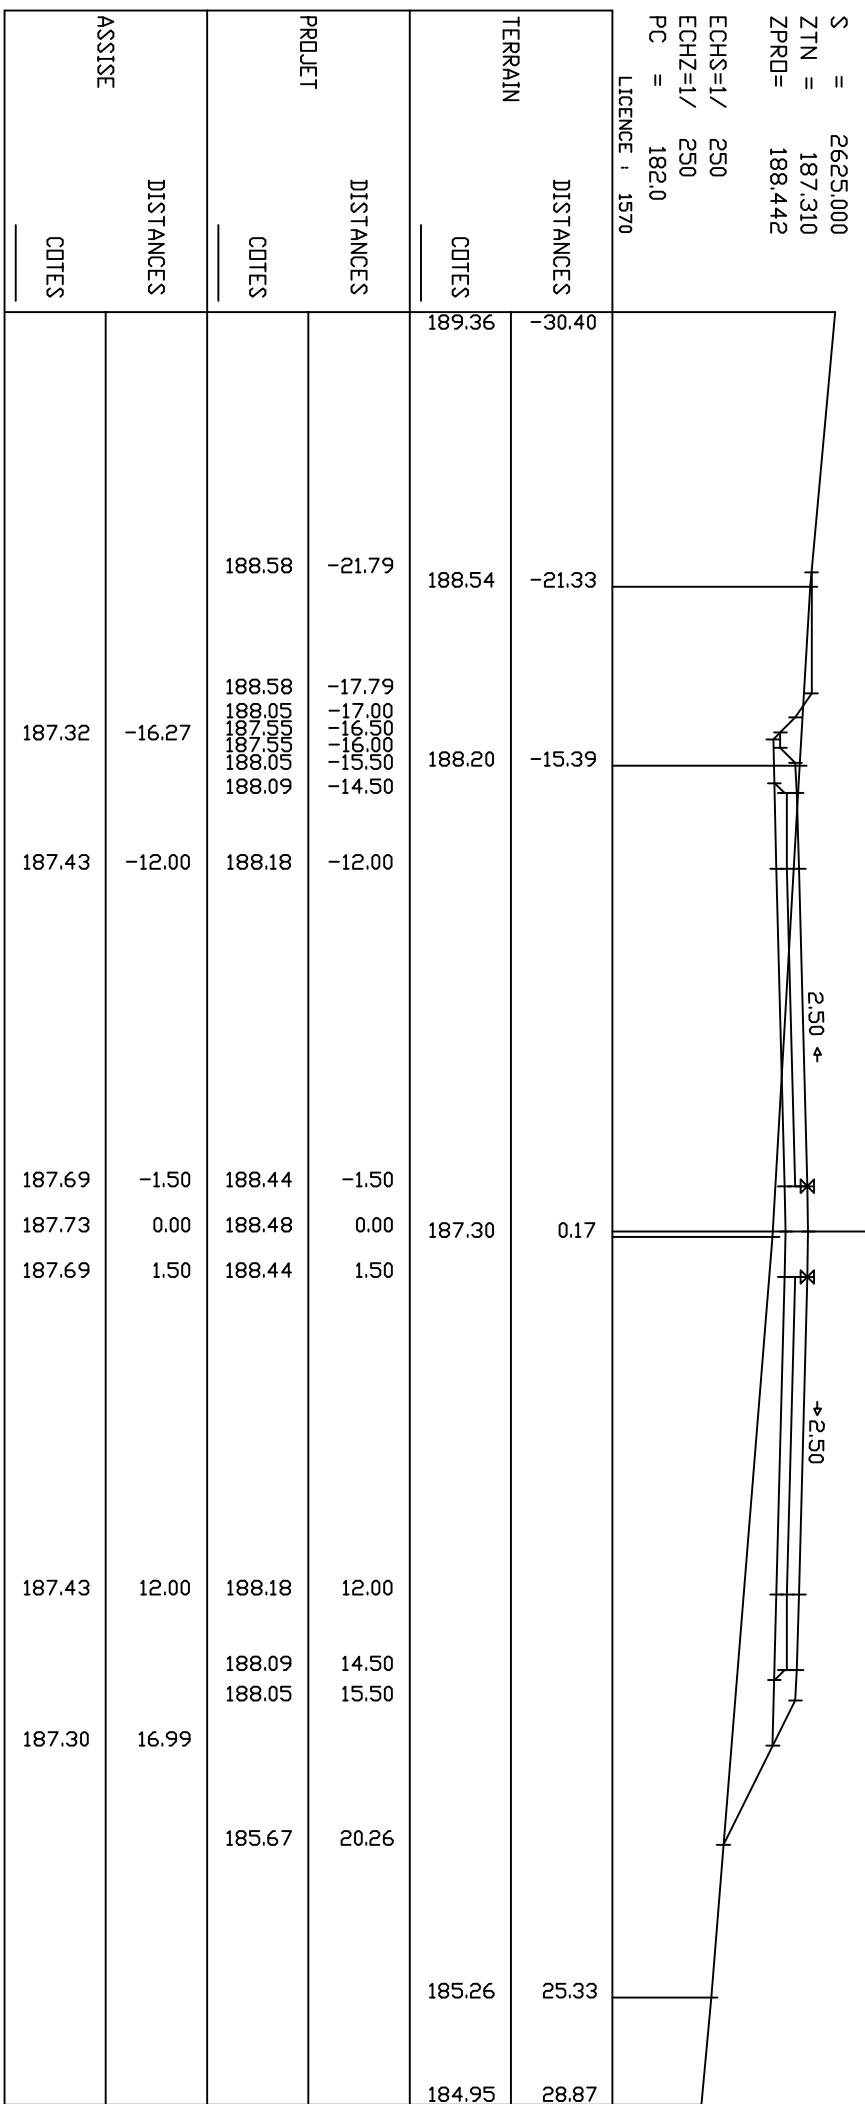

PROFIL 112

G2PIS

S = 2650.000
 ZTN = 187.524
 ZPROD= 188.580

ECHS=1/
 ECHZ=1/
 PC = 182.0
 LICENCE , 1570

TERRAIN

DISTANCES

COTES

189.81 -30.78

DISTANCES

COTES

189.28 -22.63

DISTANCES

COTES

189.28 -18.63

DISTANCES

COTES

188.19 -17.00

DISTANCES

COTES

187.69 -16.50

DISTANCES

COTES

187.69 -16.00

DISTANCES

COTES

188.19 -15.50

DISTANCES

COTES

188.23 -14.50

DISTANCES

COTES

188.23 -12.00

DISTANCES

COTES

188.32 -12.00

DISTANCES

COTES

188.58 -1.50

DISTANCES

COTES

188.62 0.00

DISTANCES

COTES

188.58 1.50

DISTANCES

COTES

188.23 12.00

DISTANCES

COTES

188.19 14.50

DISTANCES

COTES

185.77 20.34


DISTANCES

COTES

185.07 28.50

DISTANCES

COTES

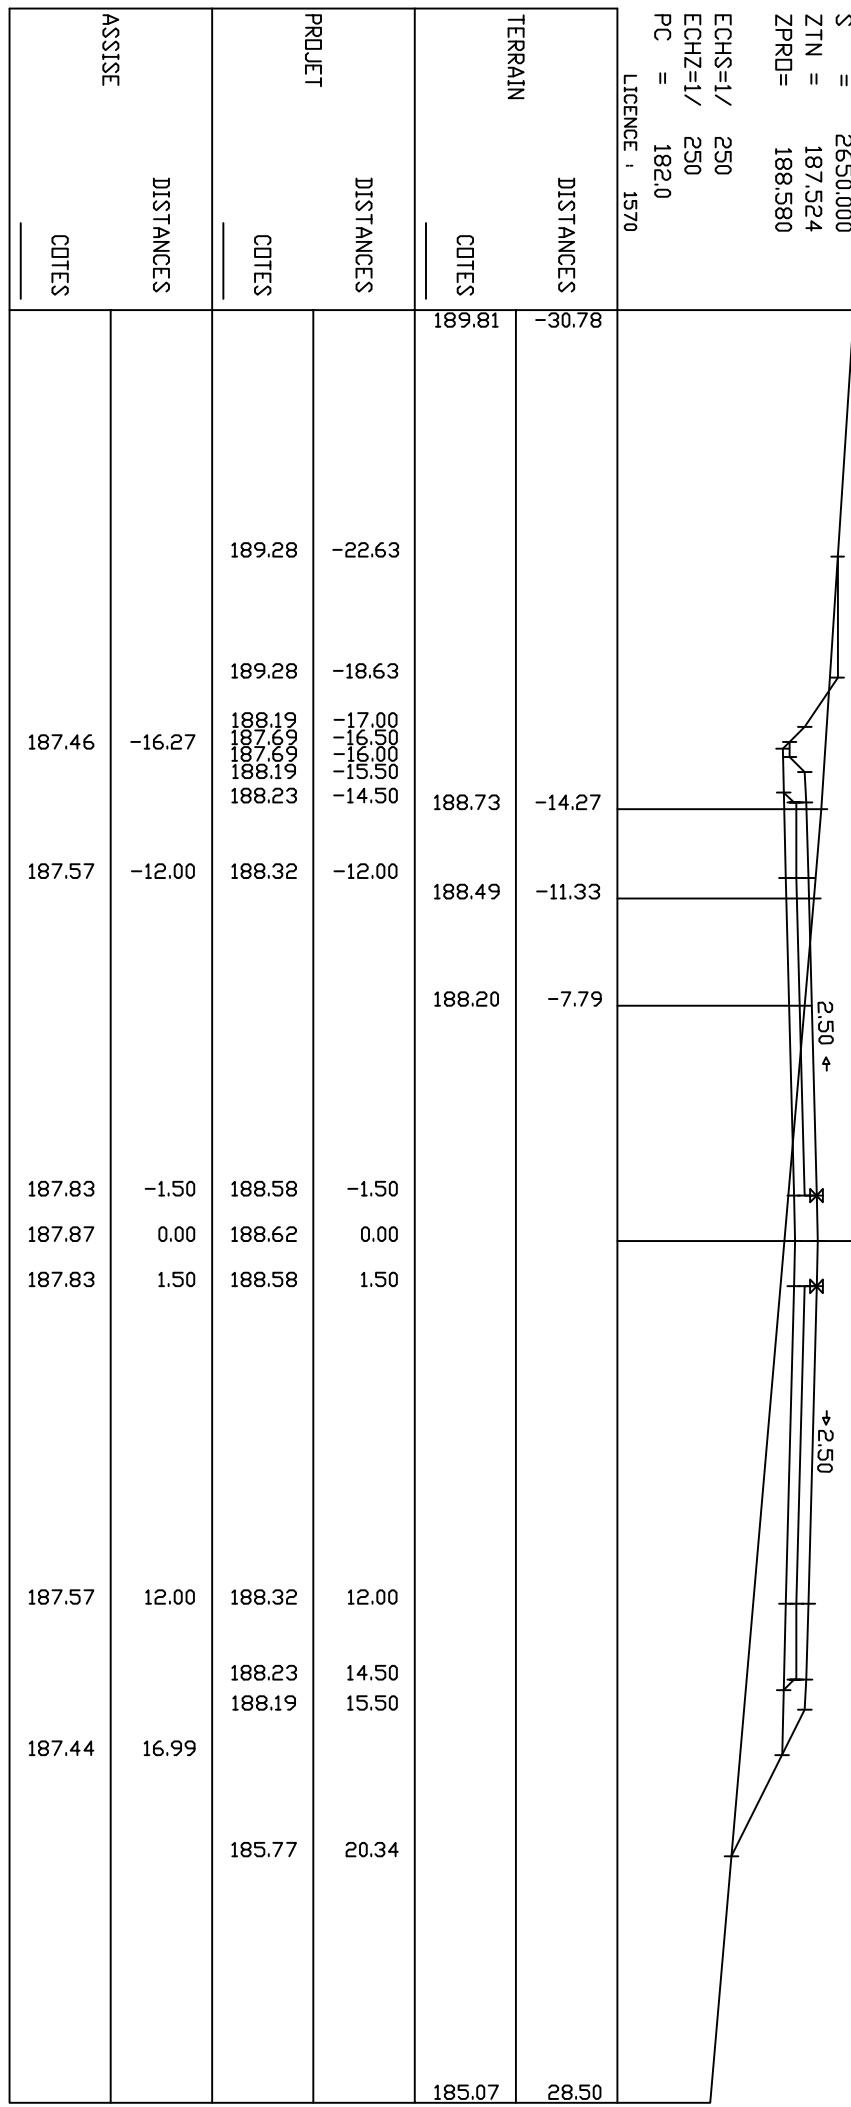


PROFIL 113

G2PIS

S = 2675.000
 ZTN = 187.625
 ZPRO= 188.719

ECHS=1/
 ECHZ=1/
 PC = 182.0
 LICENCE , 1570

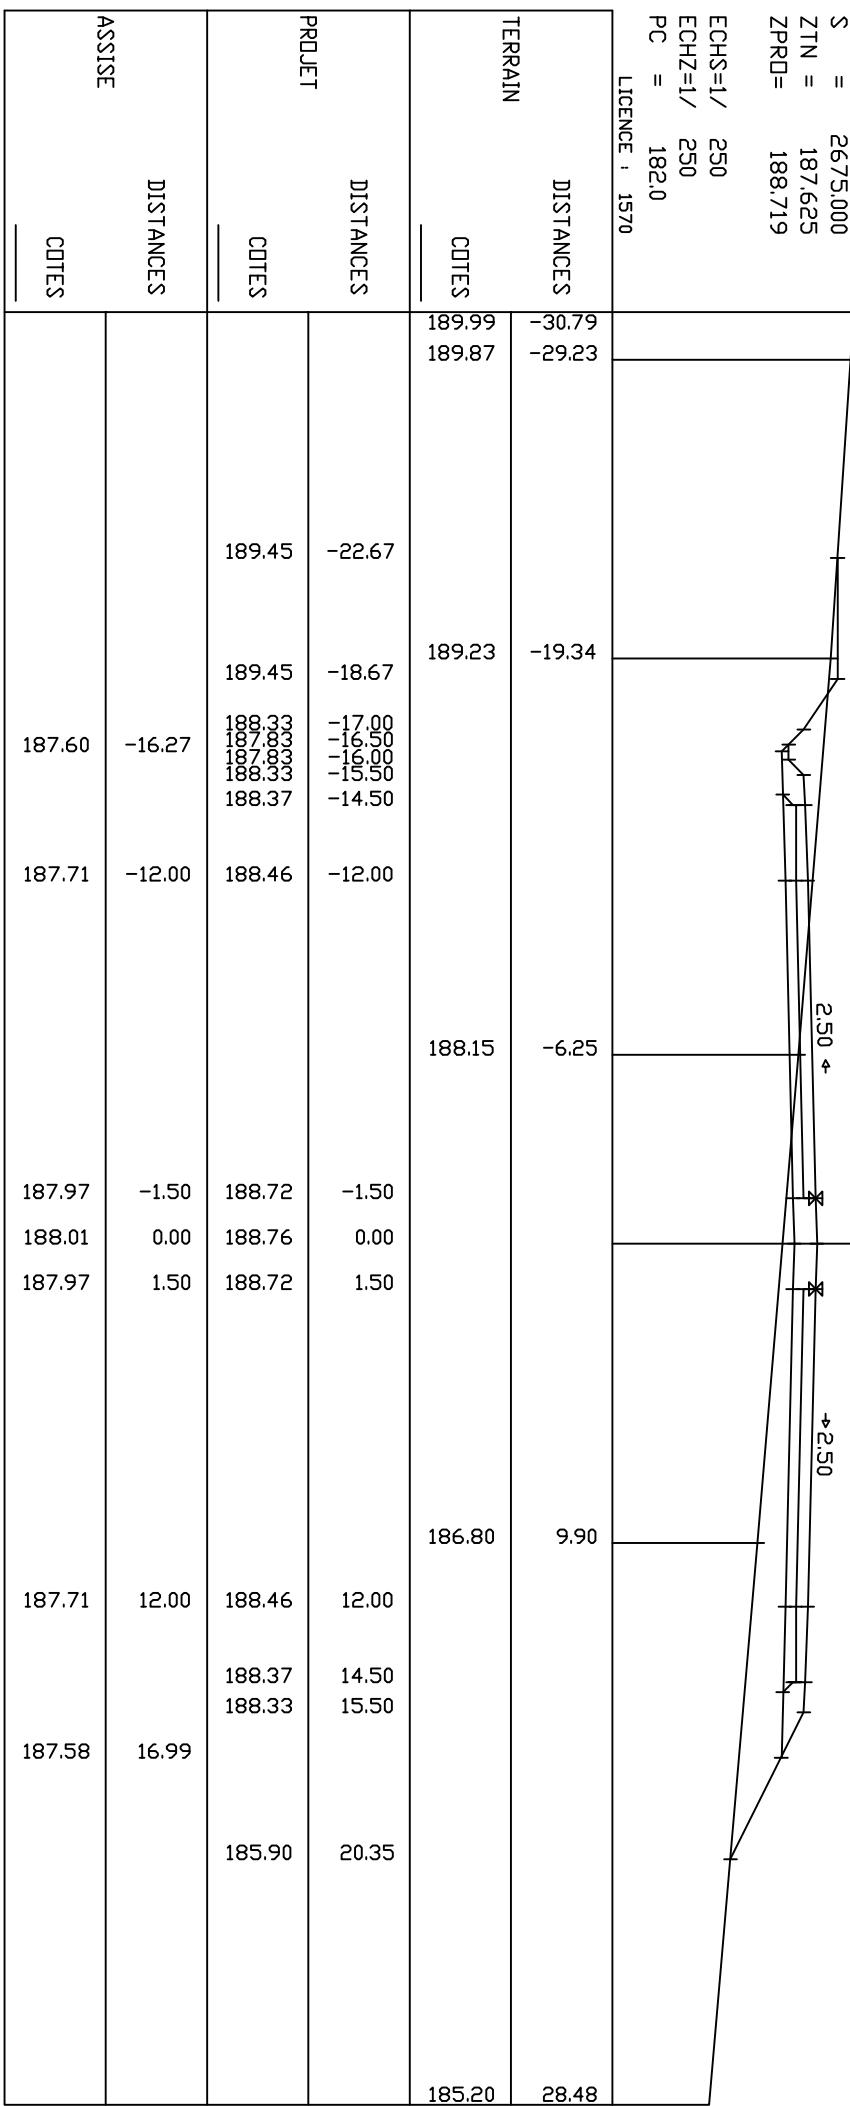

PROFIL 114

G2PIS

S = 2700.000
 ZTN = 187.756
 ZPRO= 188.857

ECHS=1/
 ECHZ=1/
 PC = 182.0
 LICENCE , 1570

TERRAIN

DISTANCES

COTES

190.19 -30.80

DISTANCES

COTES

188.01 -3.03

DISTANCES

COTES

187.80 -0.49

DISTANCES

COTES

187.84 12.00 188.59 12.00

DISTANCES

COTES

188.51 14.50

DISTANCES

COTES

188.47 15.50

DISTANCES

COTES

186.07 20.29

DISTANCES

COTES

185.39 28.48

ASSISE	DISTANCES	COTES			
187.74	-16.27	189.55	-22.61		
187.84	-12.00	189.55	-18.61		
		188.47	-17.00		
		187.97	-16.50		
		187.97	-16.00		
		188.47	-15.50		
		188.51	-14.50		
188.11	-1.50	188.86	-1.50		
188.14	0.00	188.89	0.00		
188.11	1.50	188.86	1.50		
187.84	12.00	188.59	12.00		
187.72	16.99	188.51	14.50		
		188.47	15.50		
		186.07	20.29		

PROFIL 115

G2PIS

S = 2725.000
 ZTN = 187.673
 ZPRO= 188.995

ECHS=1/
 ECHZ=1/
 PC = 183.0
 LICENCE , 1570

TERRAIN

DISTANCES

COTES

190.12 -30.52

DISTANCES

COTES

188.92 -15.77

DISTANCES

COTES

188.08 -5.35

DISTANCES

COTES

187.98 -3.96

DISTANCES

COTES

187.98 15.95

DISTANCES

COTES

186.44 12.00

DISTANCES

COTES


185.50 28.76

ASSISE	DISTANCES	COTES	PROJECT		DISTANCES	COTES	DISTANCES	COTES
			DISTANCES	COTES				
187.88	-16.27	189.45	-22.25					
		189.45	-18.25					
		188.61	-17.00					
		188.11	-16.50					
		188.11	-16.00					
		188.61	-15.50					
		188.65	-14.50					
187.98	-12.00	188.73	-12.00					
188.25	-1.50	189.00	-1.50					
188.28	0.00	189.03	0.00					
188.25	1.50	189.00	1.50					
187.98	12.00	188.73	12.00					
		188.65	14.50					
		188.61	15.50					
187.86	16.99	186.11	20.50					

卷之三

G2,PIS

S = 2/50.000
ZTN = 188,664
ZPRD= 189,134

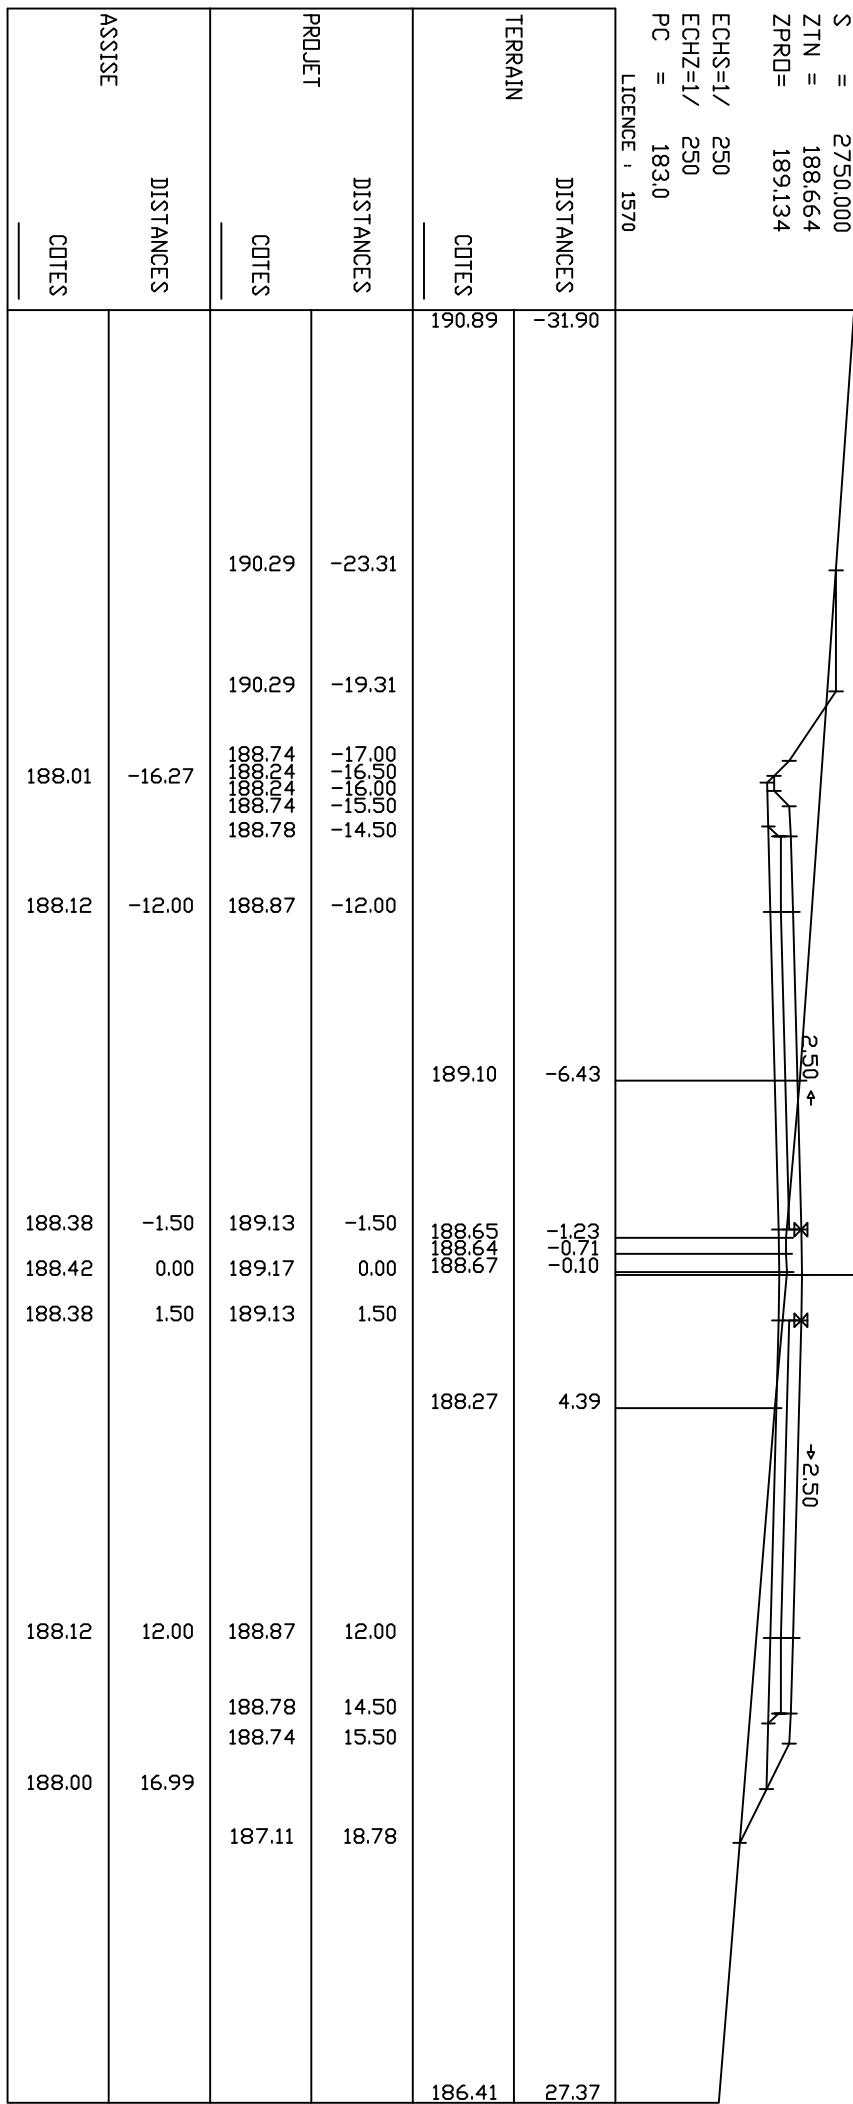

PROFIL 117

G2PIS

S = 2775.000
 ZTN = 188.976
 ZPRO= 189.272
 ECHS=1/
 ECHZ=1/
 PC = 184.0
 LICENCE , 1570

TERRAIN
 DISTANCES
 COTES

191.22
 191.13

-32.43

-31.02


		PROFIL 118		G2PIS	
				S = 2800.000 ZTN = 188.871 ZPRD= 189.410	
				ECHS=1/ ECHZ=1/ PC = 184.0 LICENCE , 1570	
		DISTANCES		TERRAIN	
DISTANCES		COTES		COTES	
COTES					
ASSISE	DISTANCES	188.29	-16.27	190.26	-22.85
		188.40	-12.00	190.26	-18.85
		188.66	-1.50	189.02	-17.00
		188.70	0.00	189.02	-16.00
		188.66	1.50	189.06	-15.50
		188.40	12.00	189.15	-14.50
		188.27	16.99	189.15	-12.00
				189.41	-1.50
				189.45	0.00
				189.41	1.50
				189.06	14.50
				189.02	15.50
				187.74	18.06
				187.17	27.24

PROFIL 118

G2PIS

S = 2800.000
ZTN = 188.871
ZPRD= 189.410

ECHS=1/
ECHZ=1/
PC = 184.0
LICENCE , 1570

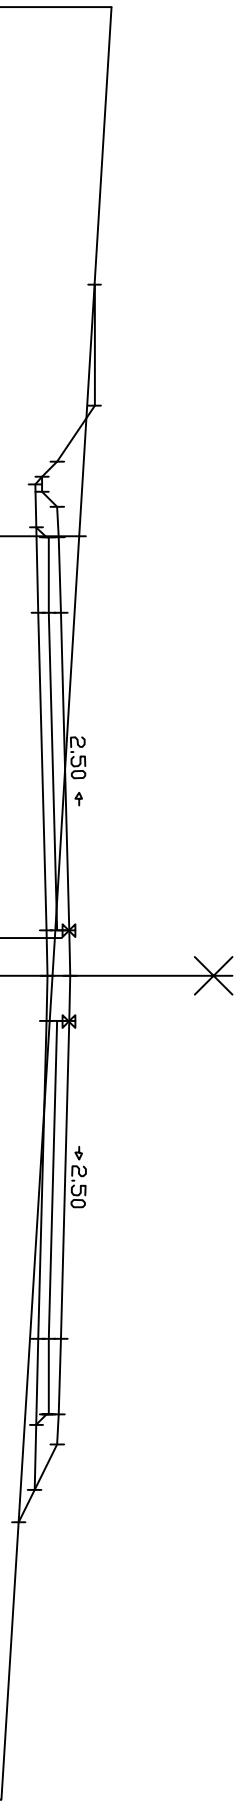


PROFIL 119

G2PIS

S = 2825.000
 ZTN = 188.549
 ZPRO= 189.548

ECHS=1/
 ECHZ=1/
 PC = 184.0
 LICENCE , 1570

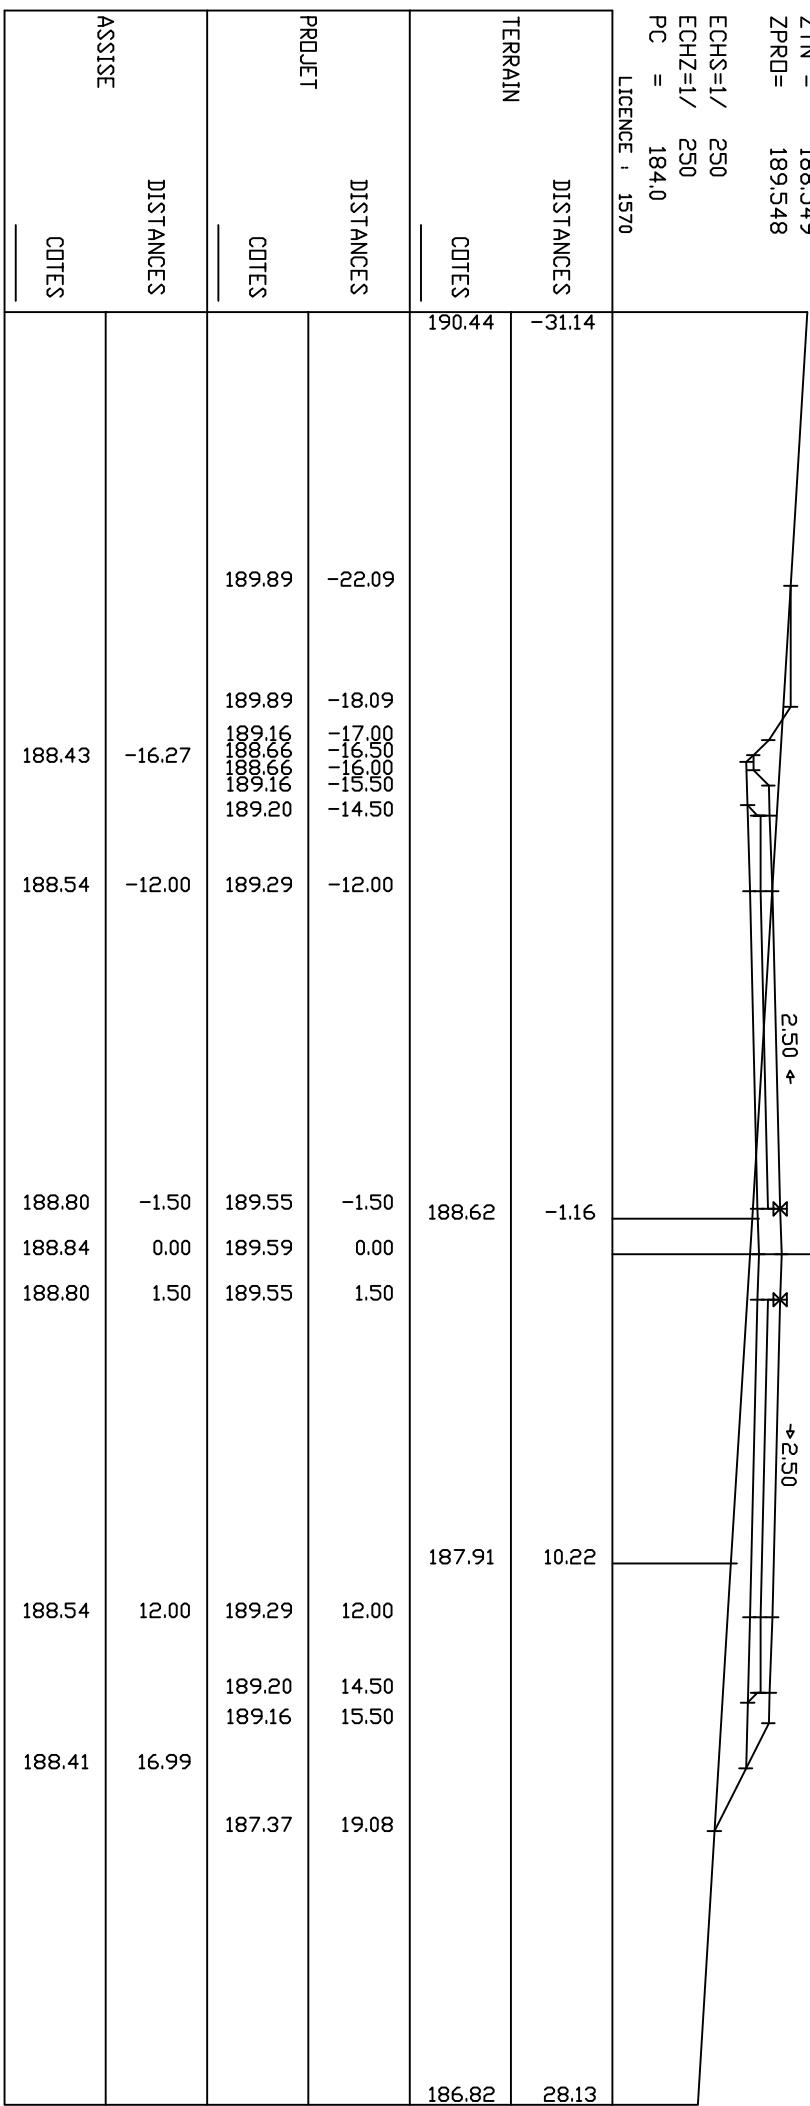


DRILL

EPICS

S = 2850.000
ZTN = 188.349
ZPRD= 189.687

ECHS=1/
ECHZ=1/
PC = 183,0
LICENCE : 1570

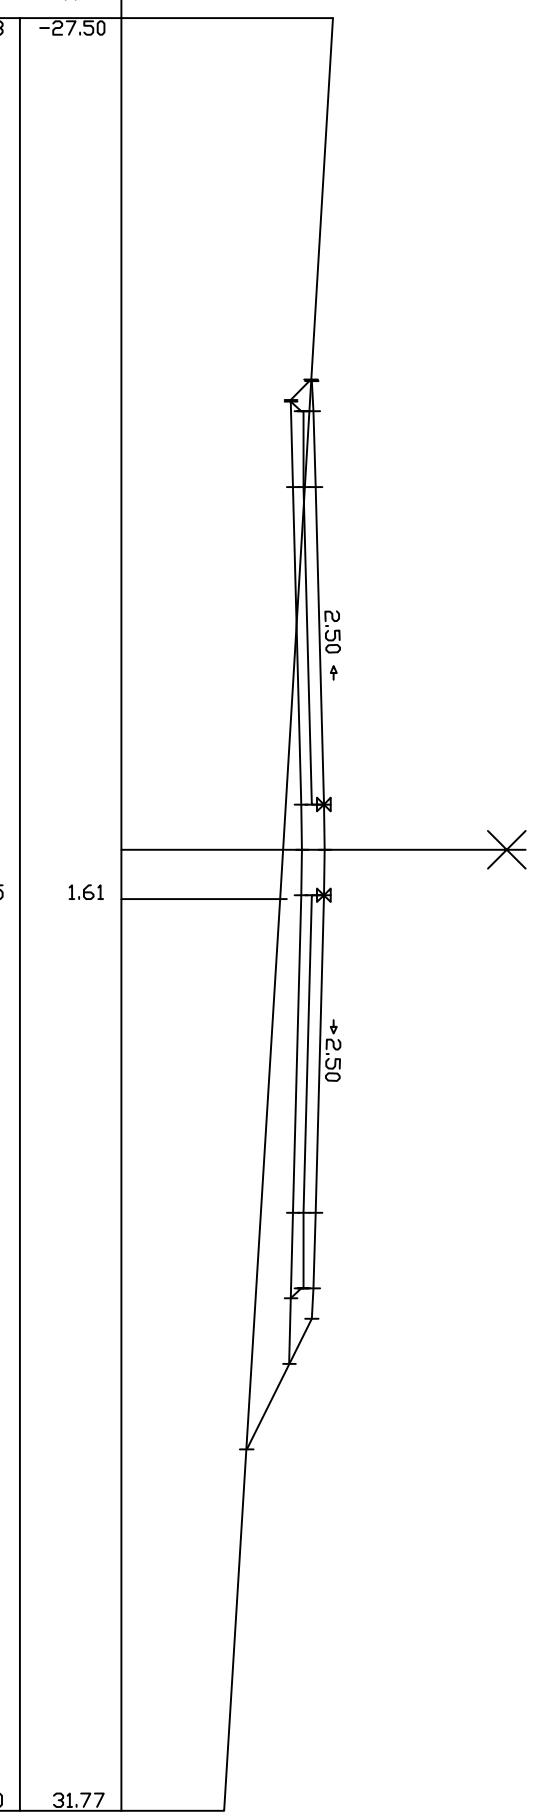


PROFIL 121

G2PIS

S = 2875.000
 ZTN = 188.230
 ZPRO= 189.825


ECHS=1/
 ECHZ=1/
 PC = 250
 LICENCE , 183.0
 1570

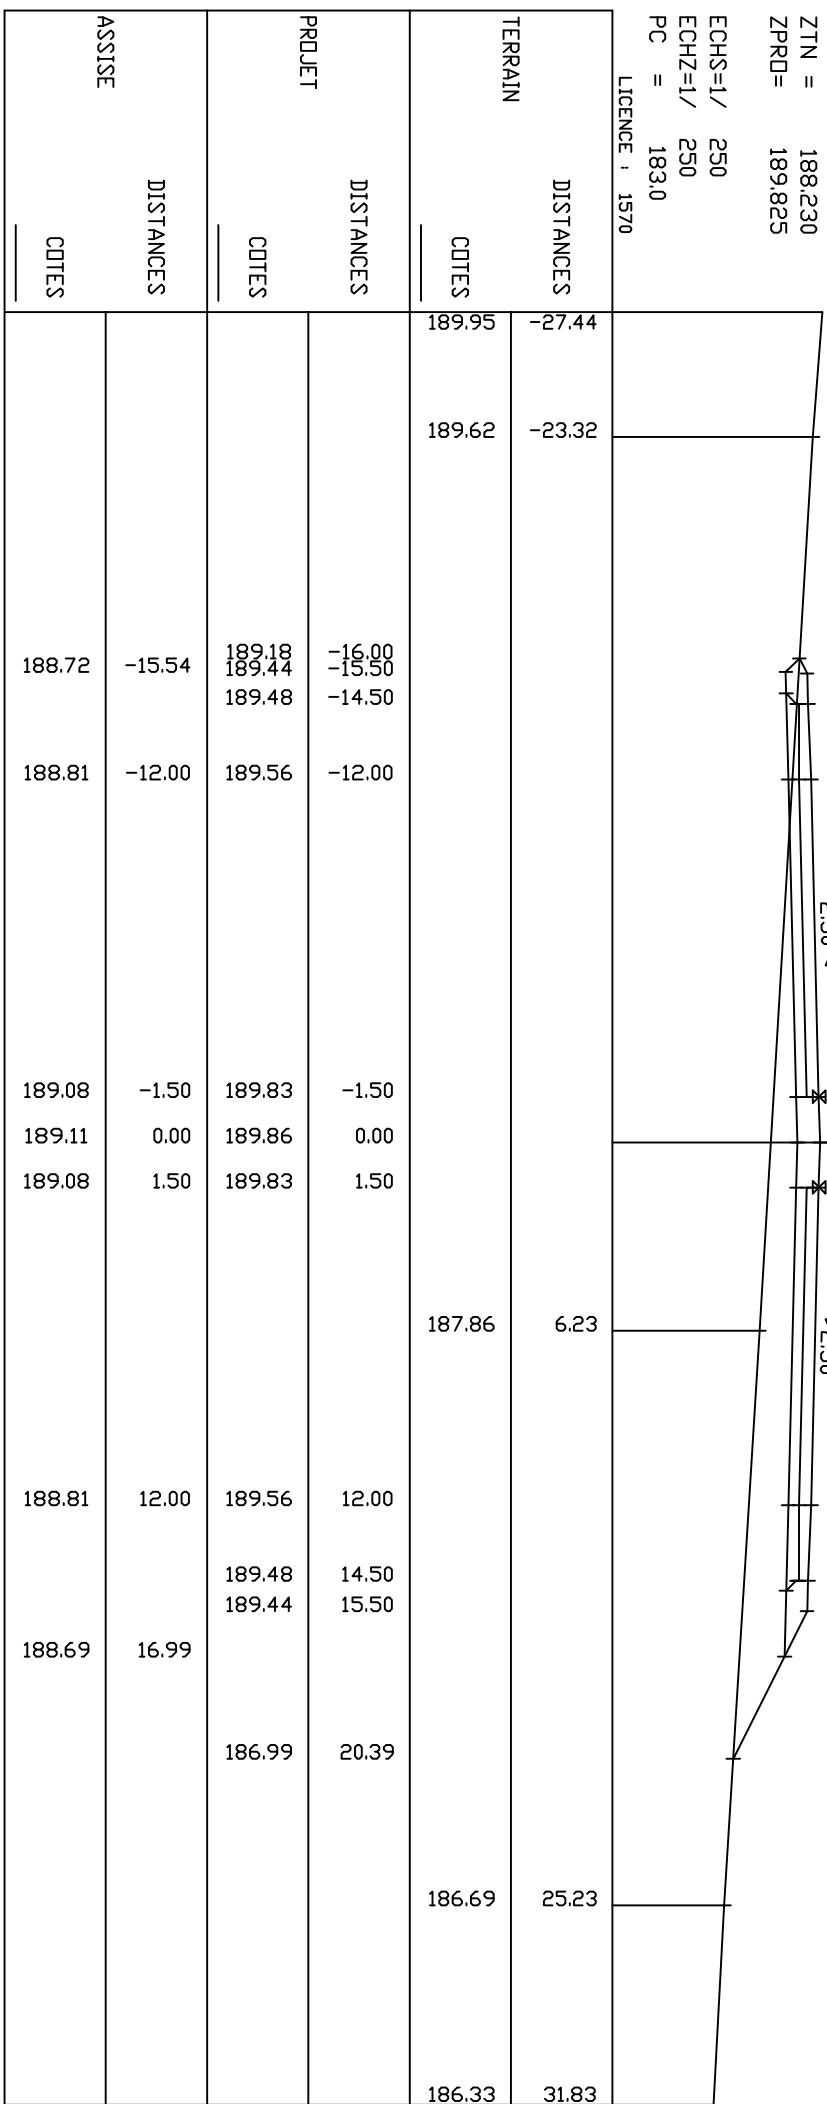

PROFIL 122

G2,PIS

S = 2900.000
ZTN = 188.274
ZPRD = 189.963

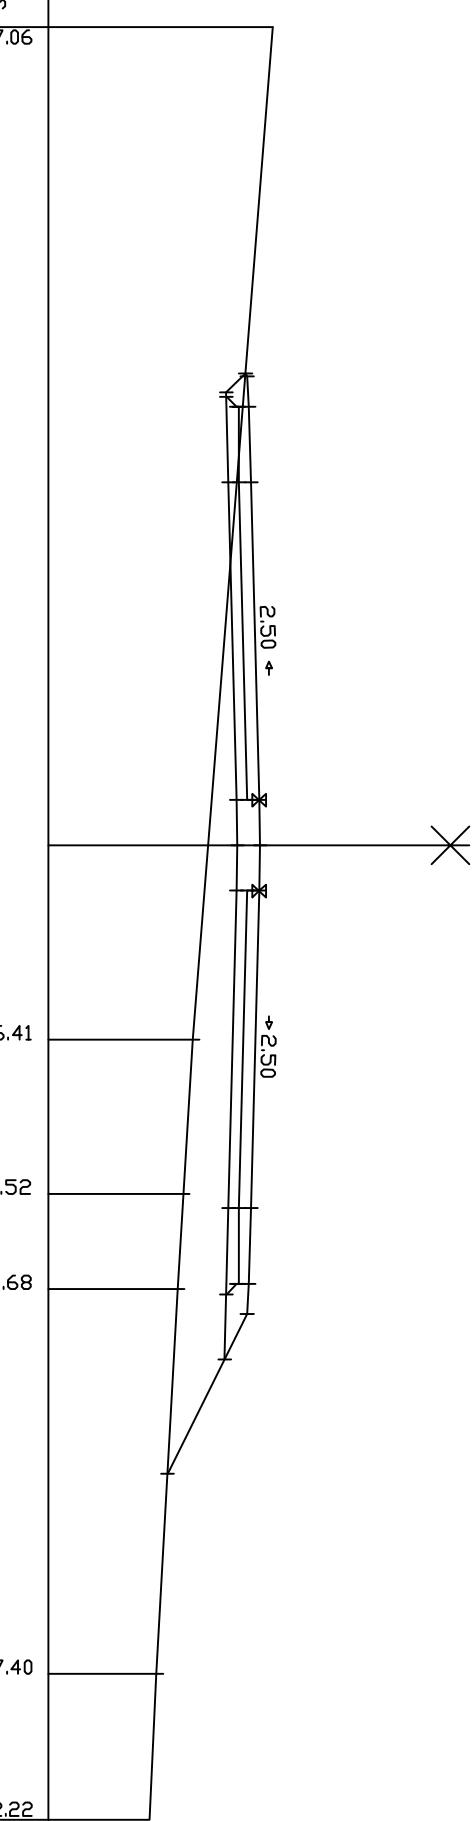

PROFIL 123

G2PIS

S = 2925.000
 ZTN = 189.196
 ZR0= 190.102

ECHS=1/
 ECHZ=1/
 PC = 184.0
 LICENCE , 1570

TERRAIN

DISTANCES

COTES

191.25 -30.46

DISTANCES

COTES

-30.46 -14.37

DISTANCES

COTES

-14.37 2.13

DISTANCES

COTES

2.13 14.20

DISTANCES

COTES

14.20 28.81

186.91 28.81

ASSISE	DISTANCES	DISTANCES		COTES
		PROJECT	COTES	
188.98	-16.27	190.61	-22.34	
		190.61	-18.34	
		189.71	-17.00	
		189.21	-16.50	
		189.71	-16.00	
		189.75	-15.50	
			-14.50	
189.09	-12.00	189.84	-12.00	
		189.84	-12.00	
		189.75	-12.00	
		189.71	-12.00	
189.35	-1.50	190.10	-1.50	
189.39	0.00	190.14	0.00	
189.35	1.50	190.10	1.50	
189.09	12.00	189.84	12.00	
188.96	16.99	189.75	14.50	
		189.71	15.50	
		187.12	20.69	


PROFIL 124

G2,PIS

S = 2950.00
ZTN = 189.644
ZPRD= 190.211

EUCHS=1/
ECHZ=1/
PC = 184,0

LICENCE : 1570

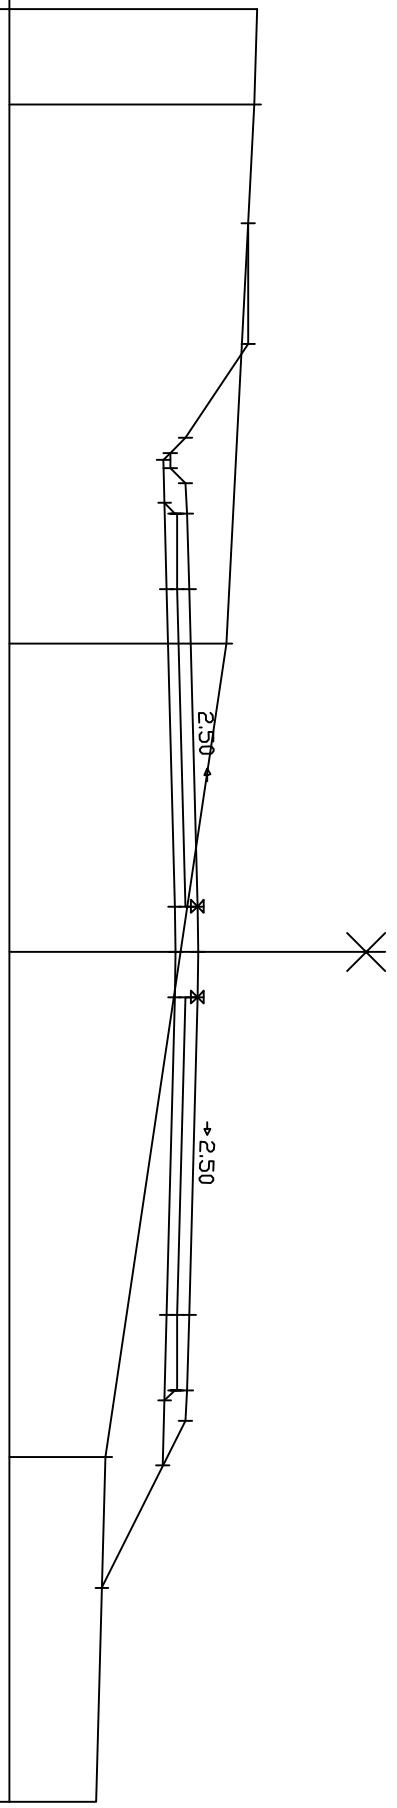


PROFIL 125

G2PIS

S = 2975.000
 ZTN = 190.212
 ZR0= 190.182


ECHS=1/
 ECHZ=1/
 PC = 184.0
 LICENCE , 1570

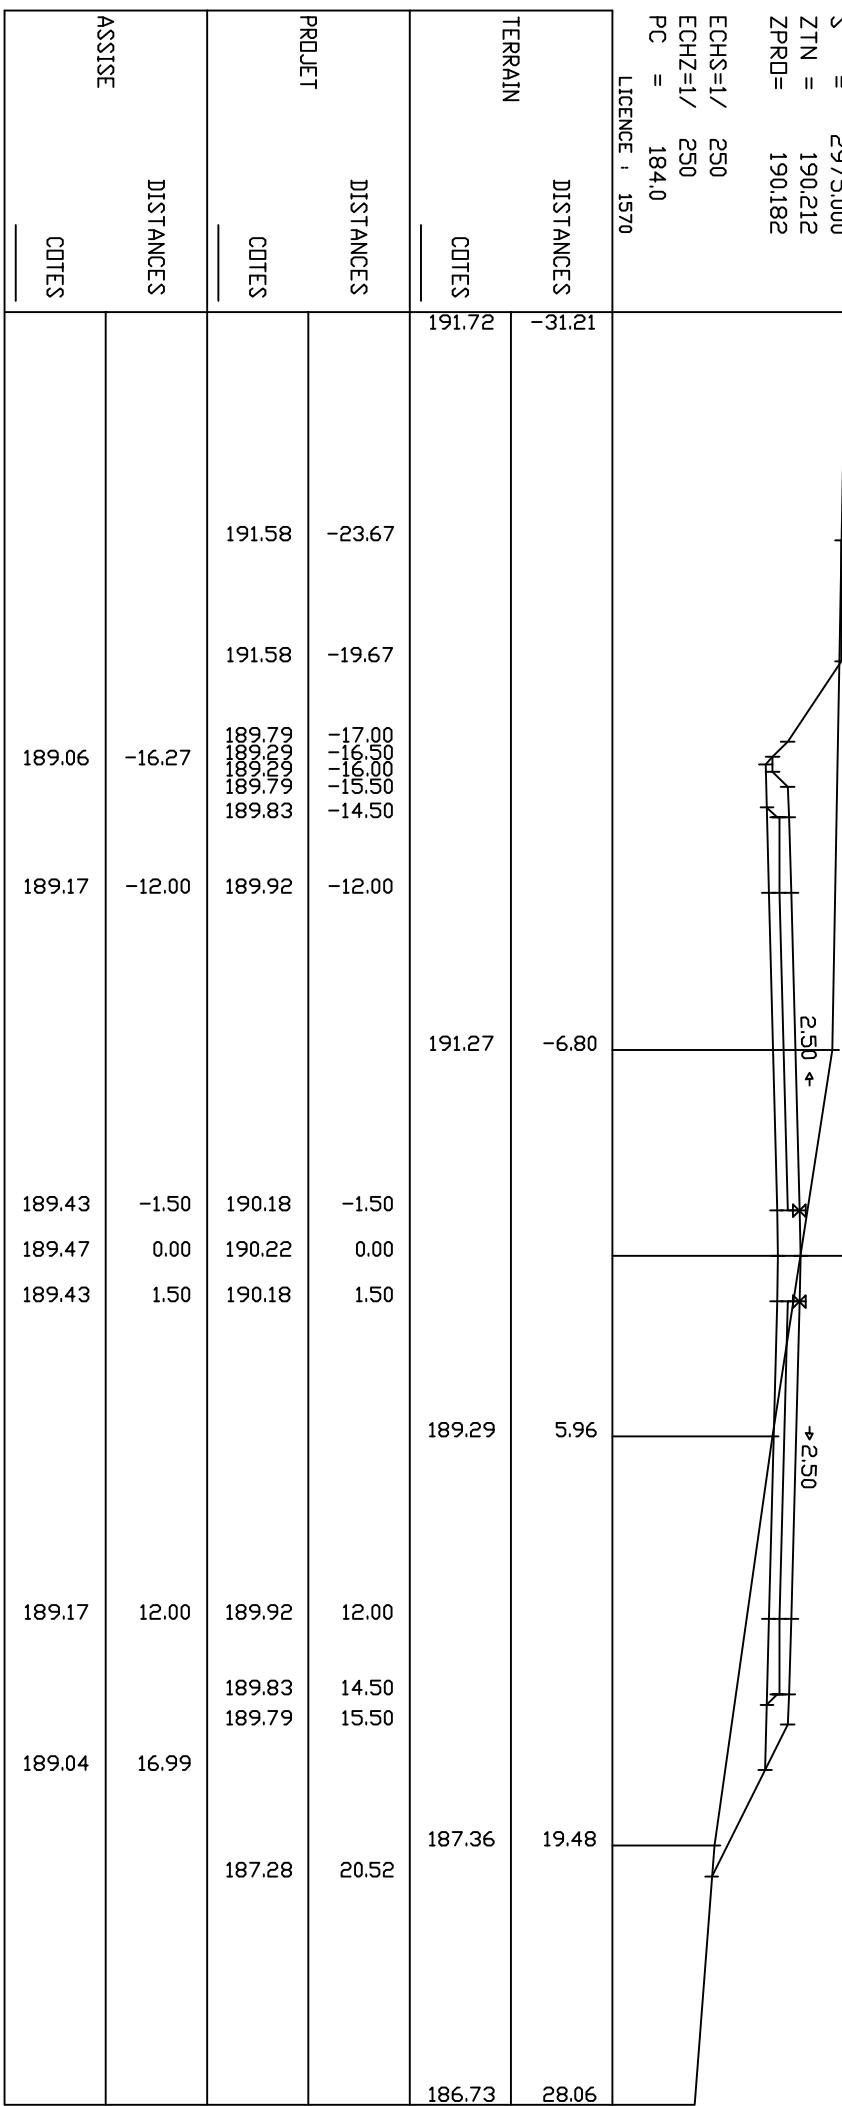

PROFIL 126

G2,PIS


S = 3000.000
 ZTN = 190.517
 ZPRD= 190.005
 ECHS=1/ 250
 ECHZ=1/ 250
 PC = 185.0
 LICENCE , 1570

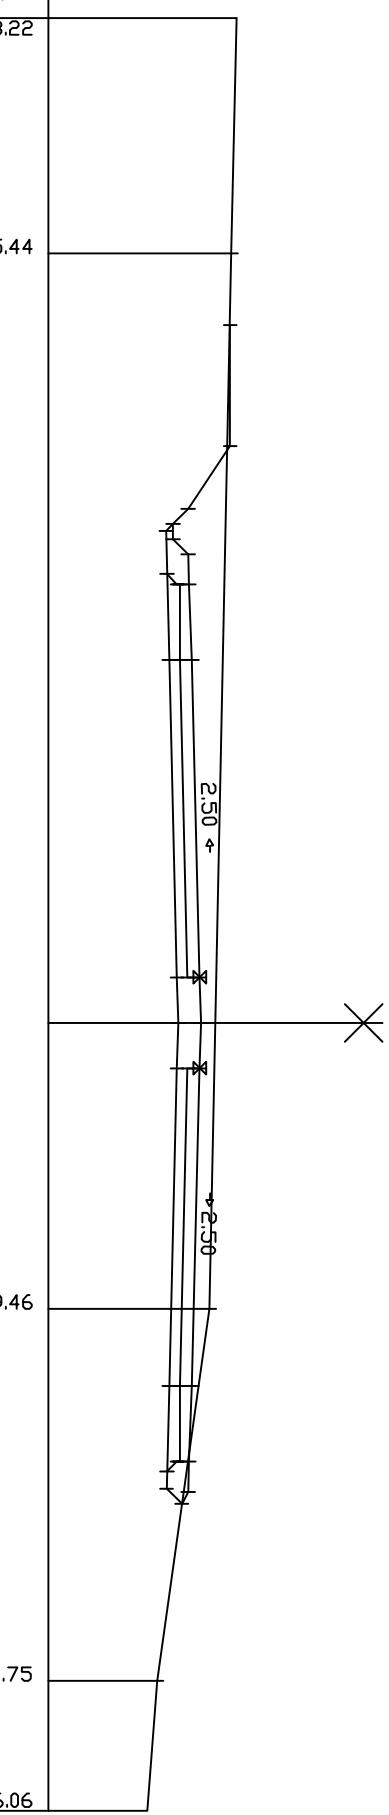


PROFIL 127

G2.PIS

S = 3025.000
ZTN = 189.354
ZPRO = 189.678

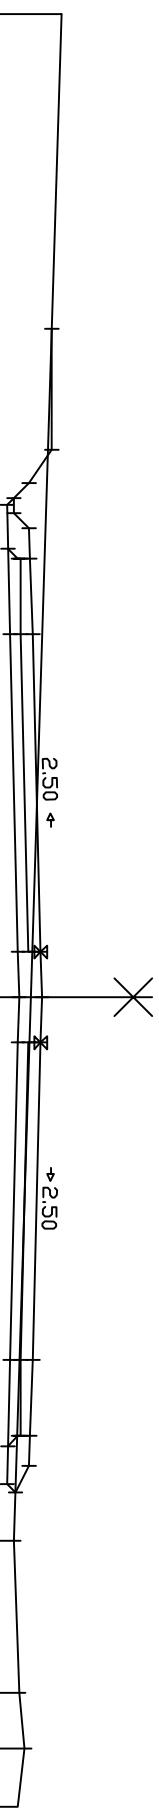

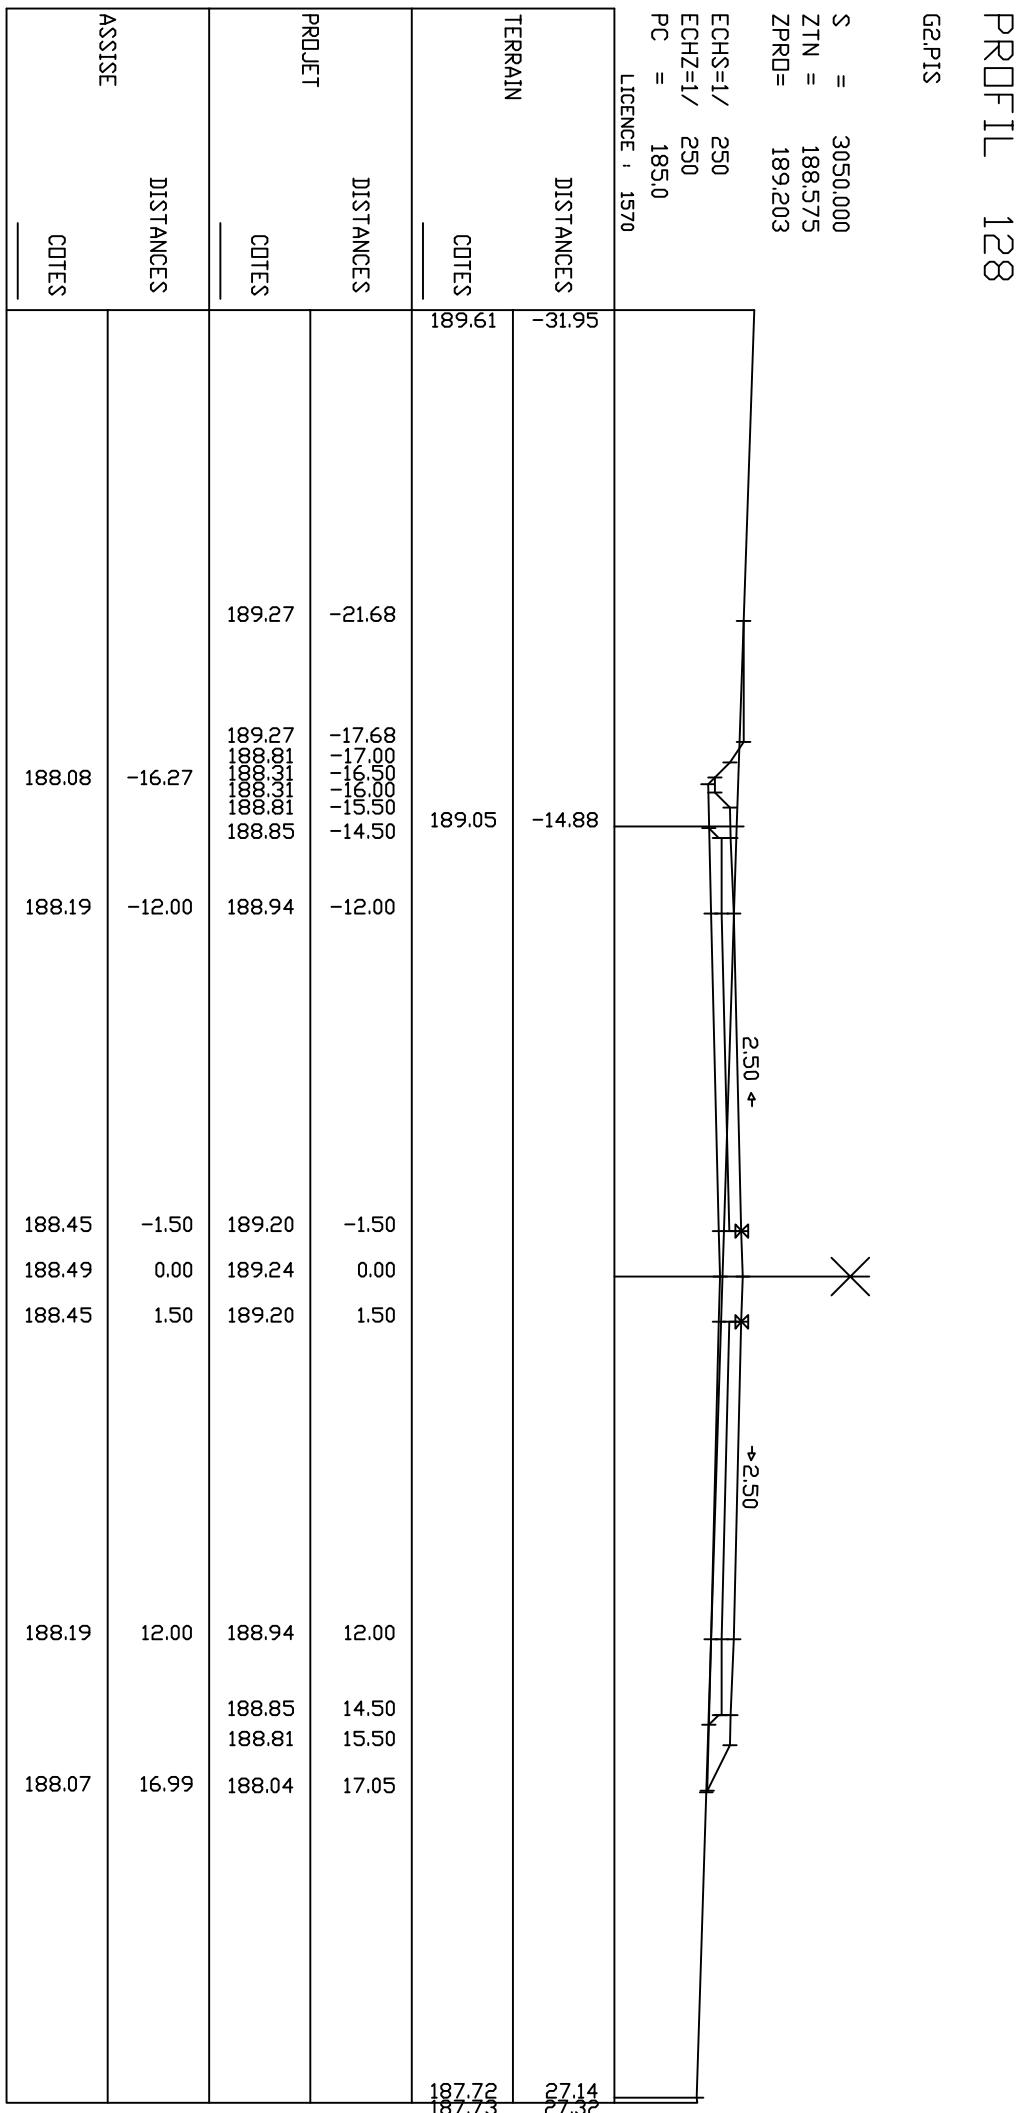


PROFIL 129


G2PIS

S = 3075.000
 ZTN = 187.571
 ZPRO= 188.589

ECHS=1/
 ECHZ=1/
 PC = 184.0
 LICENCE , 1570

ASSISE	DISTANCES	DISTANCES		TERRAIN	DISTANCES	COTES
		PROJECT	COTES			
187.47	-16.27	188.47 188.20 187.70 187.70 188.20 188.24	188.47 -21.41		188.89 -31.27	
187.58	-12.00	188.33	-12.00			
187.84	-1.50	188.59	-1.50			
187.88	0.00	188.63	0.00			
187.84	1.50	188.59	1.50			
187.58	12.00	188.33	12.00			
187.45	16.99	188.24 188.20 186.88	14.50 15.50 18.14	186.90 186.80 28.00	16.03	

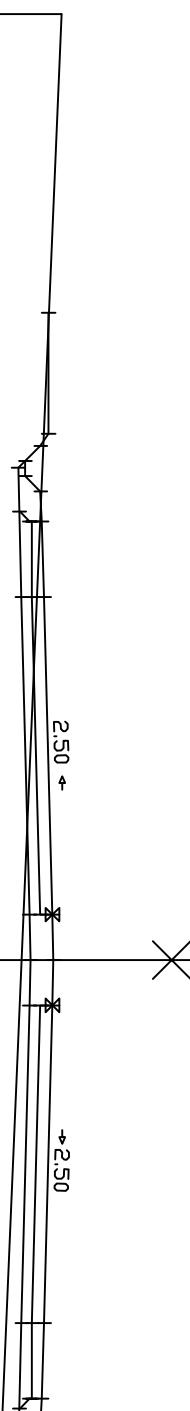

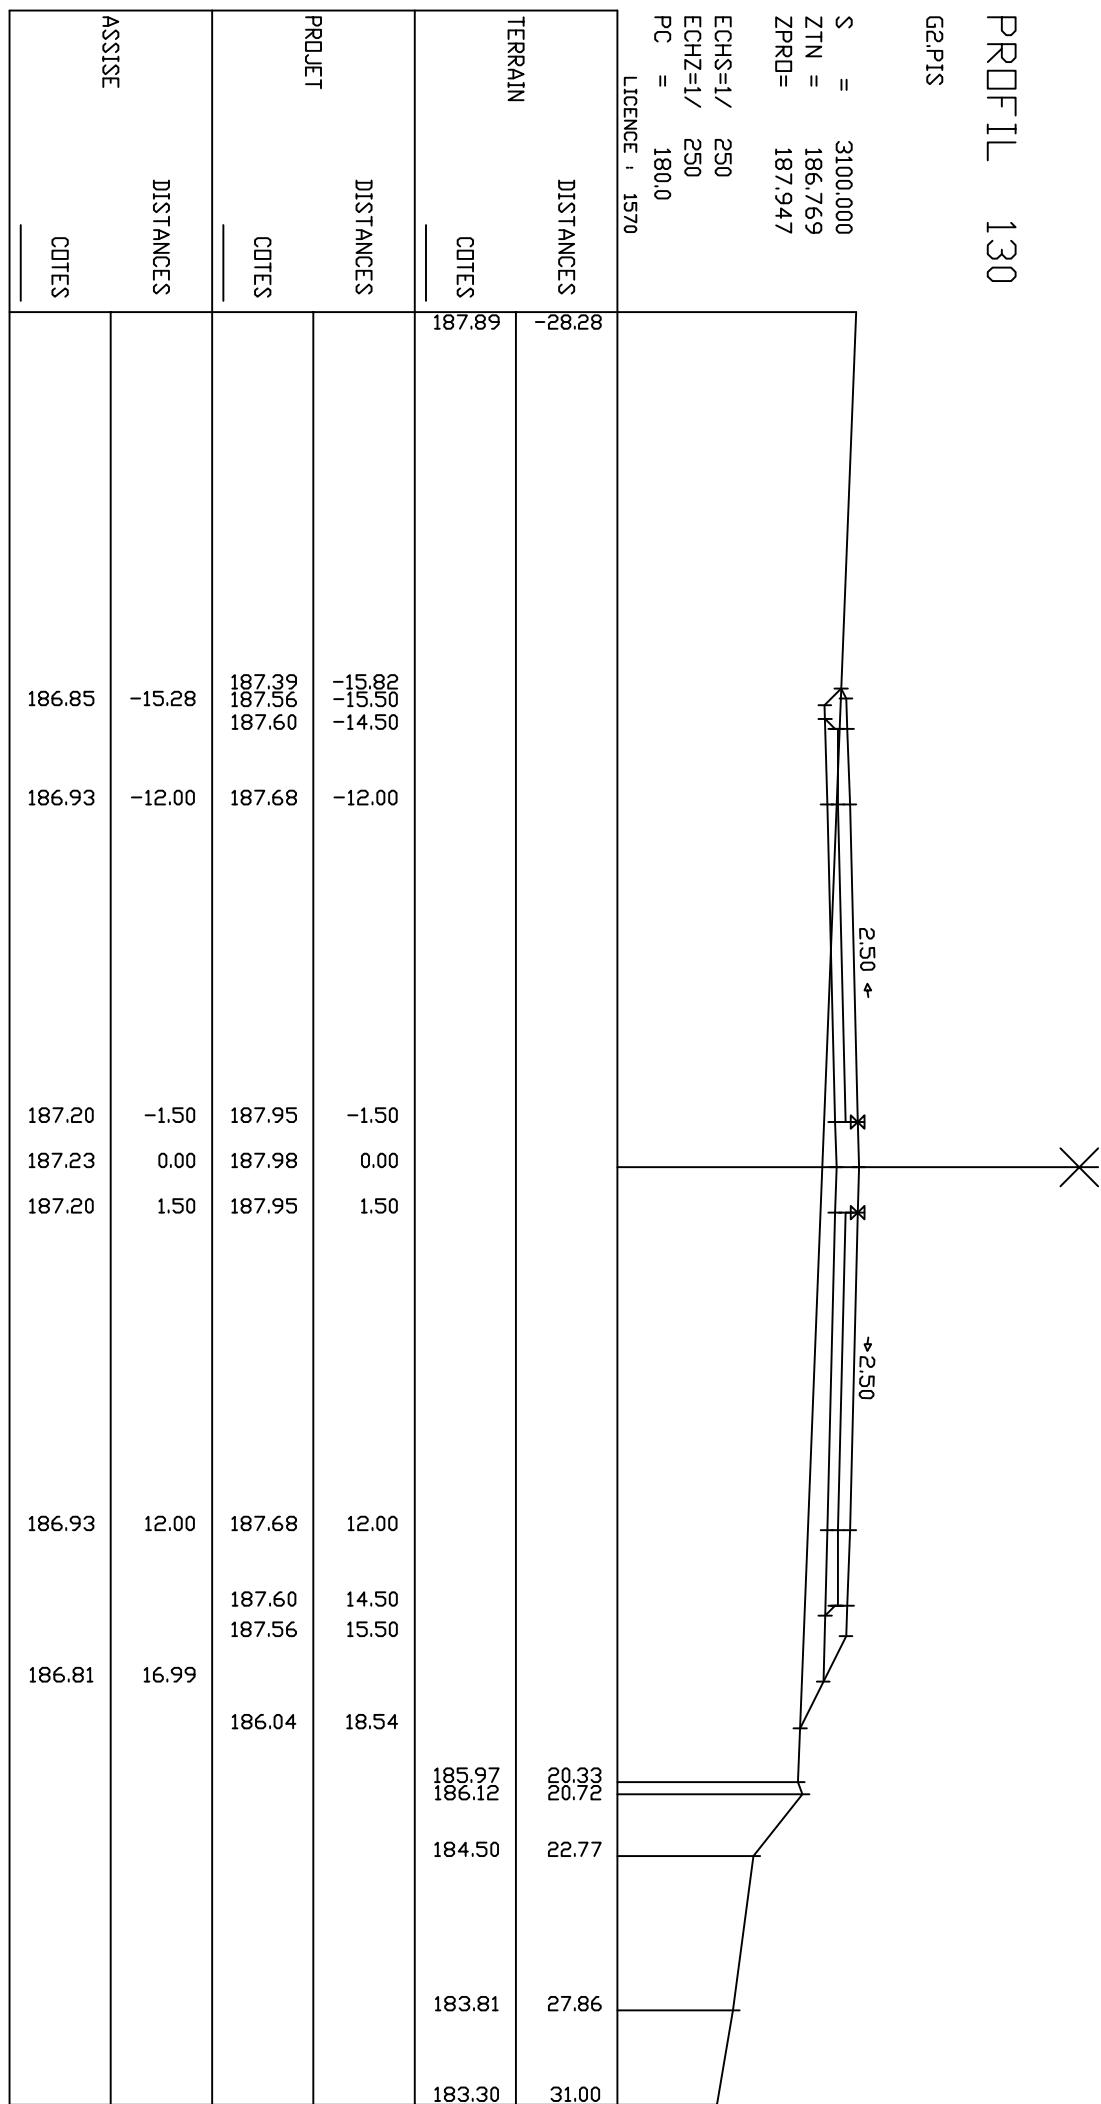


G2,PIS

S	=	3125.000
ZTN	=	185.659
ZPRD	=	187.304

LICHS=1/ 250
ECHZ=1/ 250
PC = 179.0


LICENCE : 1570

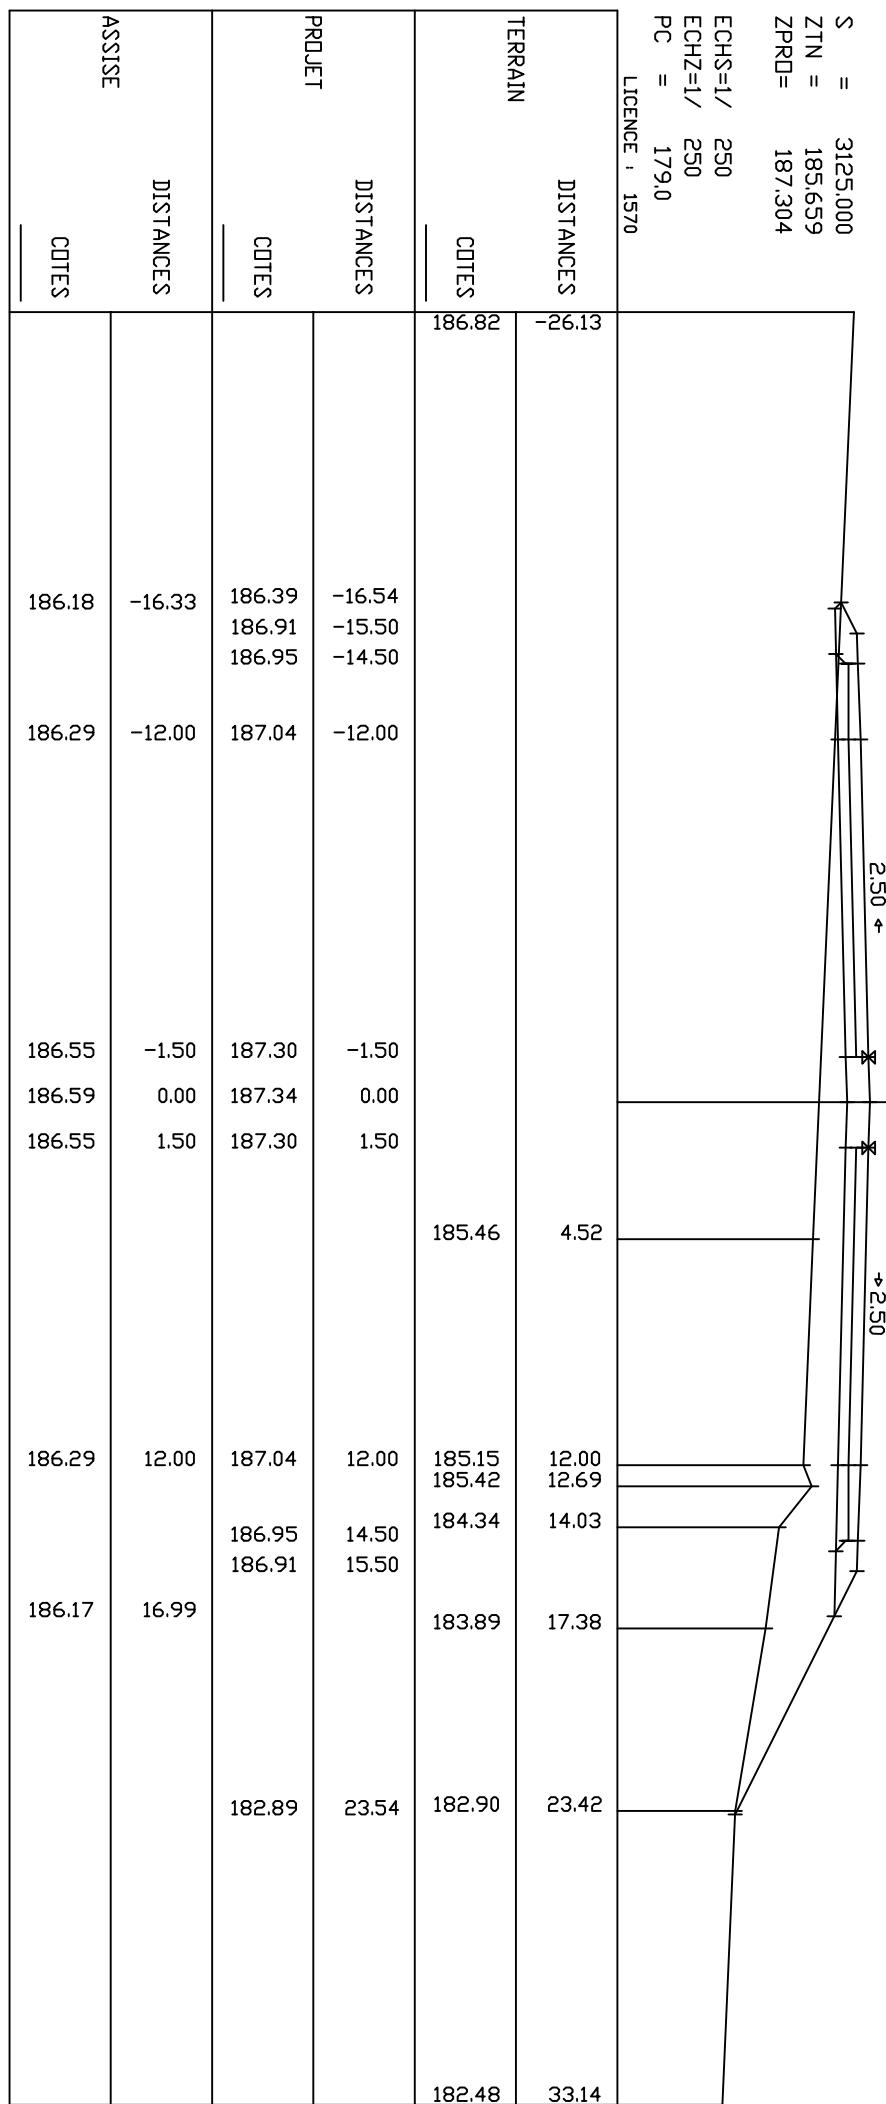

PROFIL 132

G2,PIS

S	=	3150.000
ZTN	=	184.809
ZPRO	=	186.662
ECHS=1/	250	
ECHZ=1/	250	
PC	=	180.0
LICENCE	,	1570

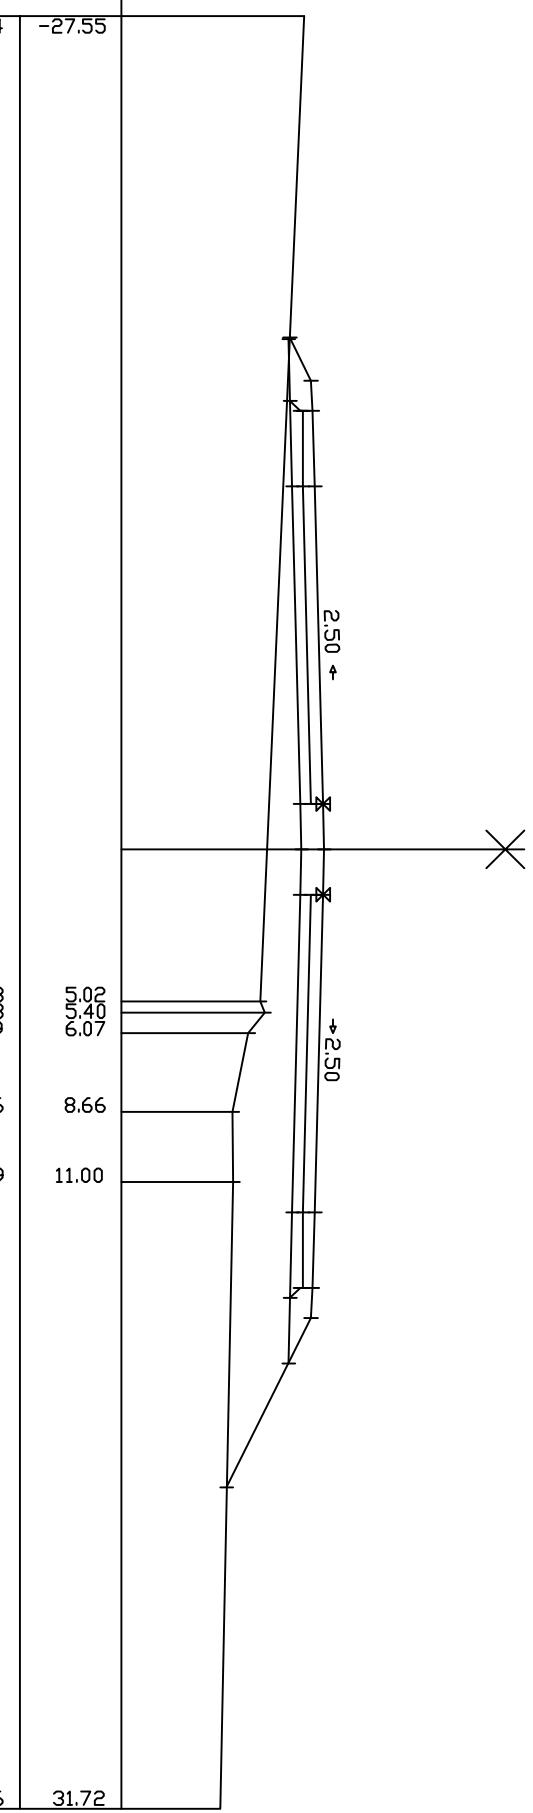


		DISTANCES		TERRAIN		PC = 180.0 LICENCE : 1570	
		COTES		DISTANCES		COTES	
		PROJECT		COTES		PROJECT	
ASSISE	COTES	DISTANCES	COTES	DISTANCES	COTES	DISTANCES	COTES
185.53	-16.88	185.56	-16.92			186.04	-27.55
		186.27	-15.50				
		186.31	-14.50				
185.65	-12.00	186.40	-12.00				
185.91	-1.50	186.66	-1.50				
185.95	0.00	186.70	0.00				
185.91	1.50	186.66	1.50				
						184.58 184.73 184.19	5.02 5.40 6.07
						183.66	8.66
						183.69	11.00
185.65	12.00	186.40	12.00				
		186.31	14.50				
		186.27	15.50				
185.52	16.99	183.48	21.09				
						183.26	31.72

ASSISE COTES	DISTANCES COTES	TERRAIN		DISTANCES COTES	DISTANCES COTES	DISTANCES COTES	DISTANCES COTES	DISTANCES COTES	DISTANCES COTES
		PROJET	ASSISE						
184.88	-16.99	184.81	-17.13		185.35	-28.34			
		185.63	-15.50						
		185.67	-14.50						
185.01	-12.00	185.76	-12.00						
185.27	-1.50	186.02	-1.50		184.19	-4.10			
185.29	-0.53	186.04	-0.53		184.06	-1.17			
					184.04	-1.15			
185.27	1.50	186.02	1.50		183.43	1.82			
					183.46	4.50			
185.15	12.00	185.90	12.00						
		185.81	14.50						
		185.77	15.50						
185.09	16.86	183.65	19.73						
					183.80	30.94			

PRØFIL 133
G2PIS

S = 3175.000
ZTN = 183.808
ZPRO= 186.020

ECHS=1/
ECHZ=1/
PC = 180.0
LICENCE , 1570

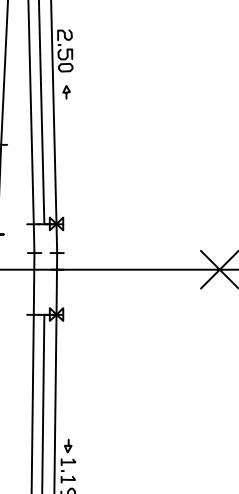


PROFIL 134

G2PIS

S = 3200.000
 ZTN = 184.449
 ZPRO= 185.377


ECHS=1/
 ECHZ=1/
 PC = 181.0
 LICENCE , 1570

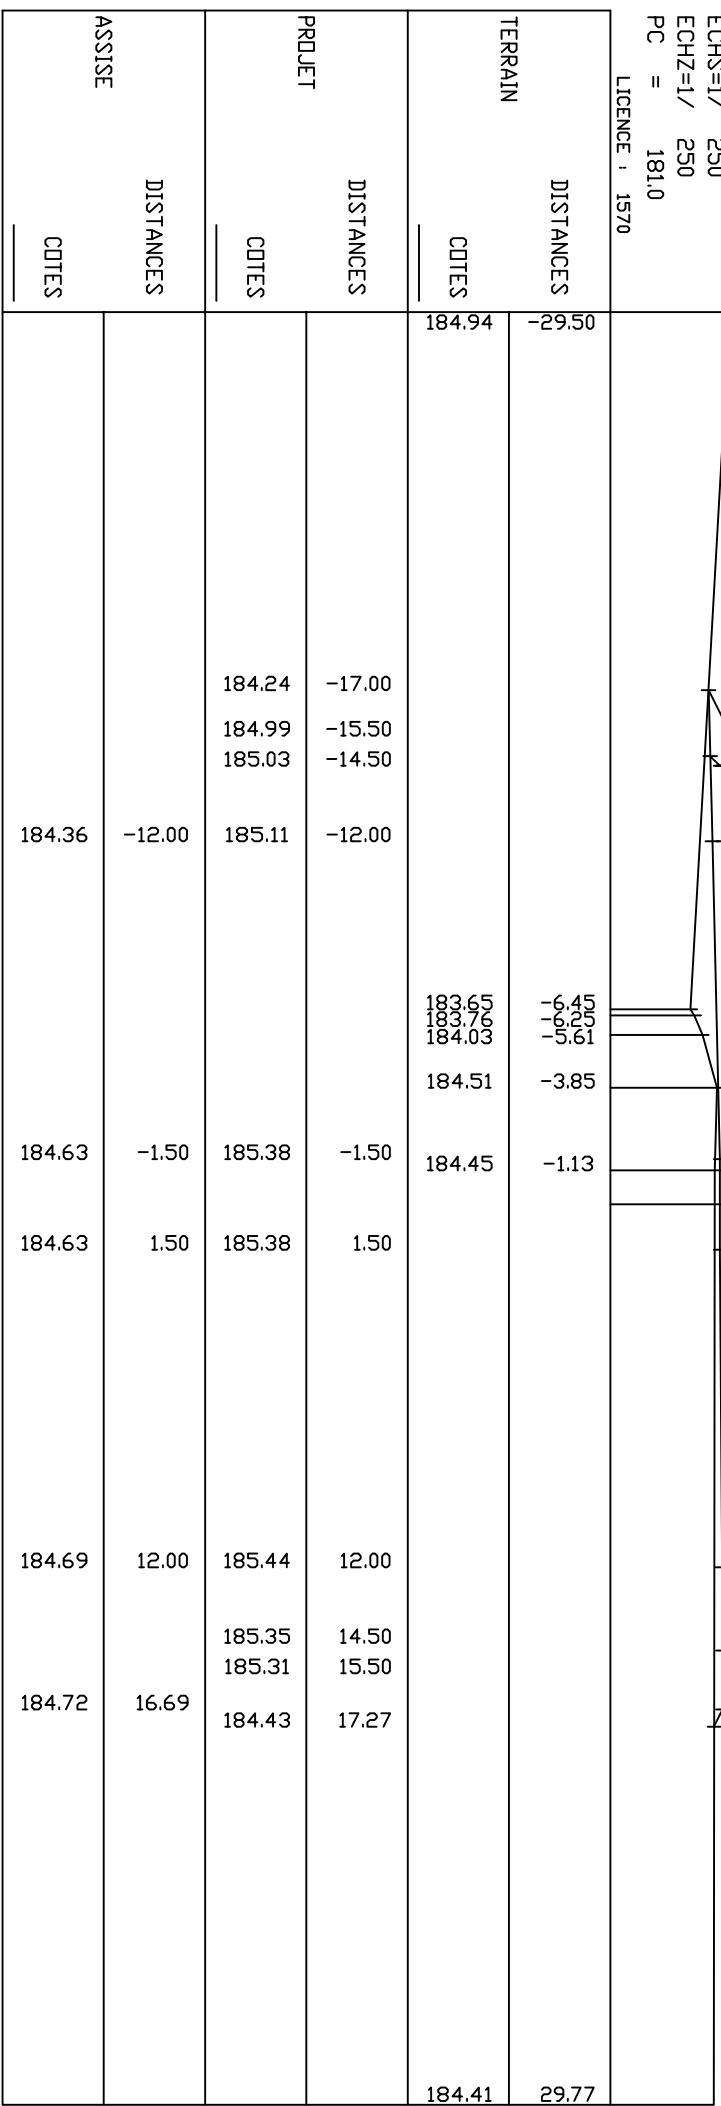

PROFIL 135

G2,PIS

S = 3202.828
ZTN = 184.414
ZPRD= 185.304

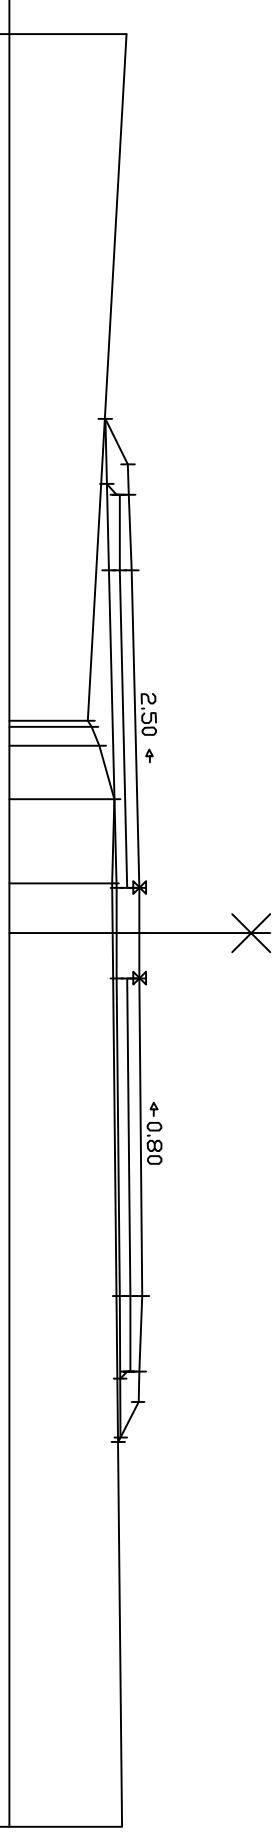


PROFIL 136

G2PIS

S = 3223.008
 ZTN = 184.001
 ZPRO= 184.786

ECHS=1/
 ECHZ=1/
 PC = 180.0

LICENCE , 1570

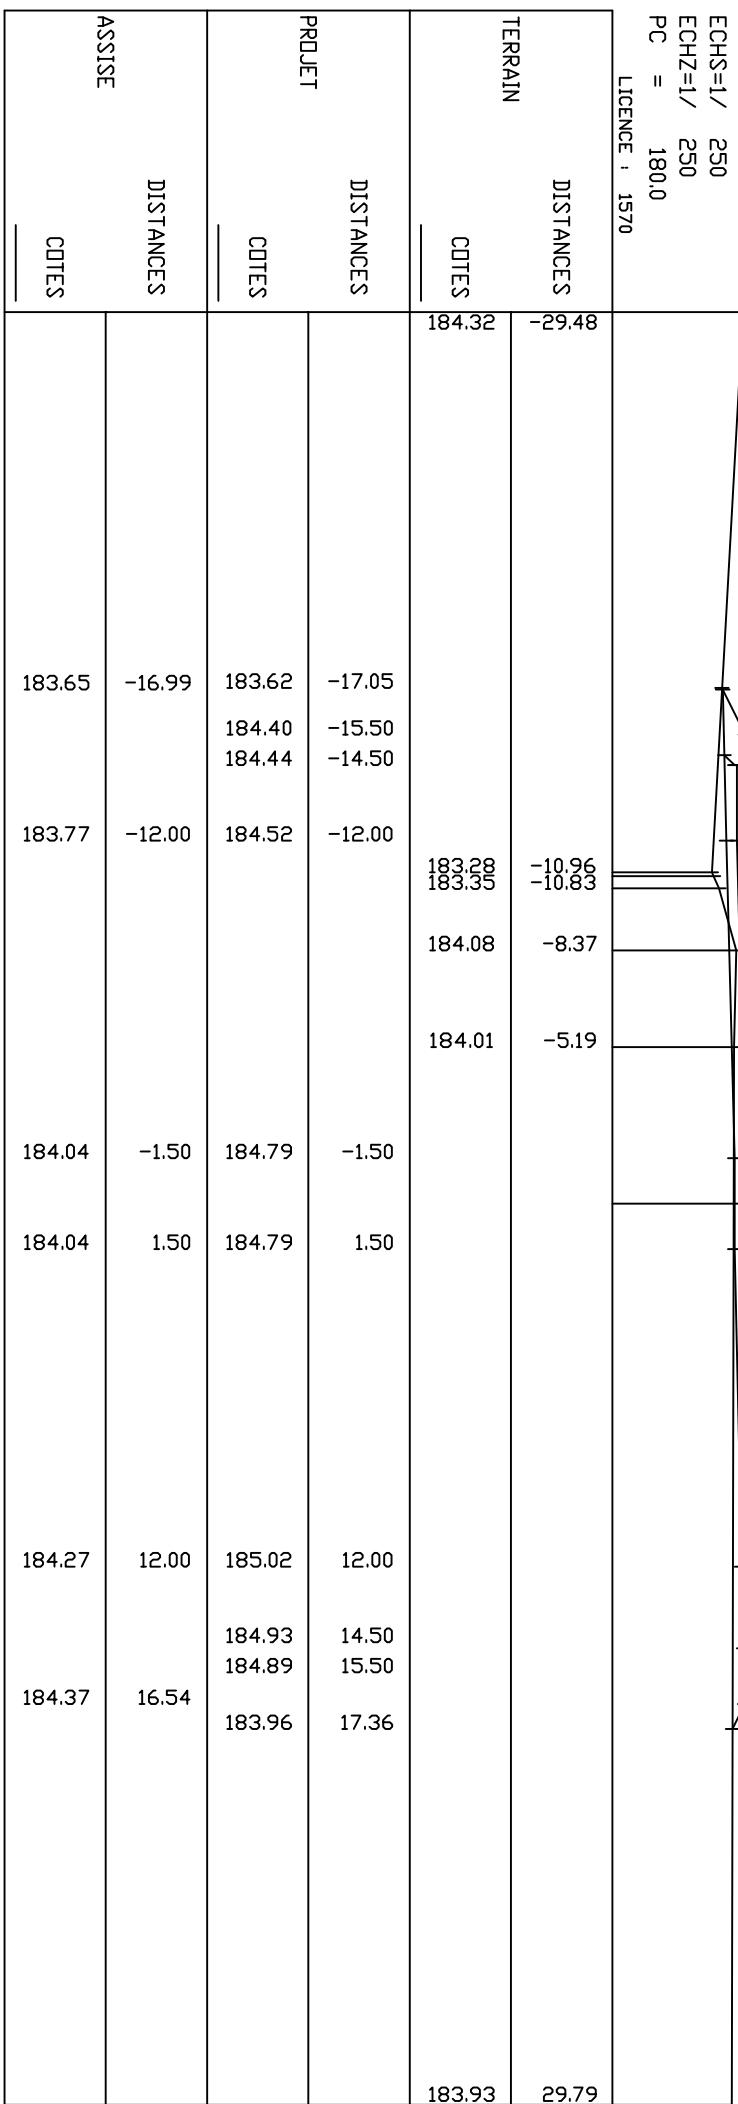



PROFIL 137

G2PIS

S = 3225.000
 ZTN = 183.925
 ZPRO= 184.735

ECHS=1/
 ECHZ=1/
 PC = 180.0
 LICENCE , 1570

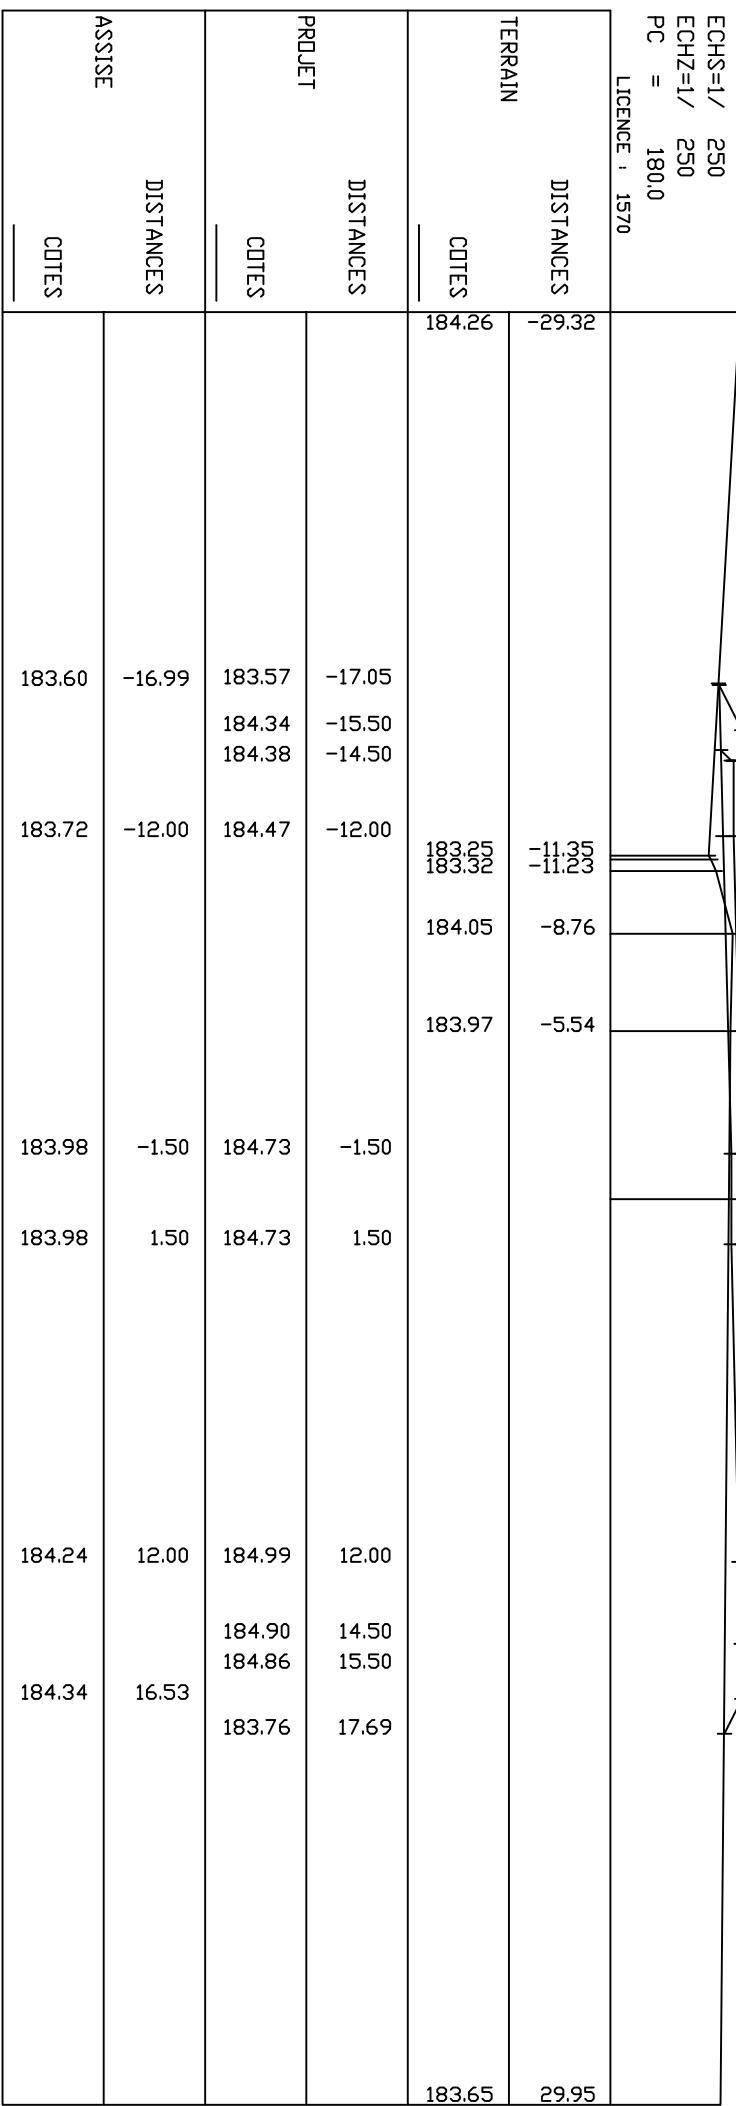

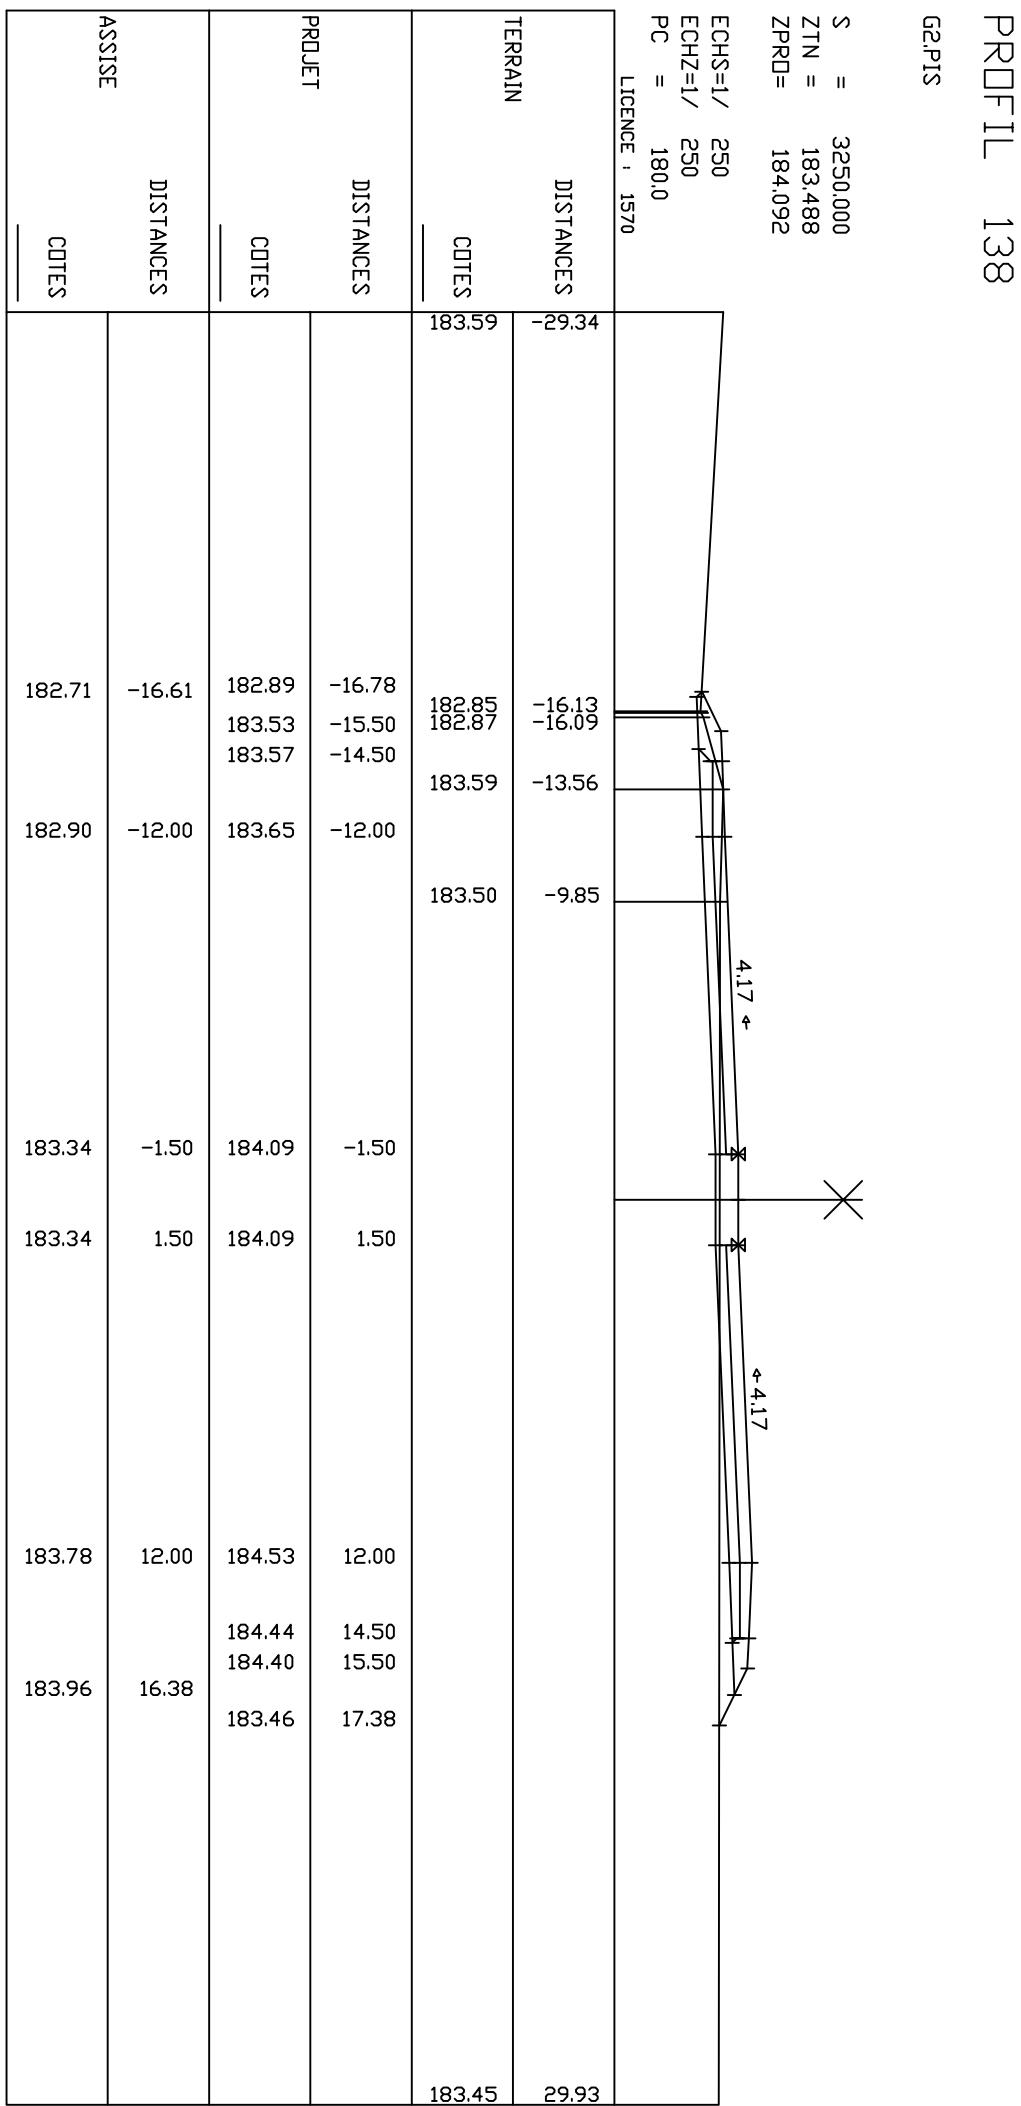


PROFIL 139

G2PIS

S = 3275.000
 ZTN = 182.710
 ZPRO= 183.450

ECHS=1/
 ECHZ=1/
 PC = 179.0
 LICENCE , 1570

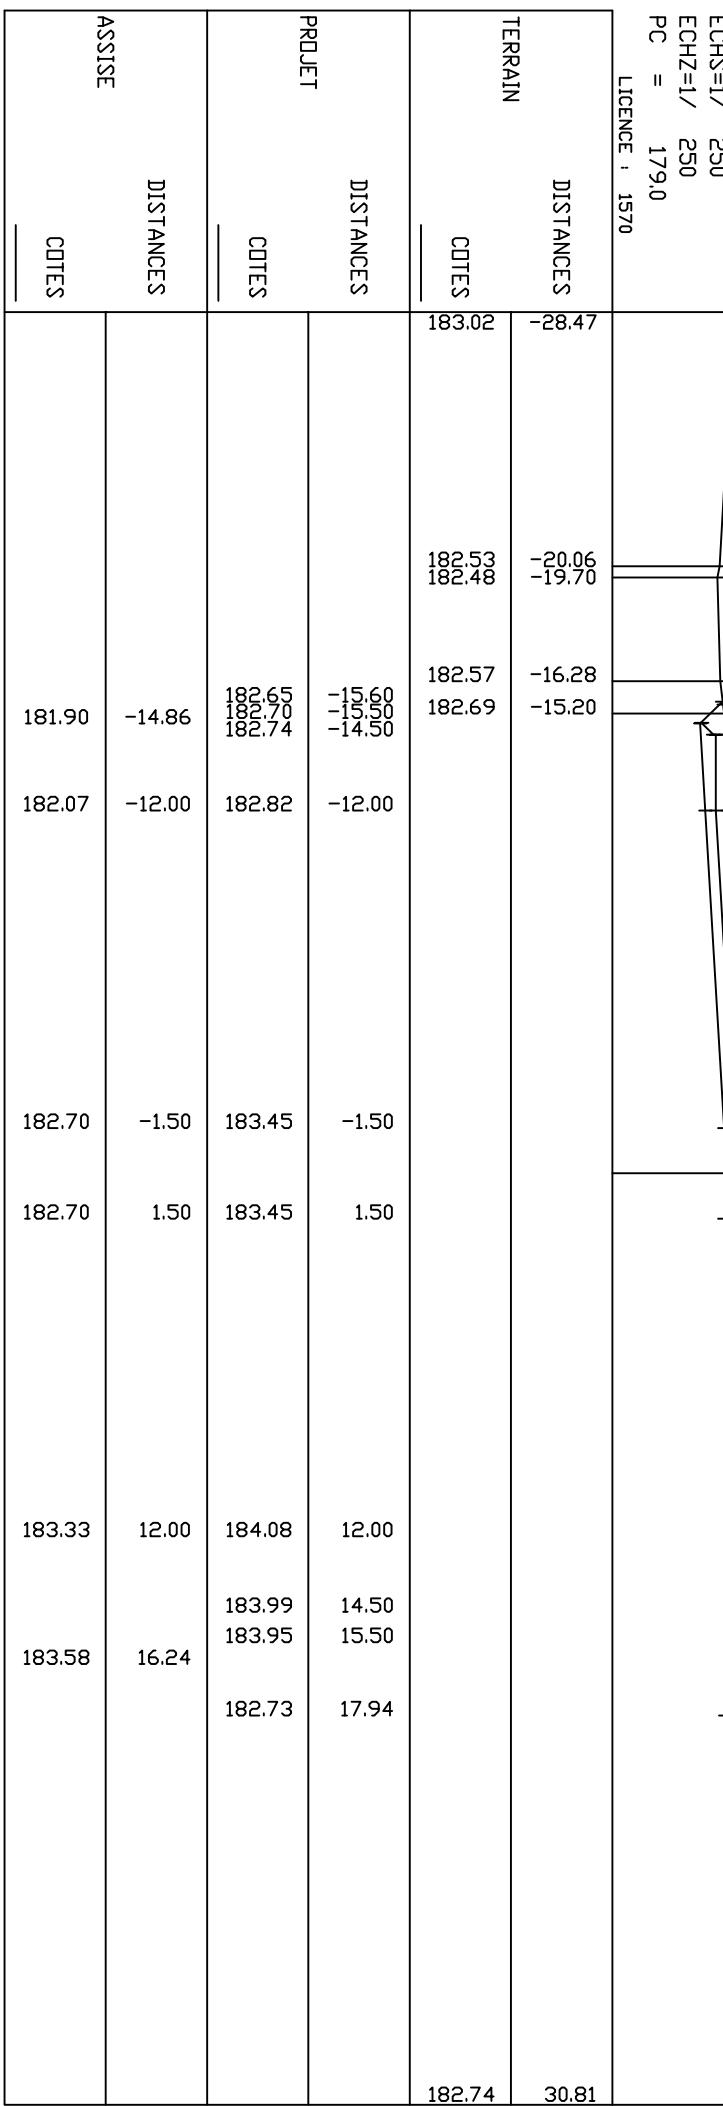

PROFIL 140

G2PIS

S = 3289.608
 ZTN = 182.420
 ZPRO= 183.074

ECHS=1/
 ECHZ=1/
 PC = 178.0
 LICENCE , 1570

TERRAIN

DISTANCES

COTES

182.97 -31.17

DISTANCES

COTES

182.41 -21.67

DISTANCES

COTES

182.28 -20.82

DISTANCES

COTES

182.35 -17.83

DISTANCES

COTES

182.47 -16.88

DISTANCES

COTES

182.34 -7.00

DISTANCES

COTES

182.34 28.11


ASSISE	DISTANCES	COTES		
			PROJECT	COTES
181.30	-16.09	182.34	-21.18	182.41 182.28
		182.34 182.21 181.71 181.71 182.25	-17.18 -17.00 -16.50 -16.00 -14.50	182.35 182.47
181.59	-12.00	182.34	-12.00	
182.32	-1.50	183.07	-1.50	
182.32	1.50	183.07	1.50	
183.06	12.00	183.81	12.00	
183.35	16.16	183.72 183.68 182.37	14.50 15.50 18.13	

PROFIL 141

G2PIS

S = 3300.000
 ZTN = 182.244
 ZPRO= 182.807

ECH\$=1/
 ECHZ=1/
 PC = 250
 LICENCE , 178.0
 1570

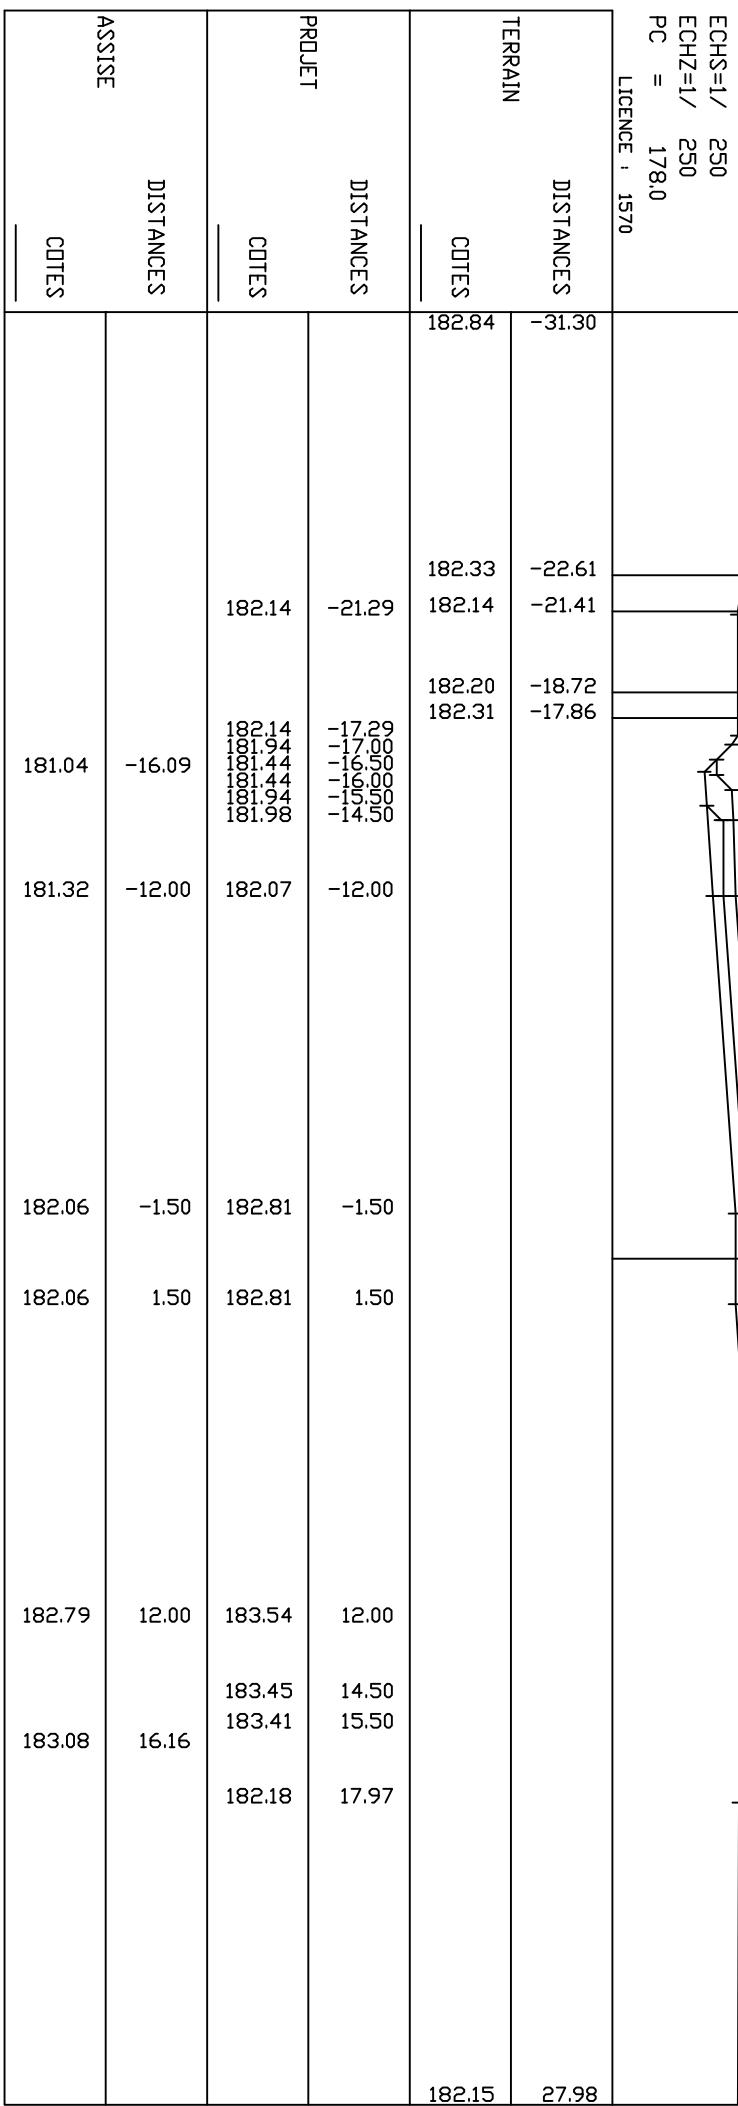


PROFIL 142

G2PIS

S = 3325.000
 ZTN = 180.621
 ZPRO= 182.165

ECHS=1/
 ECHZ=1/
 PC = 250
 LICENCE , 177,0
 1570

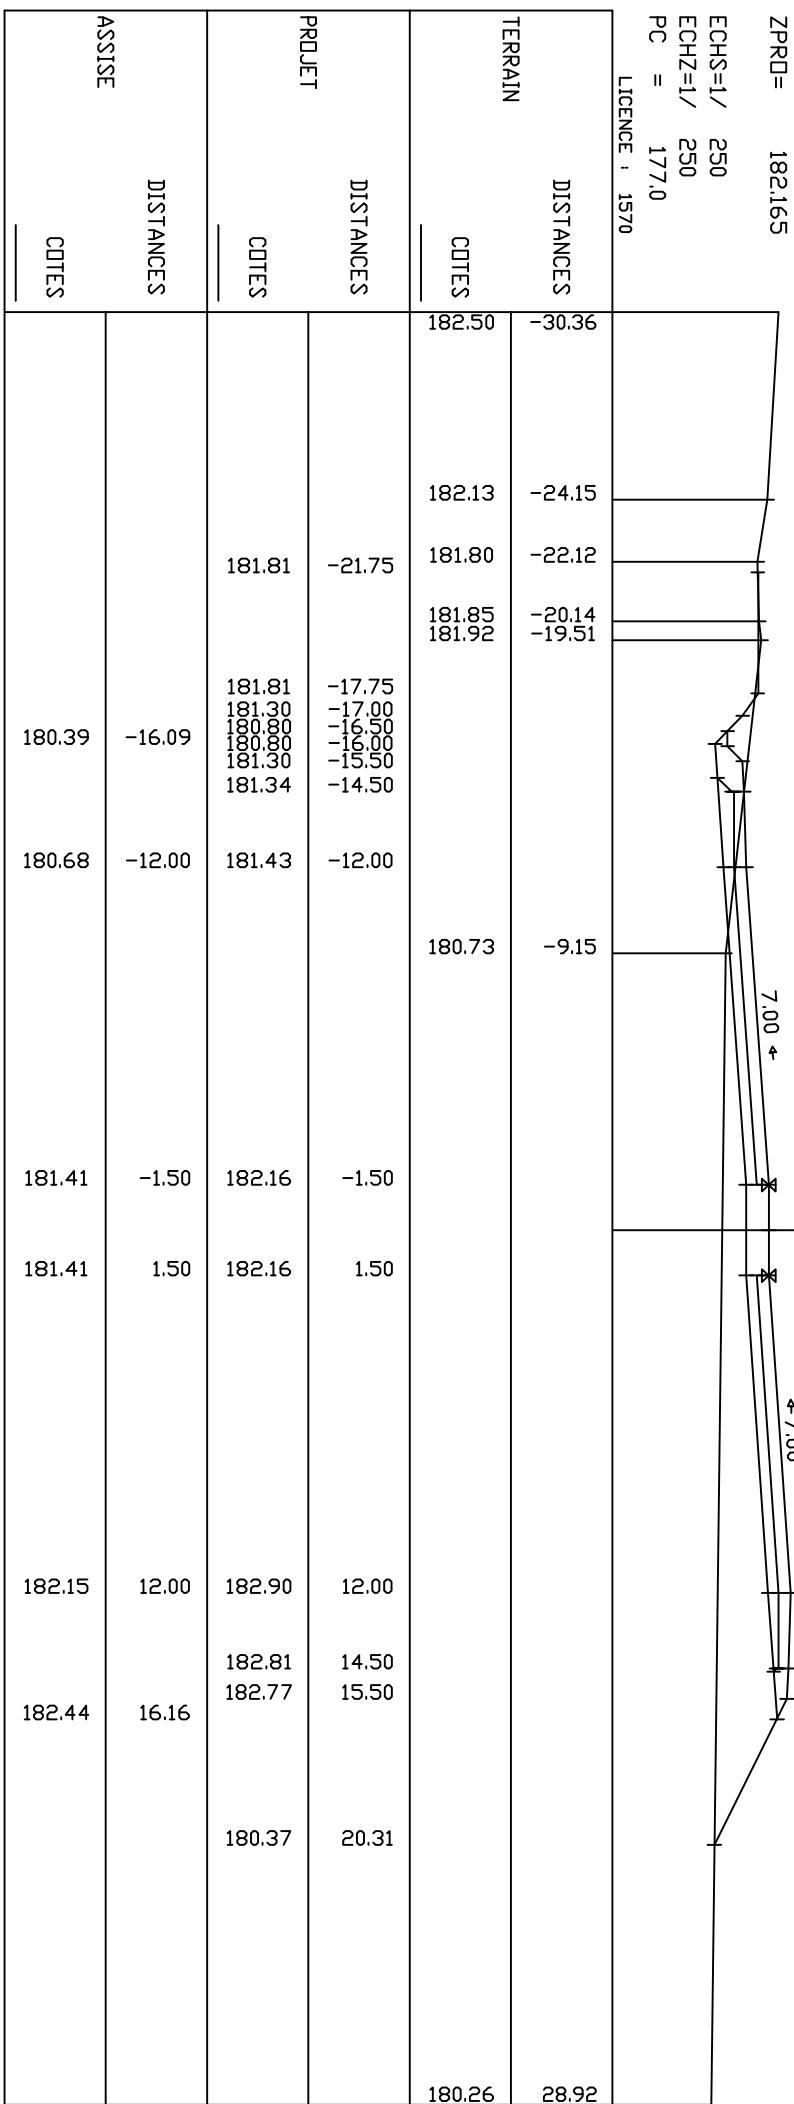


PROFIL 143

G2PIS

S = 3350.000
 ZTN = 180.305
 ZPRO= 181.523


ECHS=1/
 ECHZ=1/
 PC = 177,0
 LICENCE , 1570

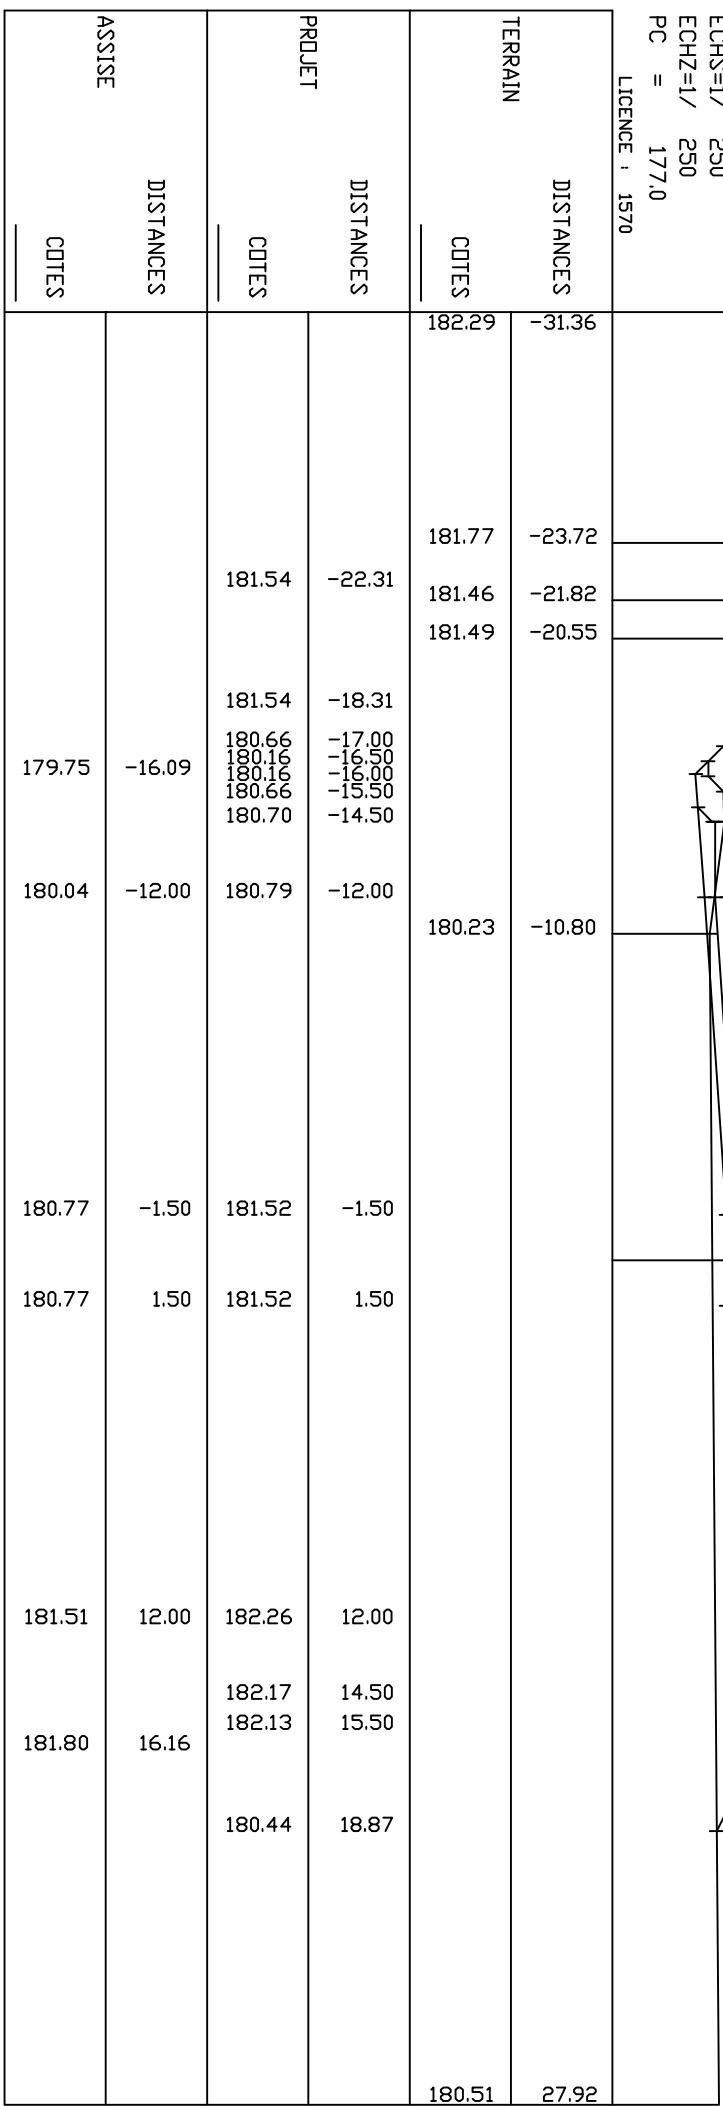

PROFIL 144

G2,PIS


S = 33/5.000
ZTN = 179.652
ZPRO = 180.880

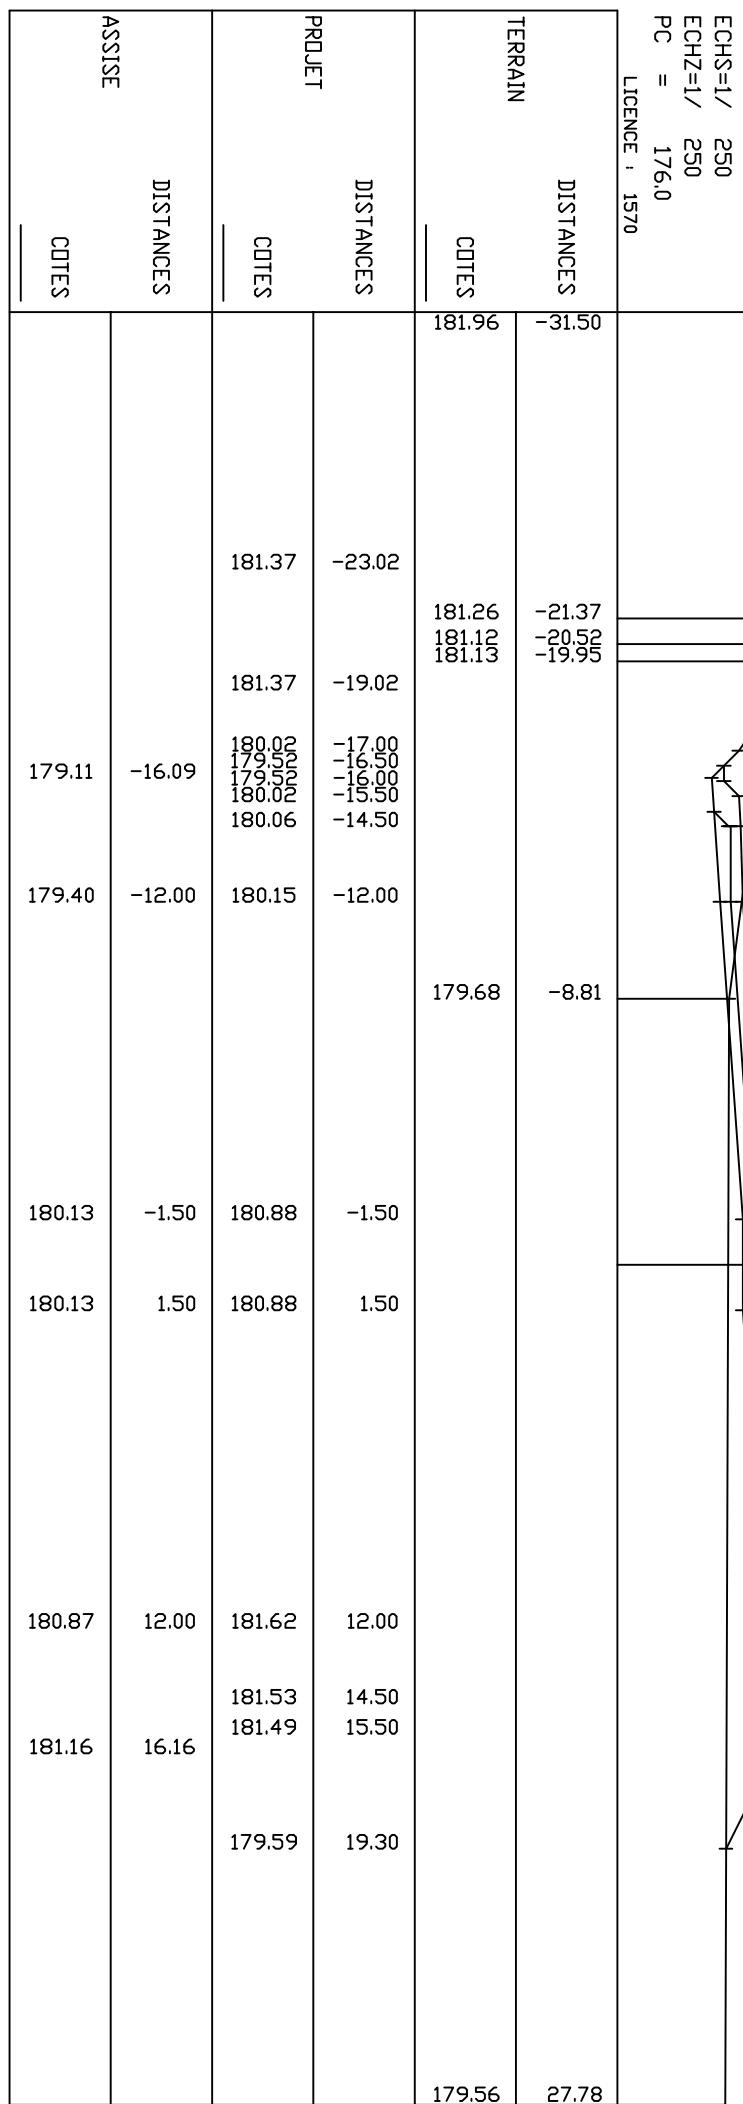

PROFIL 145

G2,PIS

S = 3400.000
 ZTN = 179.388
 ZPRO= 180.238
 ECHS=1' 250
 ECHZ=1' 250
 PC = 175.0
 LICENCE , 1570

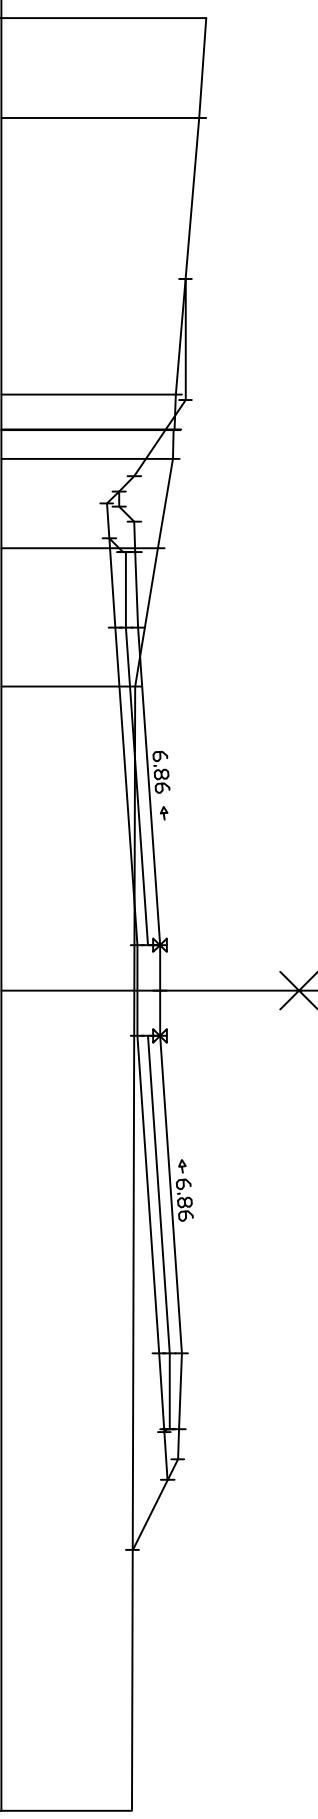

ASSISE		DISTANCES		TERRAIN	
COTES	DISTANCES	COTES	DISTANCES	COTES	DISTANCES
178.49	-16.10	181.08	-23.53	181.77	-32.10
		181.08	-19.53	181.54	-28.80
		179.39	-17.00		
		178.89	-16.50		
		178.89	-16.00		
		179.39	-15.50		
		179.43	-14.50		
178.77	-12.00	179.52	-12.00	180.76	-19.70
				180.71	-18.50
				180.70	-18.50
				180.68	-17.50
179.49	-1.50	180.24	-1.50	180.18	-14.60
179.49	1.50	180.24	1.50	179.42	-10.00
180.21	12.00	180.96	12.00		
180.49	16.17	180.87	14.50		
		180.83	15.50		
		179.33	18.49		
				179.31	27.10

PROFIL 146

G2PIS

S = 3425.000
 ZTN = 178.739
 ZPRO= 179.595

ECHS=1/
 ECHZ=1/
 PC = 250
 LICENCE , 175.0
 1570

TERRAIN DISTANCES

COTES

		181.02	-31.87
		180.30	-23.64
		180.05	-16.97
		179.99	-16.83
		179.82	-11.15
		179.42	-8.77
		178.81	-5.08
		178.36	27.40

DISTANCES

COTES

PROJET

COTES

DISTANCES

ASSISE

COTES


ASSISE			
DISTANCES			
COTES			
178.10	-16.17	178.93 178.43 178.43 178.93 178.97	180.28 -23.01 180.28 -19.01 180.28 -17.00 -16.50 -16.00 -15.50 -14.50
178.31	-12.00	179.06	179.06 -12.00 179.82 179.42 178.81
178.85	-1.50	179.60	179.60 -1.50 179.60 1.50
178.85	1.50	179.60	179.60 1.50
179.38	12.00	180.13	180.13 12.00
179.60	16.31	180.04 180.00	180.04 14.50 180.00 15.50 178.48 18.53

PROFIL 147

G2PIS

S = 3437.369
 ZTN = 178.507
 ZPRO= 179.277

ECHS=1/
 ECHZ=1/
 PC = 175.0
 LICENCE , 1570

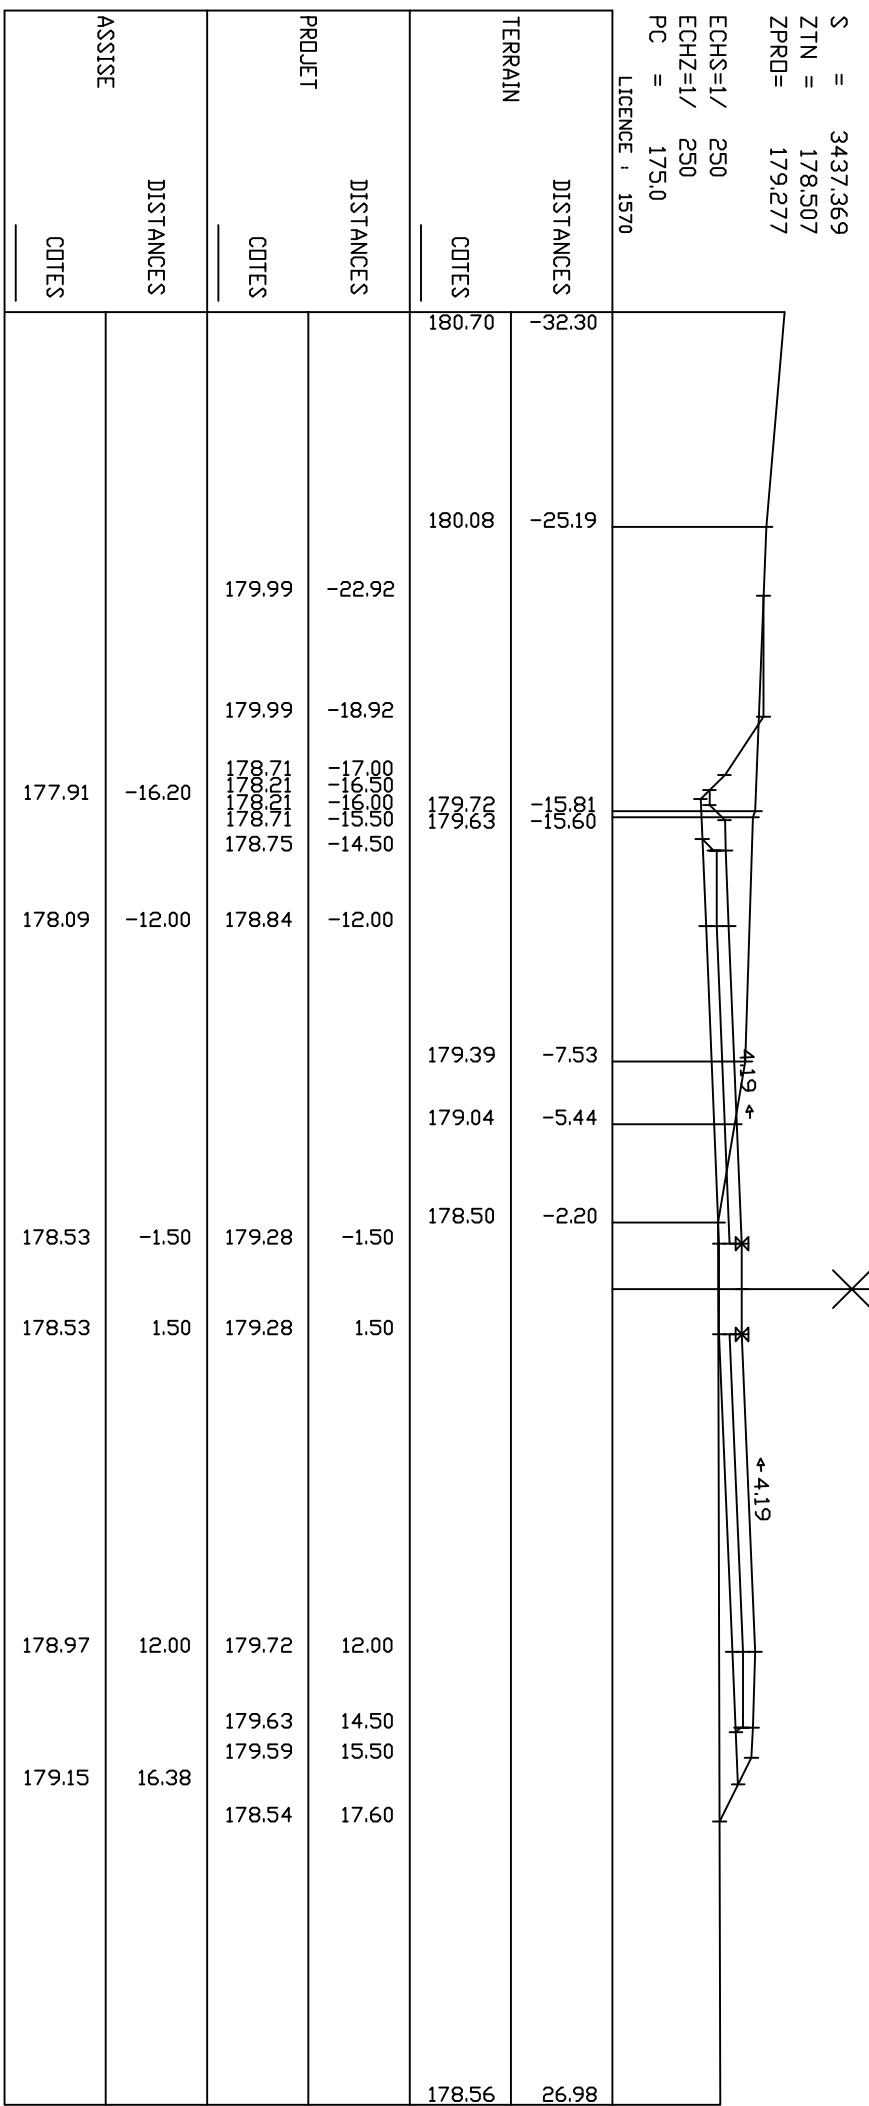

PROFIL 148

G2PIS

S = 3450.000
 ZTN = 178.355
 ZPRO= 178.953

ECHS=1/
 ECHZ=1/
 PC = 175.0
 LICENCE , 1570

TERRAIN

DISTANCES

COTES

180.13 -32.08

DISTANCES

COTES

179.85 -26.77

DISTANCES

COTES

179.80 -26.56

DISTANCES

COTES

179.71 -17.00

DISTANCES

COTES

179.71 -16.00

DISTANCES

COTES

178.48 -16.00

DISTANCES

COTES

177.98 -15.50

DISTANCES

COTES

178.48 -14.50

DISTANCES

COTES

178.52 -14.50

DISTANCES

COTES

DISTANCES

COTES

178.61 -12.00

DISTANCES

COTES

DISTANCES

COTES

178.95 -12.00

DISTANCES

COTES

DISTANCES

COTES

178.95 -1.50

DISTANCES

COTES

DISTANCES

COTES

178.95 1.50

DISTANCES

COTES

DISTANCES

COTES

179.30 12.00

DISTANCES

COTES

DISTANCES

COTES

179.21 14.50

DISTANCES

COTES

DISTANCES

COTES

179.17 15.50

DISTANCES

COTES

DISTANCES

COTES

177.94 17.96

DISTANCES

COTES

177.80

27.20


ASSISE	DISTANCES	COTES	DISTANCES			COTES	DISTANCES	COTES	DISTANCES	COTES
			1	2	3					
177.72	-16.24	178.48	17.00			179.85				
		177.98	-16.00			179.80				
		177.98	-16.00			179.80				
		178.48	-15.50			179.80				
		178.52	-14.50			179.80				
177.86	-12.00	178.61	-12.00			179.39	-14.36			
						179.27	-14.09			
178.20	-1.50	178.95	-1.50			178.94	-3.53			
						178.64	-1.74			
178.20	1.50	178.95	1.50			178.19	1.02			
178.55	12.00	179.30	12.00							
178.69	16.45	179.21	14.50							
		179.17	15.50							
		177.94	17.96							

PROFIL 149

G2PIS

S = 3475.000
 ZTN = 178.206
 ZPRO= 178.310

ECHS=1/
 ECHZ=1/
 PC = 174.0
 LICENCE , 1570

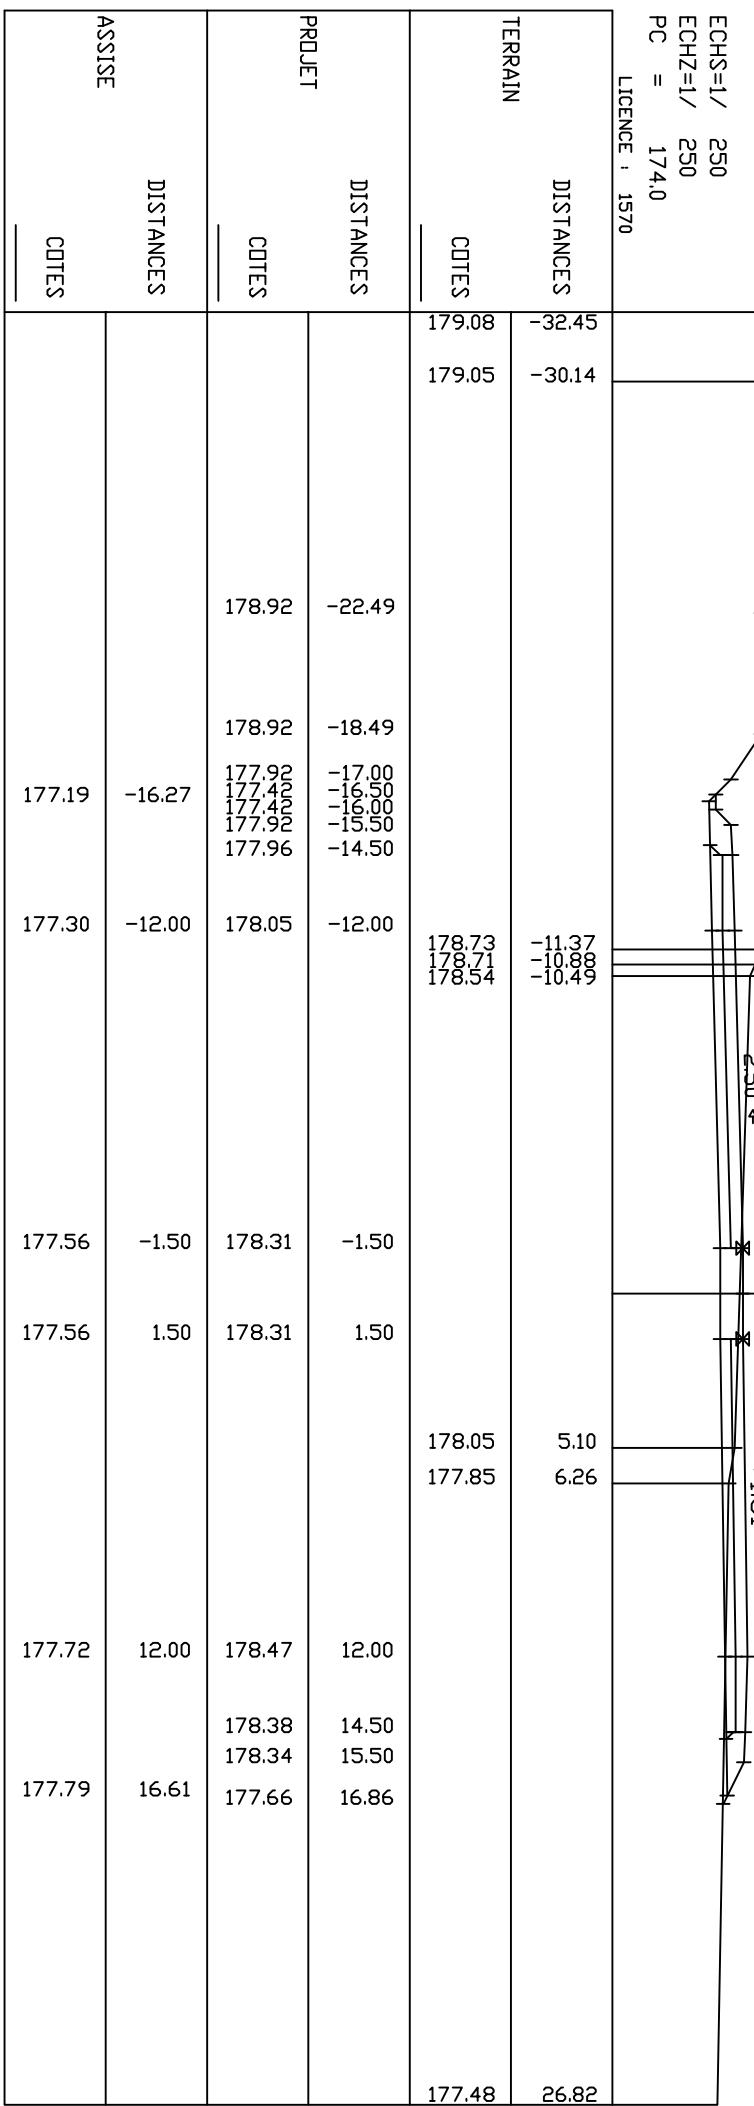

PROFIL 150

G2PIS

S = 3500.000
 ZTN = 177.671
 ZPRO= 177.668

ECH\$=1/
 ECHZ=1/
 PC = 174.0
 LICENCE , 1570

TERRAIN

DISTANCES

COTES

178.23 -32.54

DISTANCES

COTES

178.14 -27.39

TERRAIN

DISTANCES

COTES

178.07 -22.19

TERRAIN

DISTANCES

COTES

178.07 -18.19

TERRAIN

DISTANCES

COTES

177.28 -17.00

TERRAIN

DISTANCES

COTES

176.78 -16.50

TERRAIN

DISTANCES

COTES

176.78 -16.00

TERRAIN

DISTANCES

COTES

177.28 -15.50

TERRAIN

DISTANCES

COTES

177.32 -14.50

TERRAIN

DISTANCES

COTES

176.55 -16.27

TERRAIN

DISTANCES

COTES

178.07 -12.00

TERRAIN

DISTANCES

COTES

176.66 -12.00

TERRAIN

DISTANCES

COTES

176.92 1.50

TERRAIN

DISTANCES

COTES

176.92 -1.50

TERRAIN

DISTANCES

COTES

176.89 12.00

TERRAIN

DISTANCES

COTES

176.88 16.19

TERRAIN

DISTANCES

COTES

177.67 1.50

TERRAIN

DISTANCES

COTES

177.64 12.00

TERRAIN

DISTANCES

COTES

177.55 14.50

TERRAIN

DISTANCES

COTES

177.51 15.50

TERRAIN

DISTANCES

COTES

177.07 16.38

TERRAIN

DISTANCES

COTES

177.19 26.73

TERRAIN

DISTANCES

COTES

177.14 14.28

TERRAIN

DISTANCES

COTES

177.05 14.79

TERRAIN

DISTANCES

COTES

177.19 6.89

TERRAIN

DISTANCES

COTES

177.41 7.62

TERRAIN

DISTANCES

COTES

176.89 12.00

TERRAIN

DISTANCES

COTES

176.88 16.19

TERRAIN

DISTANCES

COTES

176.92 1.50

TERRAIN

DISTANCES

COTES

176.93 -1.20

TERRAIN

DISTANCES

COTES

176.66 -12.00

TERRAIN

DISTANCES

COTES

176.55 -16.27

TERRAIN

DISTANCES

COTES

176.92 -1.50

TERRAIN

DISTANCES

COTES

176.93 -1.20

TERRAIN

DISTANCES

COTES

176.66 -12.00

TERRAIN

DISTANCES

COTES

176.55 -16.27

TERRAIN

DISTANCES

COTES

TERRAIN

DISTANCES

COTES

176.93 -1.20

TERRAIN

DISTANCES

COTES

176.66 -12.00

TERRAIN

DISTANCES

COTES

176.55 -16.27

TERRAIN

DISTANCES

COTES


176.92 -1.50


TERRAIN

DISTANCES

COTES

176.93 -1.20

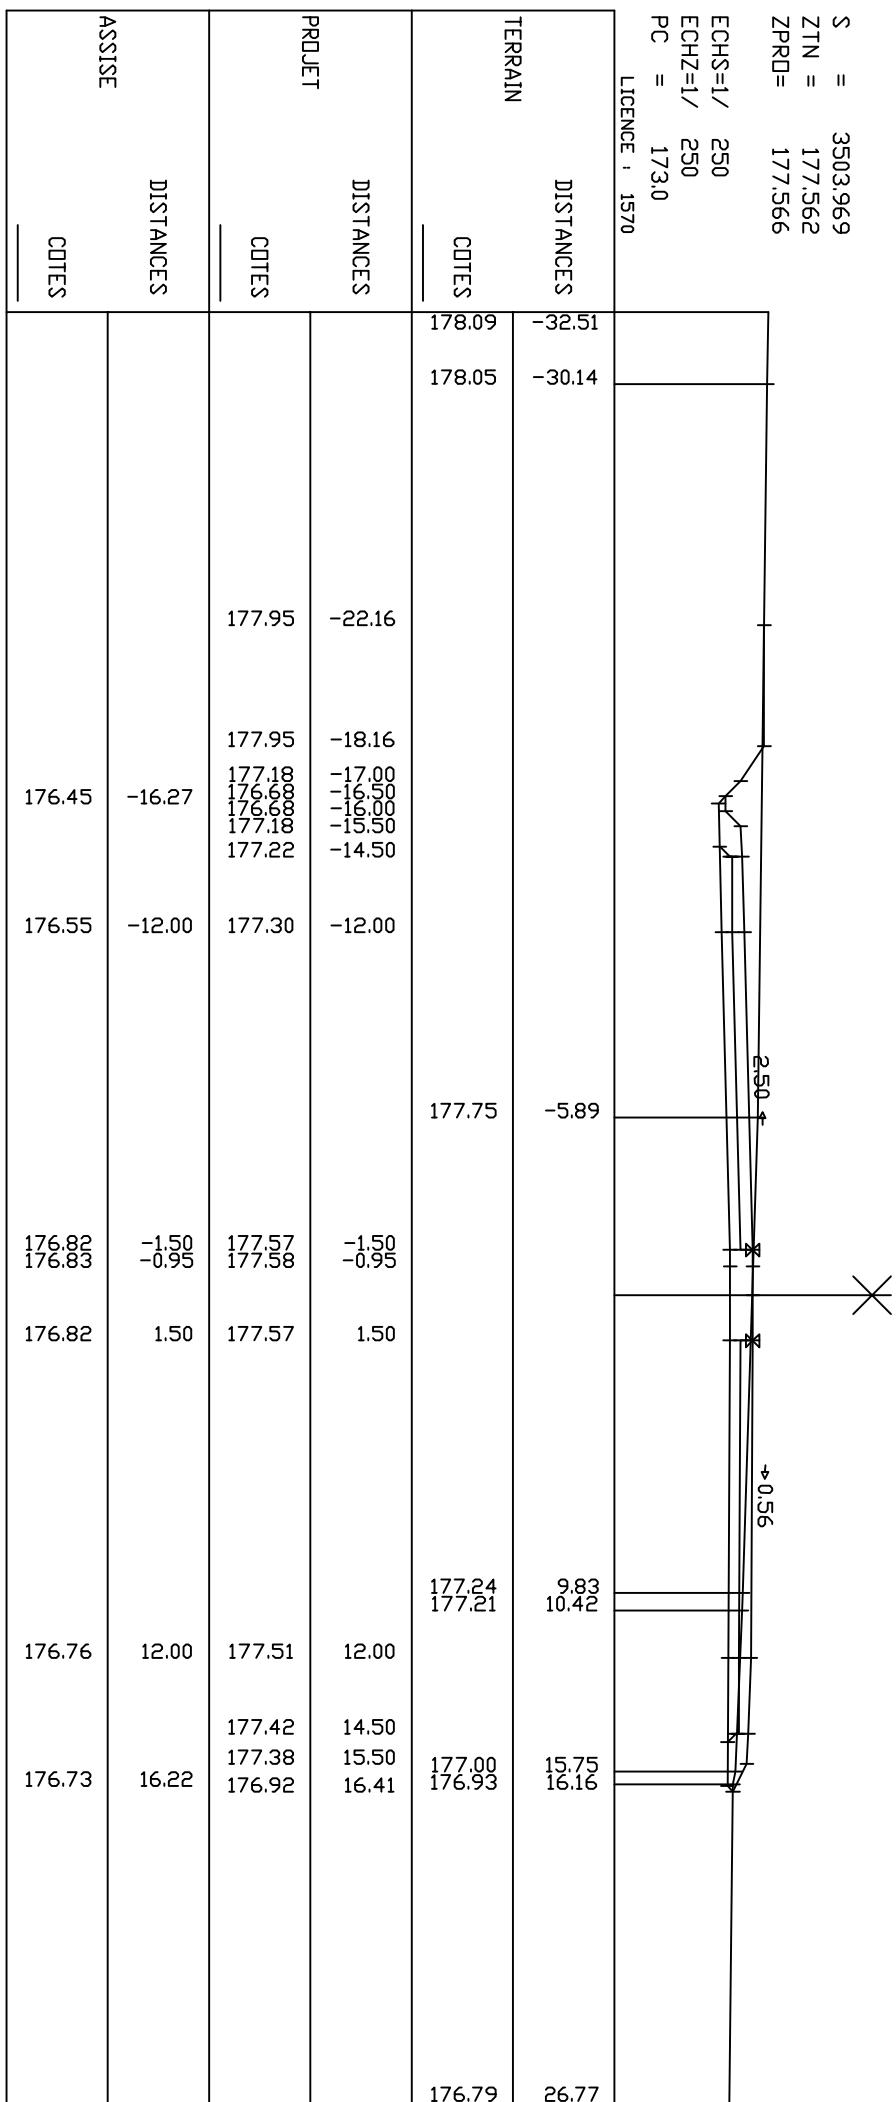

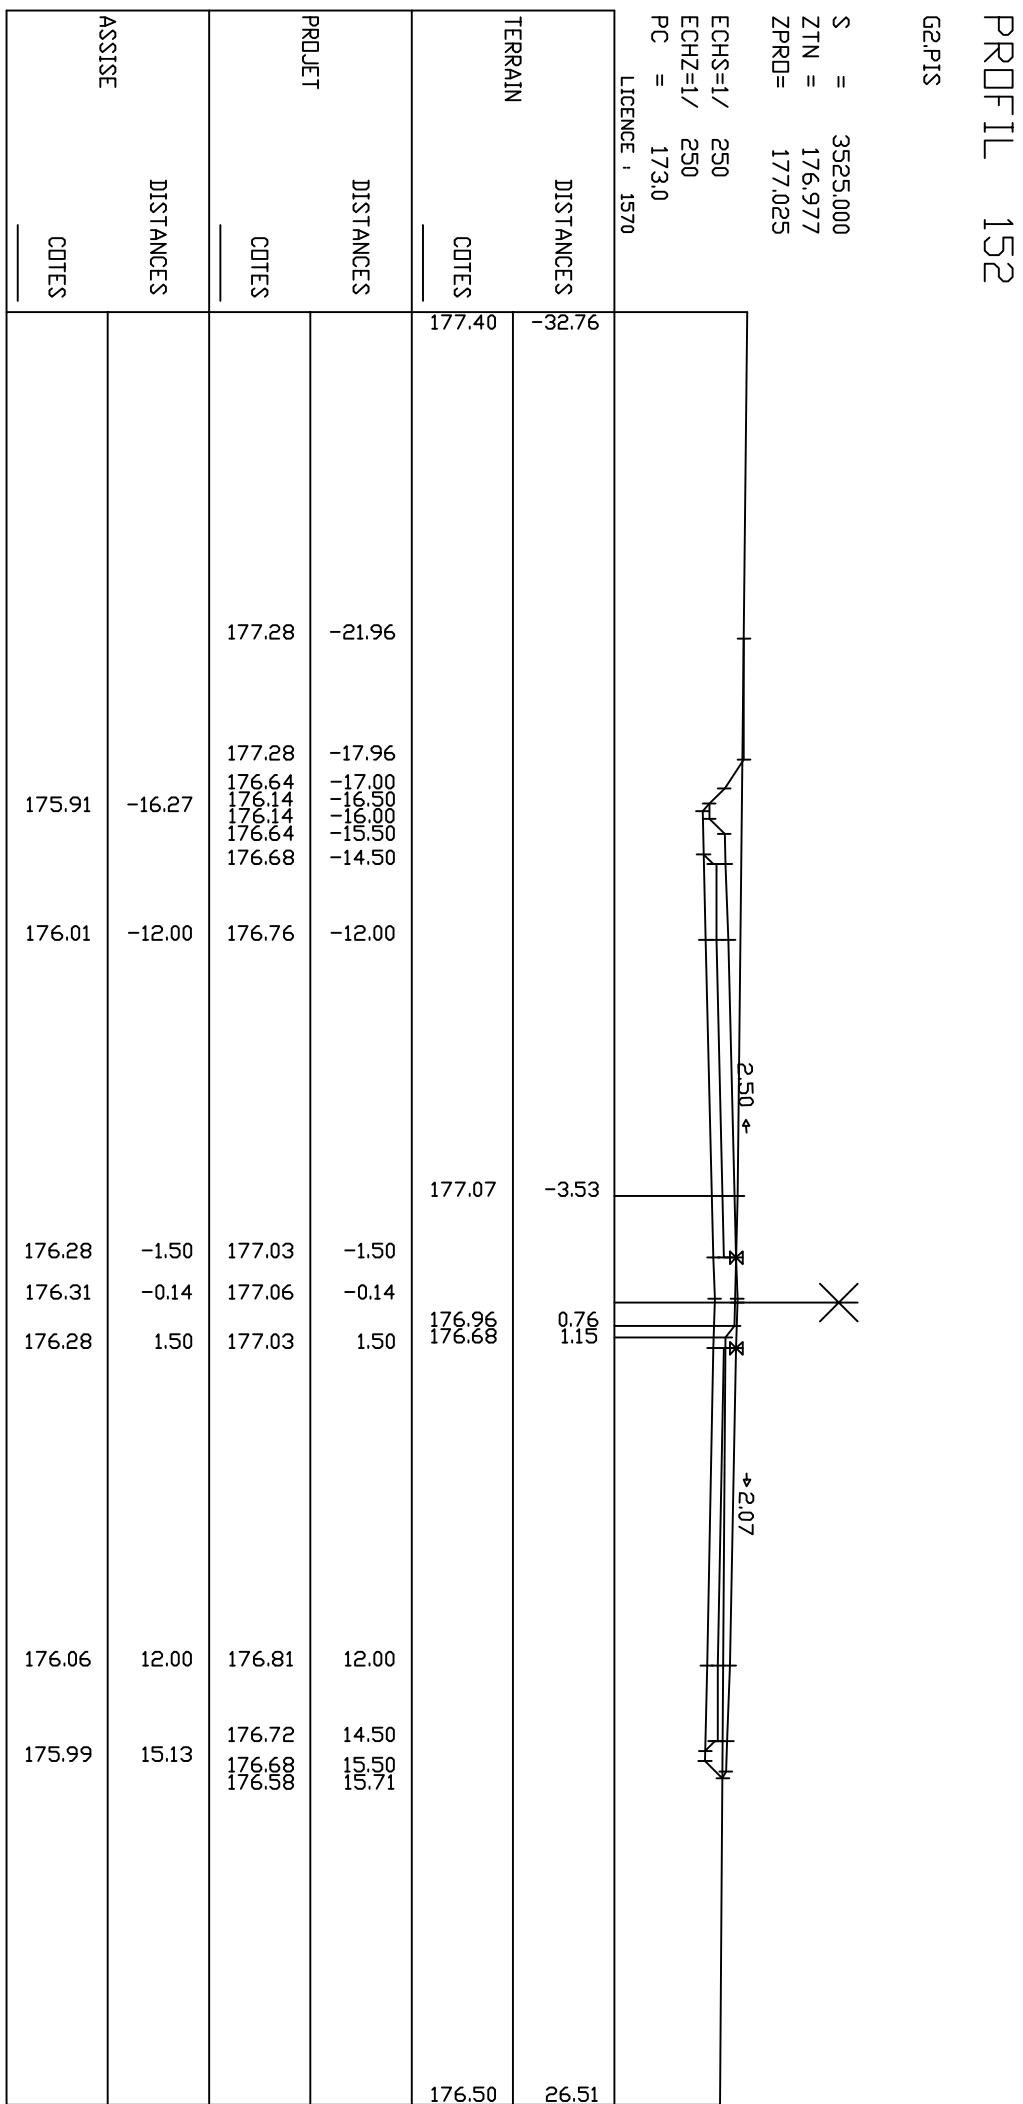

PROFIL 153

G2PIS

S = 3531.074
 ZTN = 176.869
 ZPRO= 176.869

ECH\$=1/
 ECHZ=1/
 PC = 173.0
 LICENCE , 1570

TERRAIN

DISTANCES

COTES

		177.16	-29.79
		177.09	
		176.98	
			-23.28
			-23.12



		176.73	29.48

PROJET

DISTANCES

COTES

DISTANCES

COTES

ASSISE

COTES

175.75	-16.27	176.97 176.48 175.98 176.48 176.52	-17.74 -17.00 -16.00 -15.50 -14.50
--------	--------	--	--

175.86	-12.00	176.61	-12.00
--------	--------	--------	--------

176.12	-1.50	176.87	-1.50
176.16	0.00	176.91	0.00
176.12	1.50	176.87	1.50

175.86	12.00	176.61	12.00
--------	-------	--------	-------

175.75	16.27	176.52 176.48 175.98 175.98 176.48 176.77	14.50 15.50 16.00 16.50 17.00 17.43
--------	-------	--	--

		176.77	21.43
--	--	--------	-------